



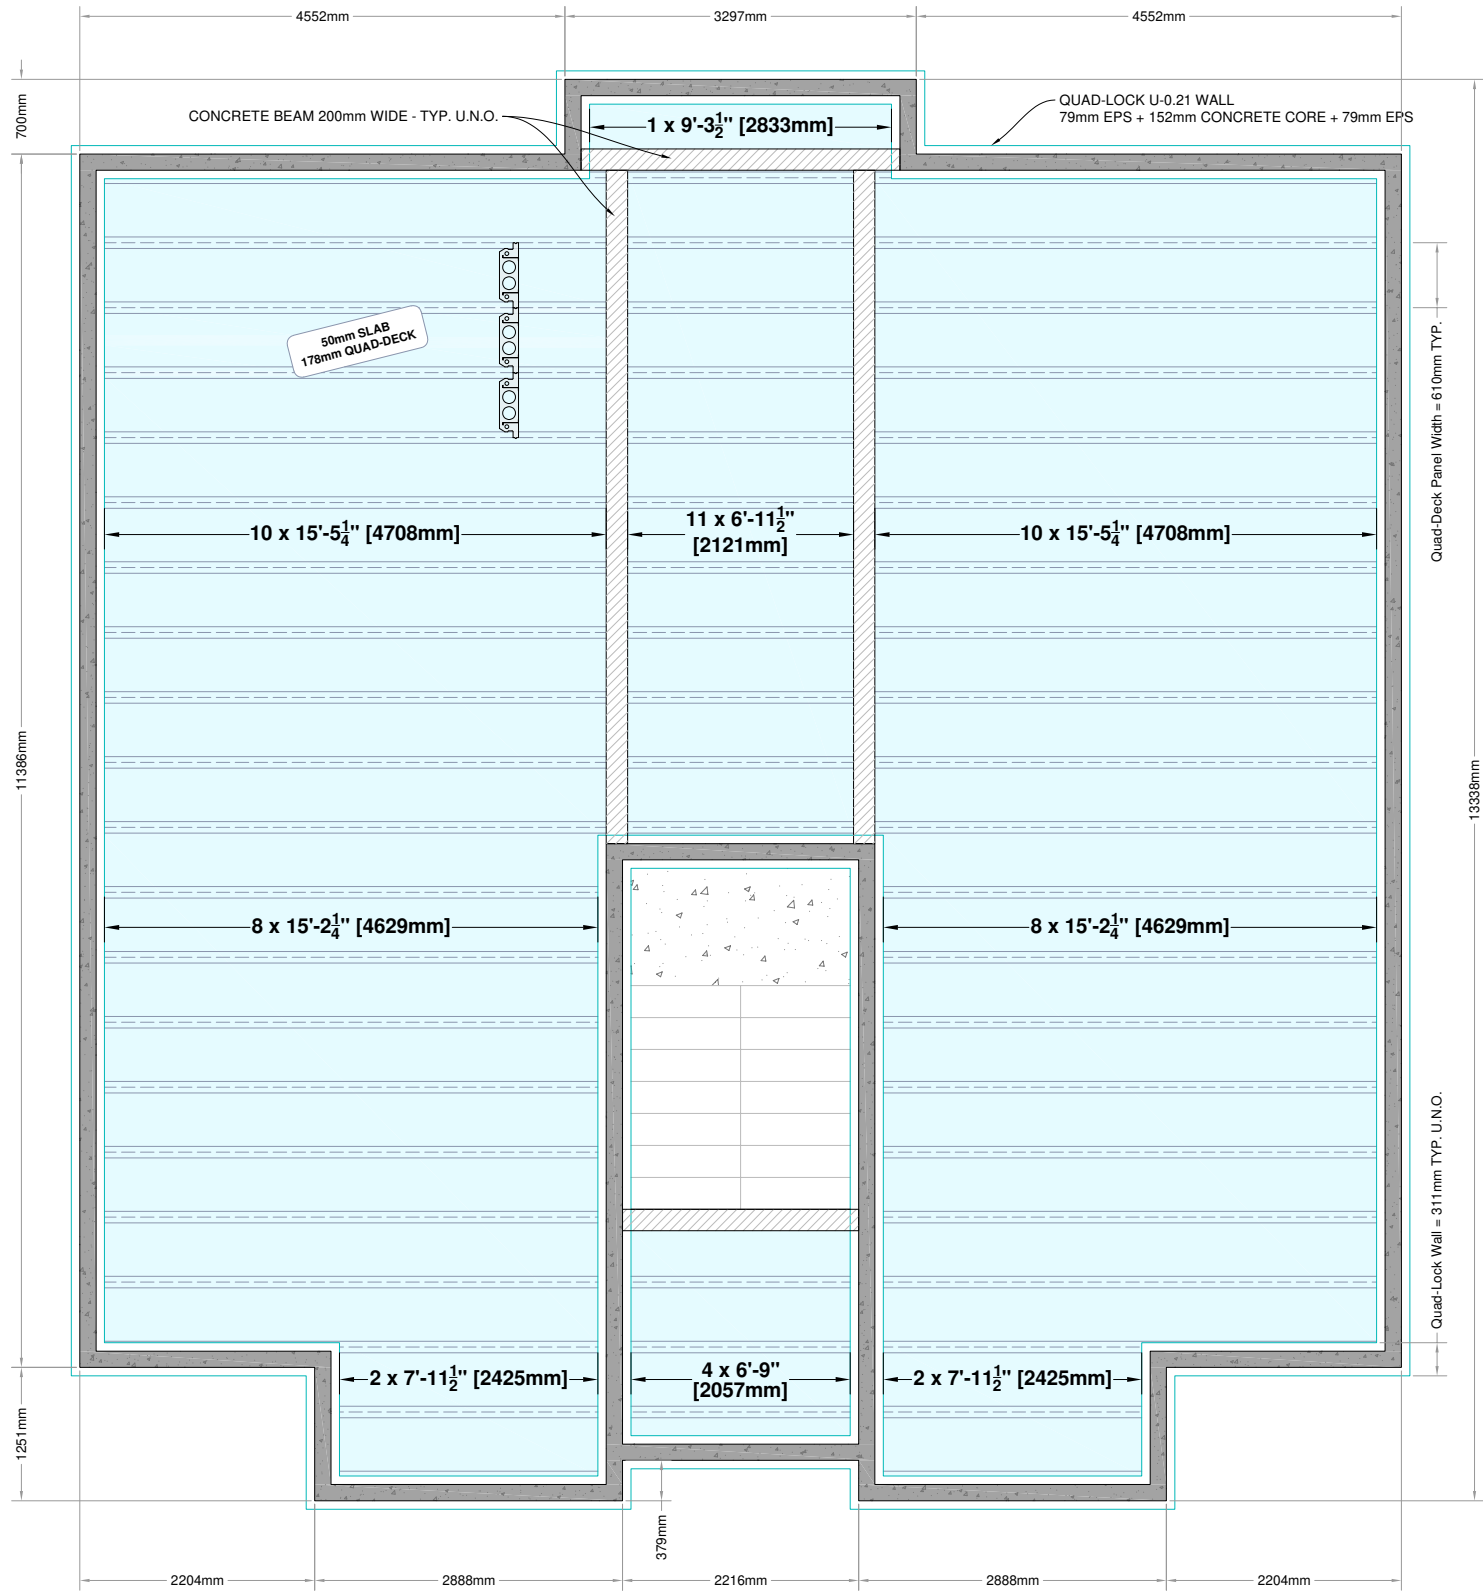

1 SECOND FLOOR PLAN
Scale: N.T.S.

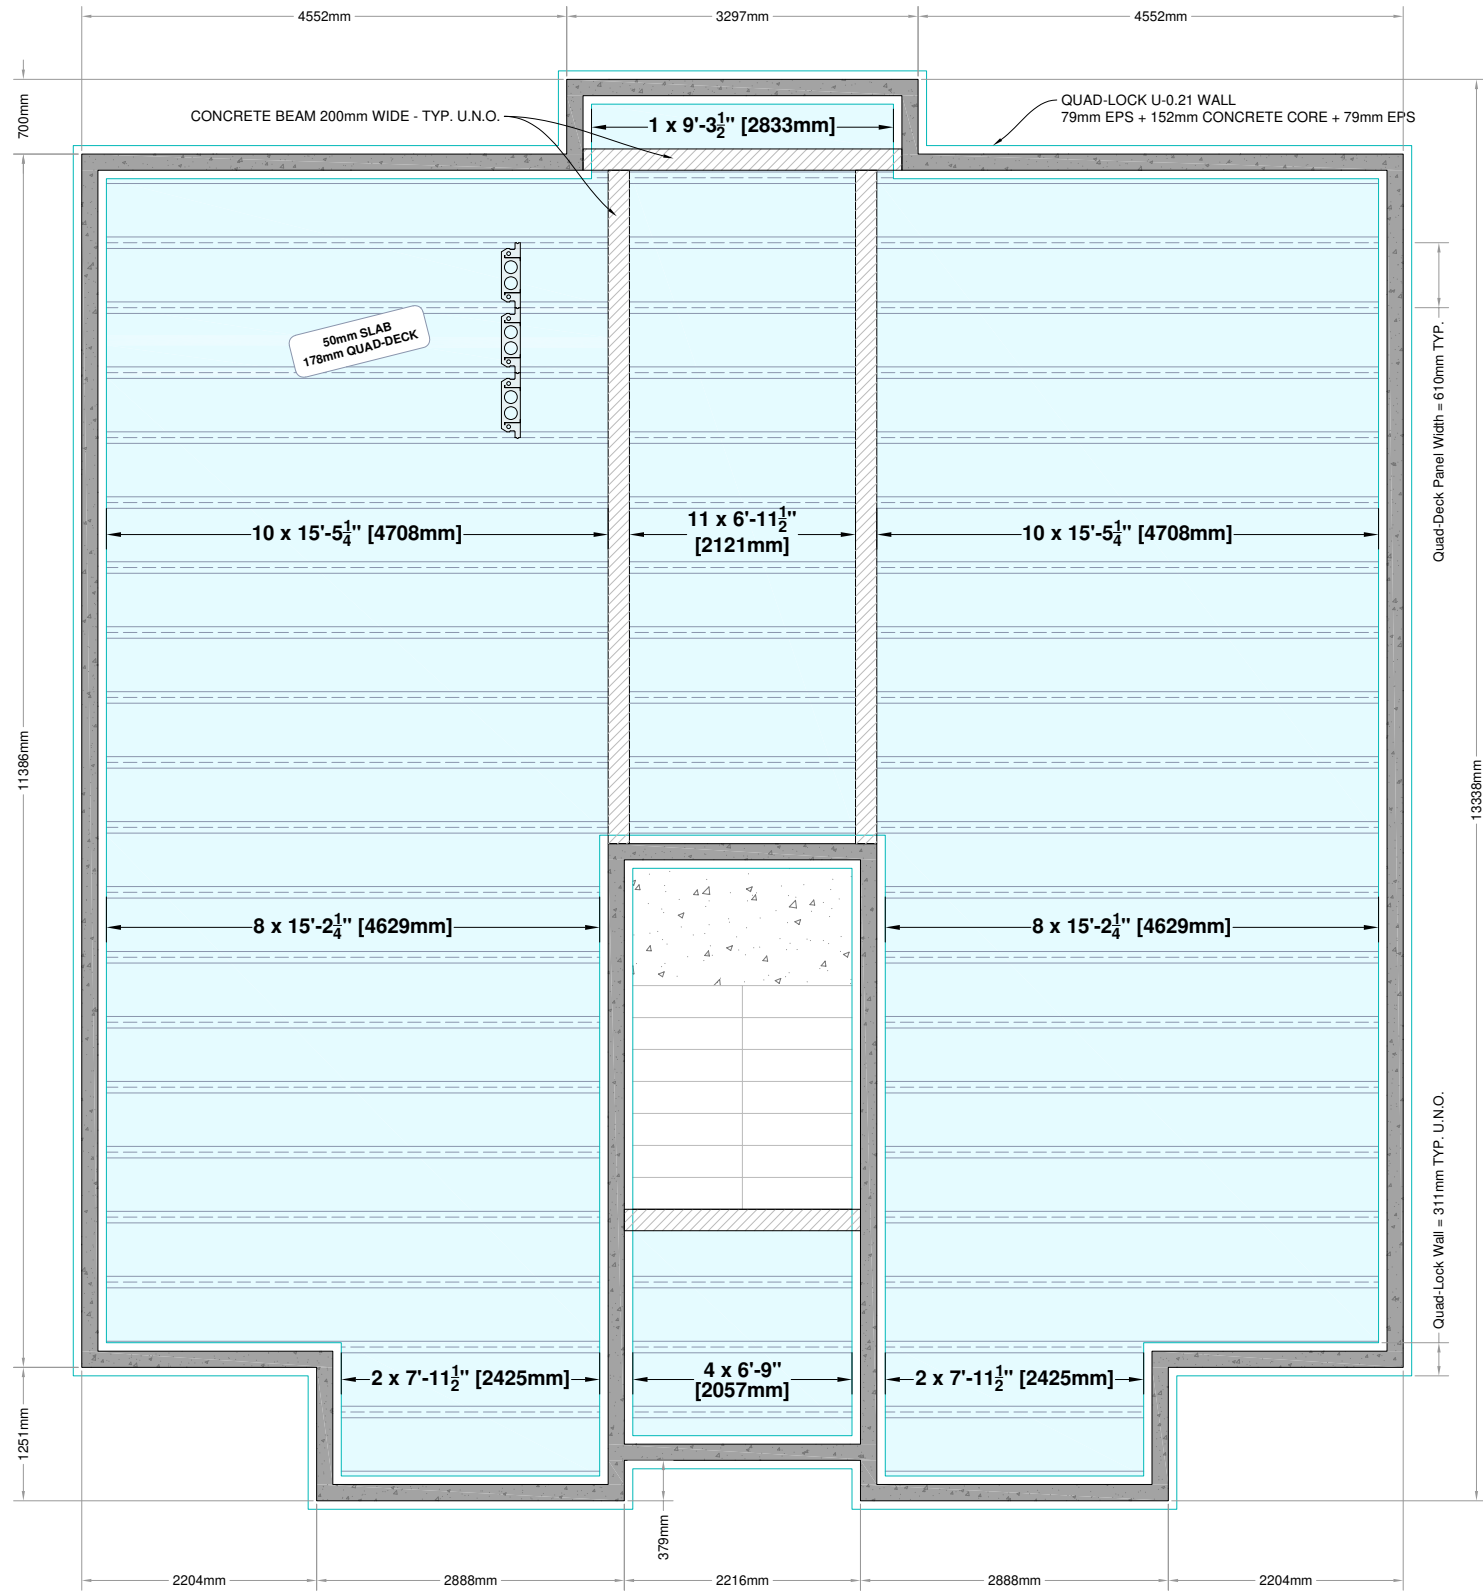

2 ROOF LEVEL PLAN
Scale: N.T.S.



Quad-Lock Building Systems
19402 - 56th Avenue Surrey, BC V3S 6K4
Canada
888.711.5625 - Toll Free
604.590.3111 | 604.534.1212 - fax
www.quadlock.com

- THIS DESIGN AND DRAWINGS IS AND AT ALL TIMES REMAINS THE EXCLUSIVE PROPERTY OF QUAD-LOCK BUILDING SYSTEMS AND CANNOT BE USED WITHOUT THE DESIGNER'S WRITTEN CONSENT.
- DO NOT SCALE DRAWINGS.
- WRITTEN DIMENSIONS ALWAYS TAKE PRECEDENCE OVER SCALED DIMENSIONS.
- ALL DIMENSIONS MUST BE VERIFIED BY THE CONTRACTOR.
- QUAD-LOCK BUILDING SYSTEMS DOES NOT ASSUME LIABILITY.
- PLEASE ADVISE QUAD-LOCK BUILDING SYSTEMS IF ANY DISCREPANCIES ARE FOUND OR EXPLANATIONS REQUIRED.
- ALL WORK MUST COMPLY WITH LOCAL BY-LAW AND CURRENT BUILDING CODE.
- ALL INSTALLATION DETAILS ARE CONTROLLED BY ICF INSTALLER & G.C.


No.	DATE (yyyy-mm-dd)	DESCRIPTION
R E V I S I O N S		

EMPRESA AZZUL


CANTON SAN RAFAEL, CONDOMINIO RECREATIVO, LOMAS DE SAN BLAS, CALLE MAJAHUAL,
POLIGONO 6, NUMERO 19, LA LIBERTAD COSTA. DEPARTAMENTO DE LA LIBERTAD

SECOND FLOOR & ROOF LAYOUT


DATE:	2025-09-16	DRAWN BY:	Z. PROSTRAN
SCALE:	AS SHOWN	APPROVED BY:	
SHEET SIZE:	11"x17"	APPROVED ON:	YYYY-MM-DD
PROJECT No:	K018750	SHEET:	Q-1
DRAWING No:			

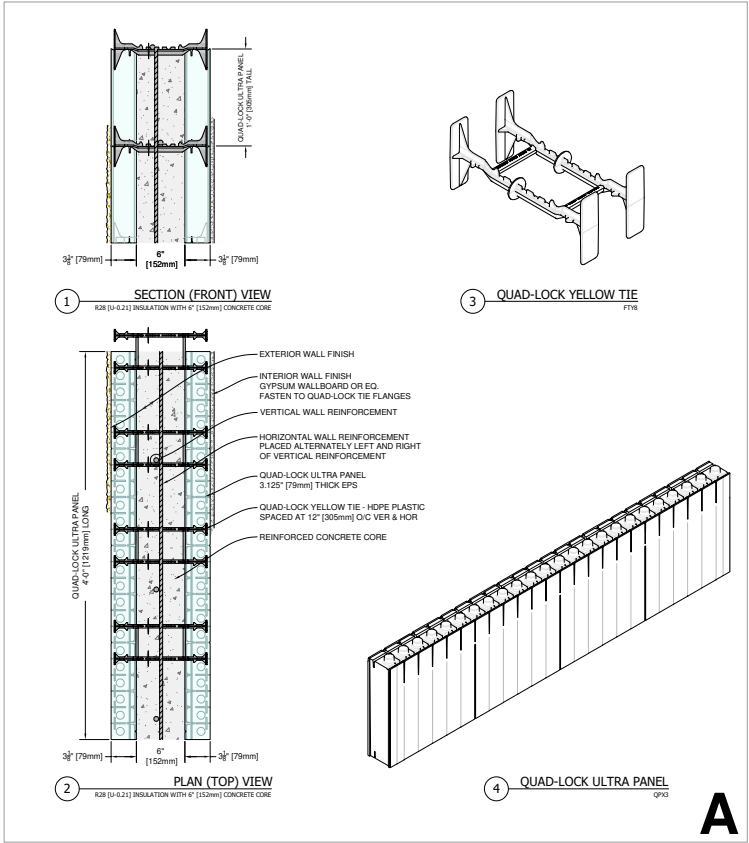


A

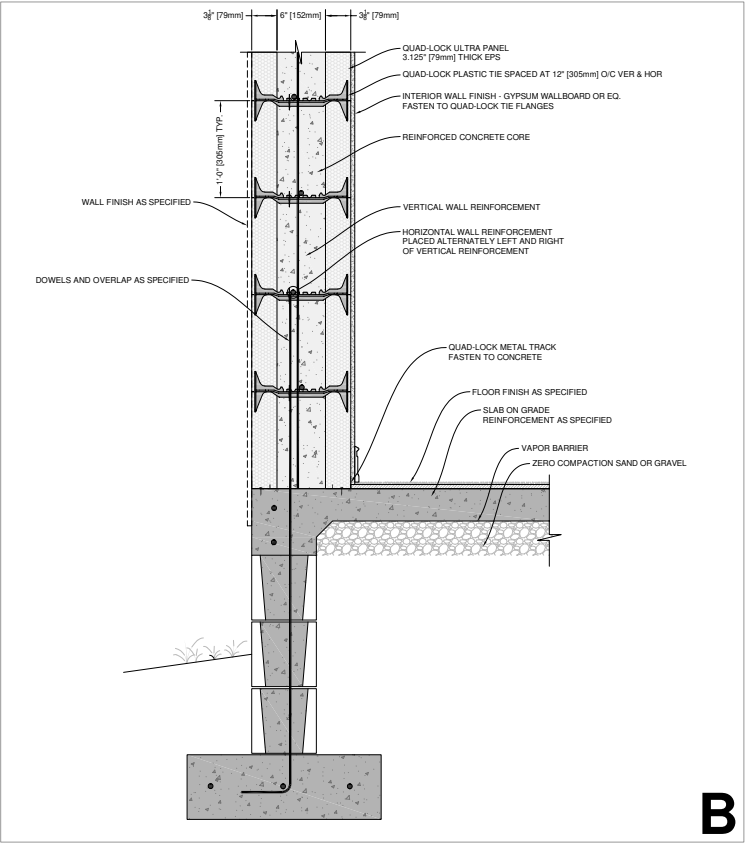


B

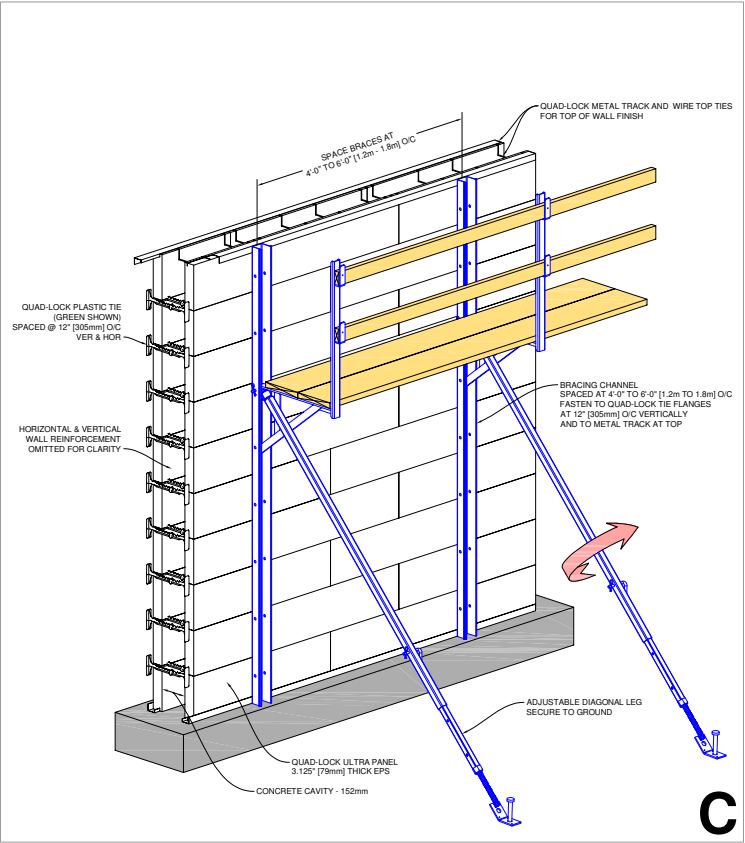


C

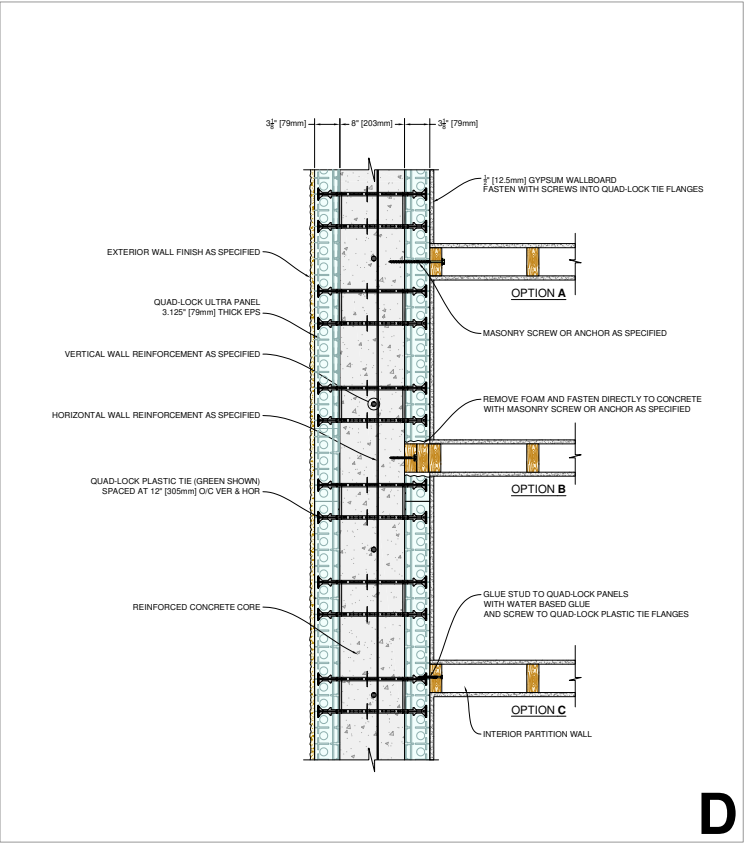


D

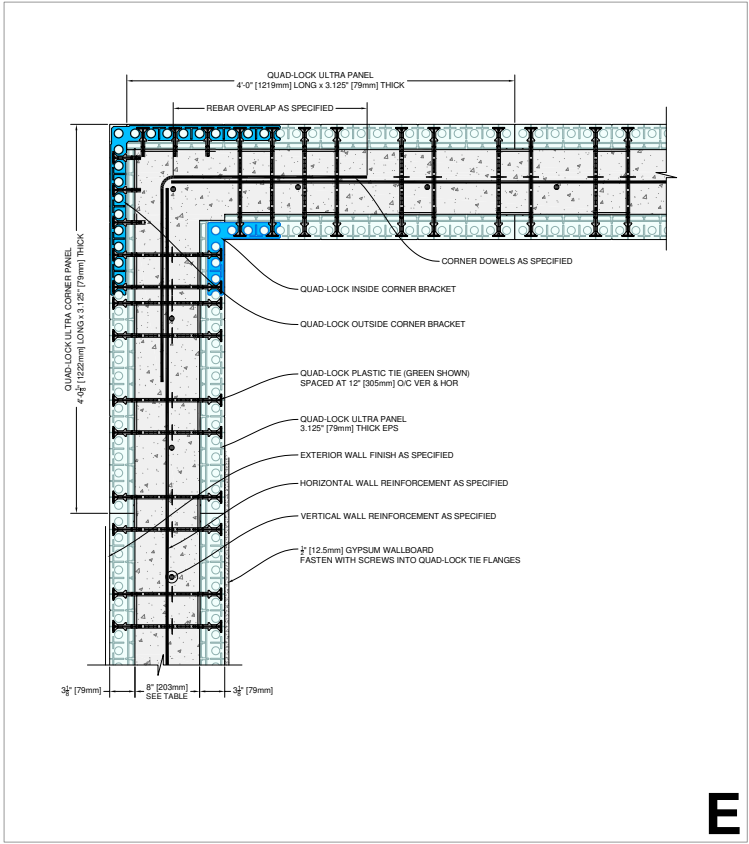


E

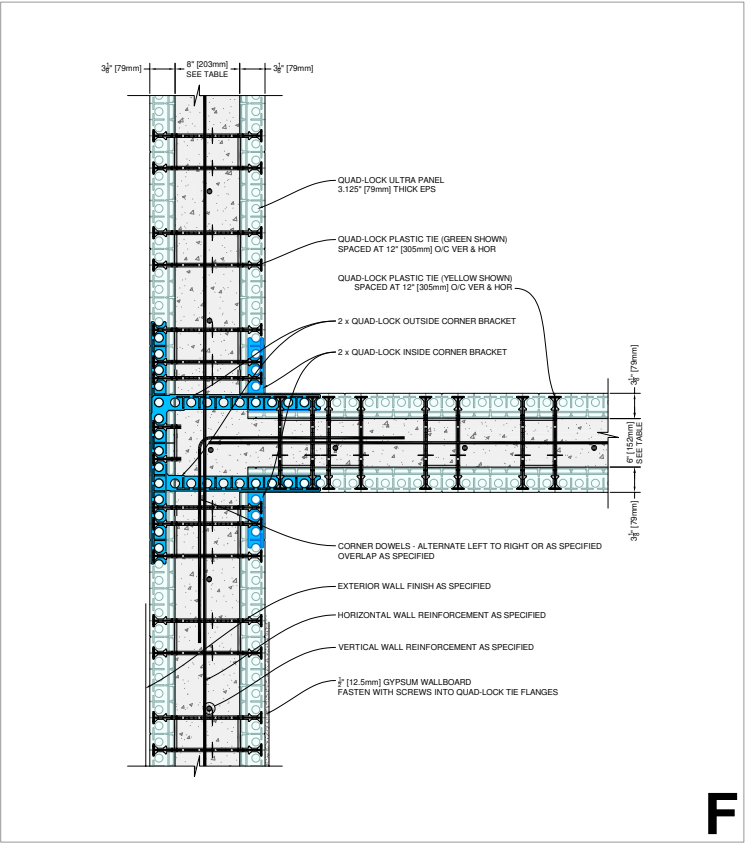

F

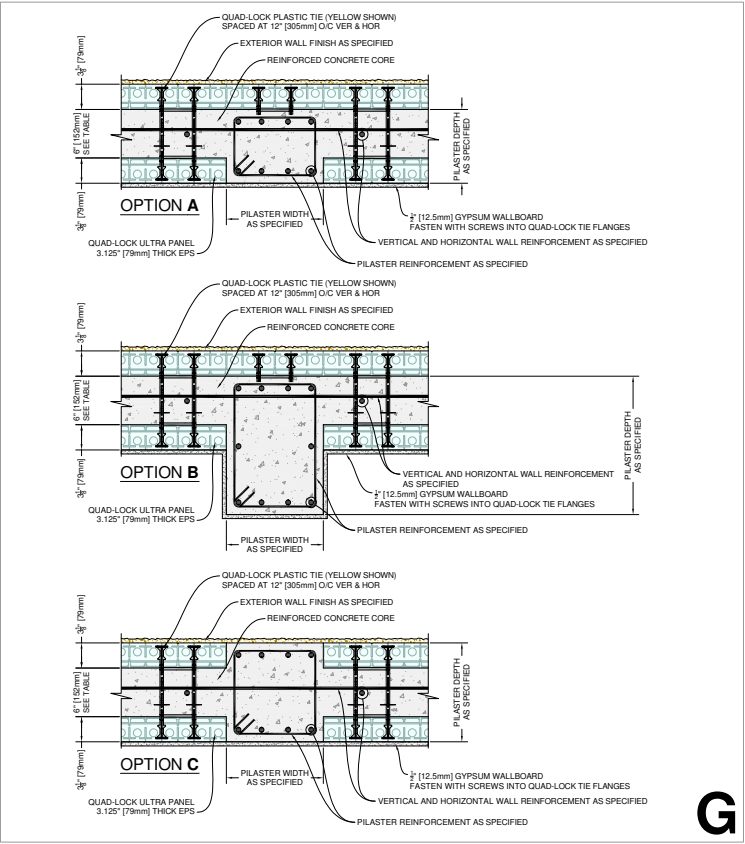

G

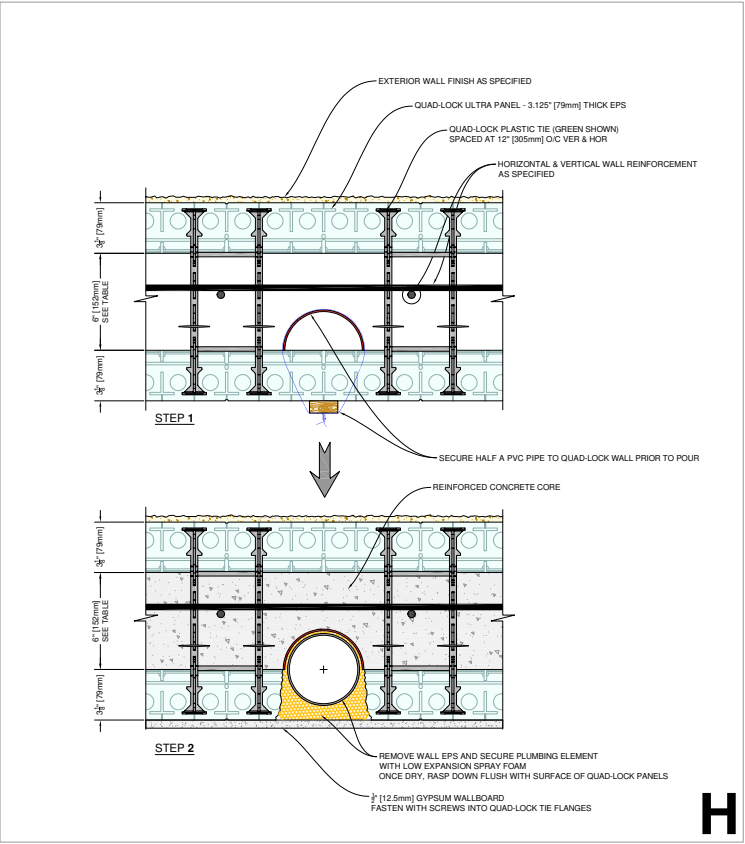

H

QUAD-LOCK
Building Systems

Quad-Lock Building Systems
19402 - 56th Avenue Surrey, BC V3S 6K4
Canada
888.711.5625 - Toll Free
604.590.3111 | 604.534.1212 - fax
www.quadlock.com

IT IS THE RESPONSIBILITY OF THE USER TO COMPLY WITH ALL APPLICABLE REGULATIONS AND BUILDING CODE REQUIREMENTS CONCERNING THE USE OF THESE PRODUCTS.
IT IS FURTHER THE RESPONSIBILITY OF THE USER TO RESEARCH AND UNDERSTAND SAFE METHODS OF USE AND HANDLING OF THESE PRODUCTS.

- THIS DESIGN AND DRAWINGS IS AND AT ALL TIMES REMAINS THE EXCLUSIVE PROPERTY OF QUAD-LOCK BUILDING SYSTEMS AND CANNOT BE USED WITHOUT THE DESIGNER'S WRITTEN CONSENT.
- DO NOT SCALE DRAWINGS.
- WRITTEN DIMENSIONS ALWAYS TAKE PRECEDENCE OVER SCALED DIMENSIONS.
- ALL DIMENSIONS MUST BE VERIFIED BY THE CONTRACTOR.
- QUAD-LOCK BUILDING SYSTEMS DOES NOT ASSUME LIABILITY.
- PLEASE ADVISE QUAD-LOCK BUILDING SYSTEMS IF ANY DISCREPANCIES ARE FOUND OR EXPLANATIONS REQUIRED.
- ALL WORK MUST COMPLY WITH LOCAL BY-LAW AND CURRENT BUILDING CODE.
- ALL INSTALLATION DETAILS ARE CONTROLLED BY ICF INSTALLER & G.C.


No.	DATE (yyyy-mm-dd)	DESCRIPTION
R E V I S I O N S		

EMPRESA AZZUL


CANTON SAN RAFAEL, CONDOMINIO RECREATIVO, LOMAS DE SAN BLAS, CALLE MAJAHUAL, POLIGONO 6, NUMERO 19, LA LIBERTAD COSTA. DEPARTAMENTO DE LA LIBERTAD

QUAD-LOCK WALL DETAILS


DATE:	2025-09-16	DRAWN BY:	Z. PROSTRAN
SCALE:	AS SHOWN	APPROVED BY:	
SHEET SIZE:	11"x17"	APPROVED ON:	YYYY-MM-DD
PROJECT No:	K018750	SHEET:	Q-2
DRAWING No:			

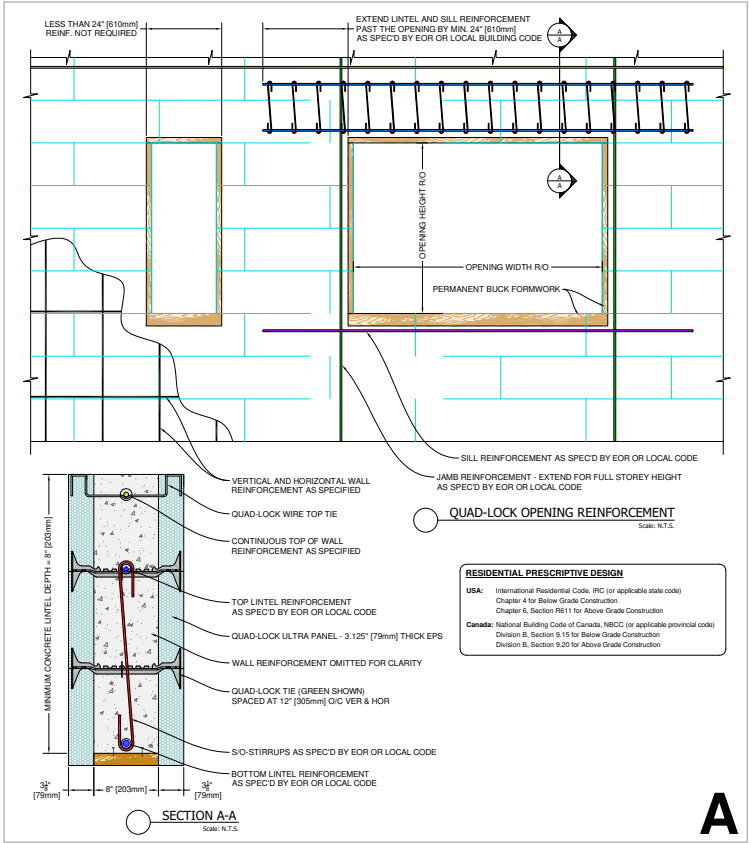


A

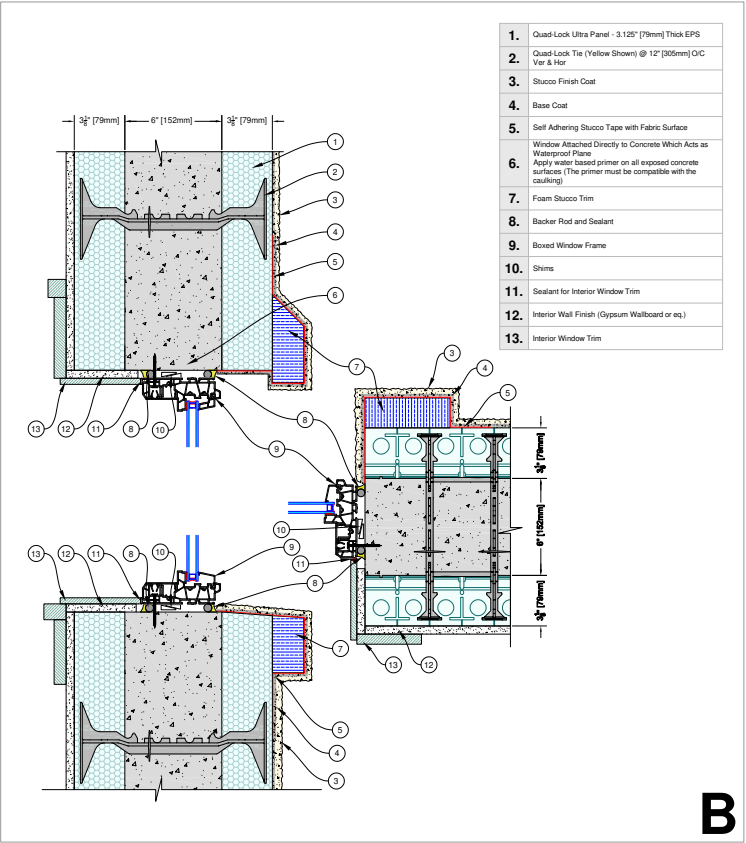


B

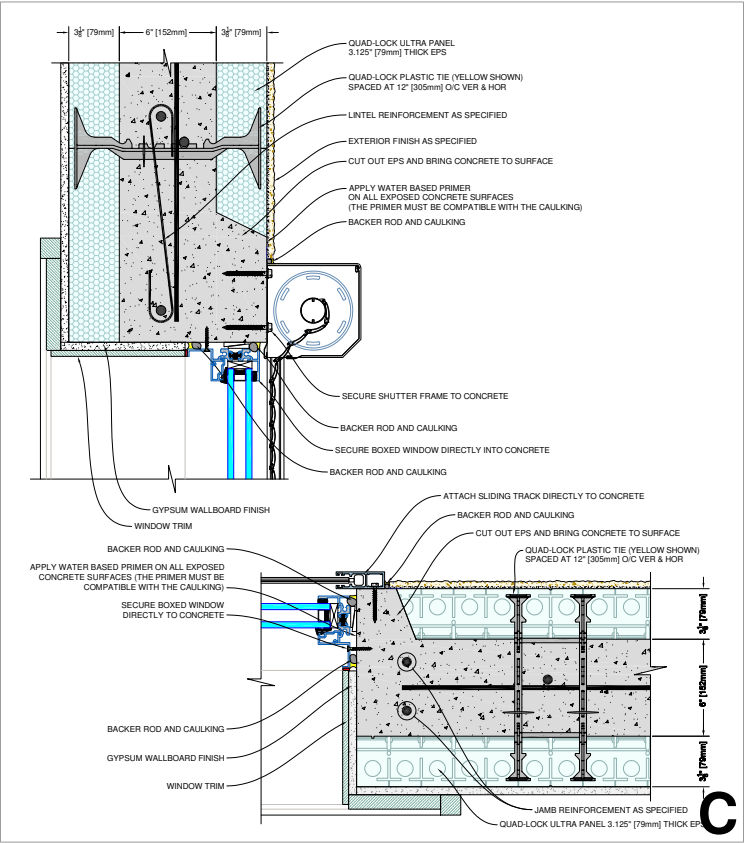


C

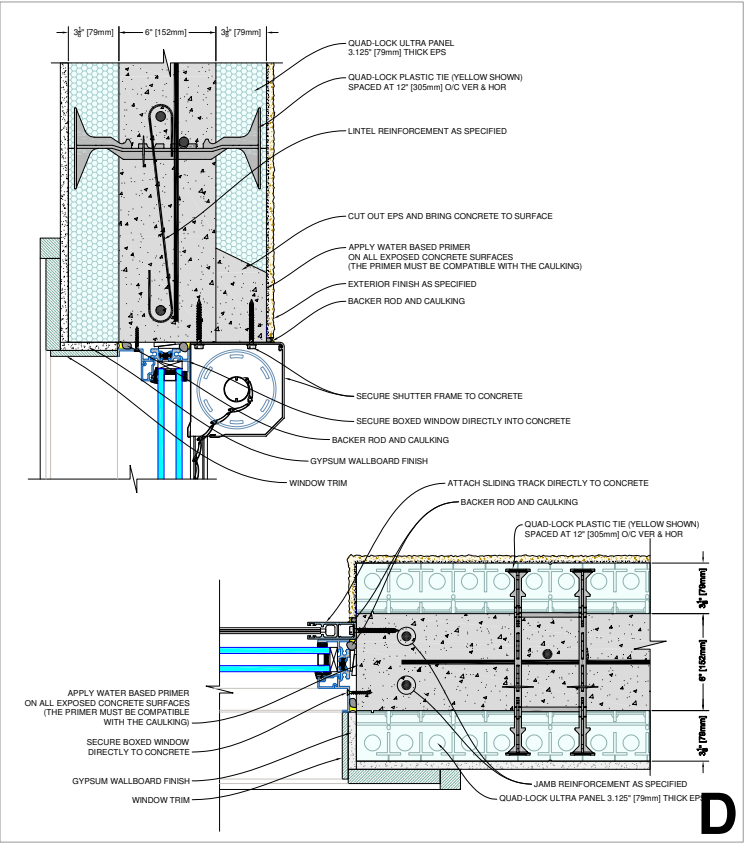


D

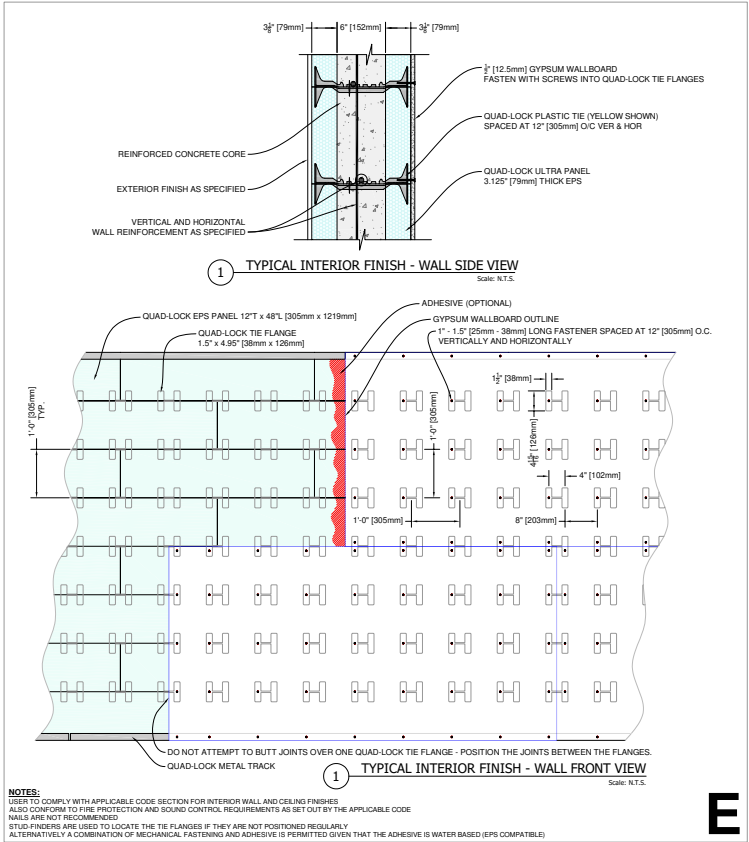


E

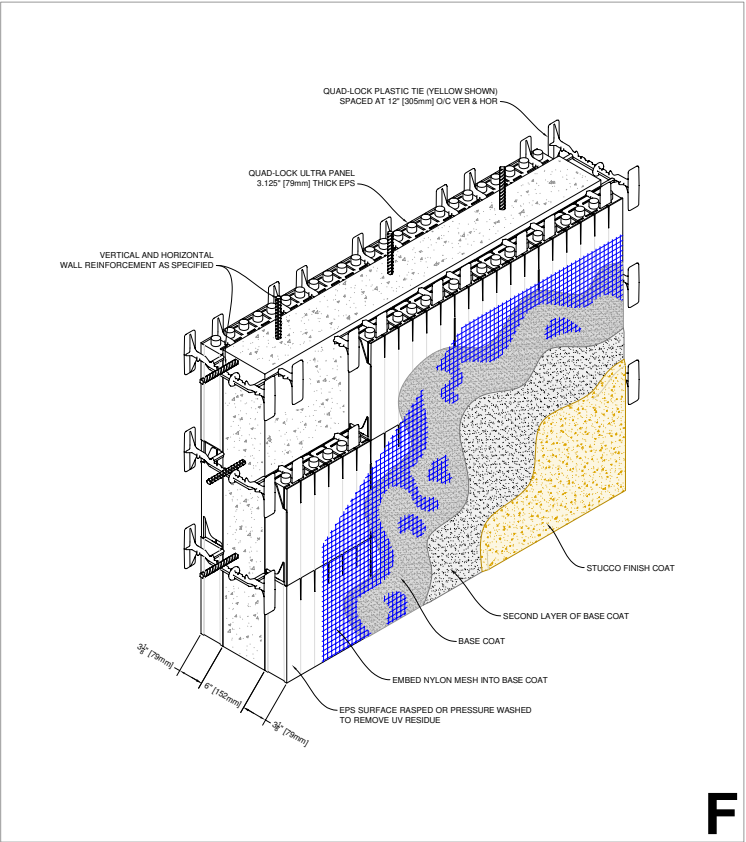

F

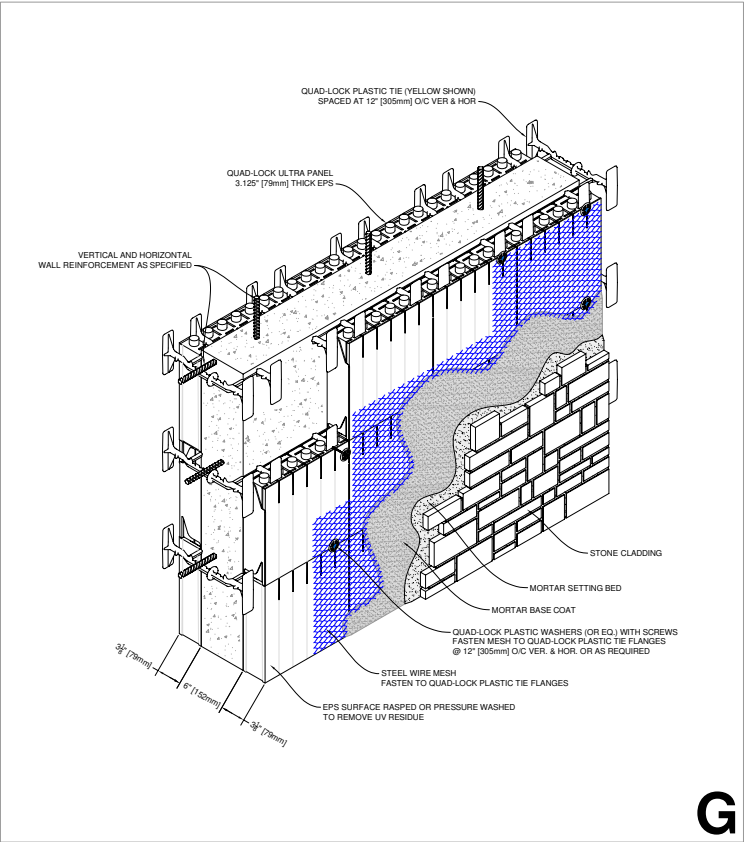

G

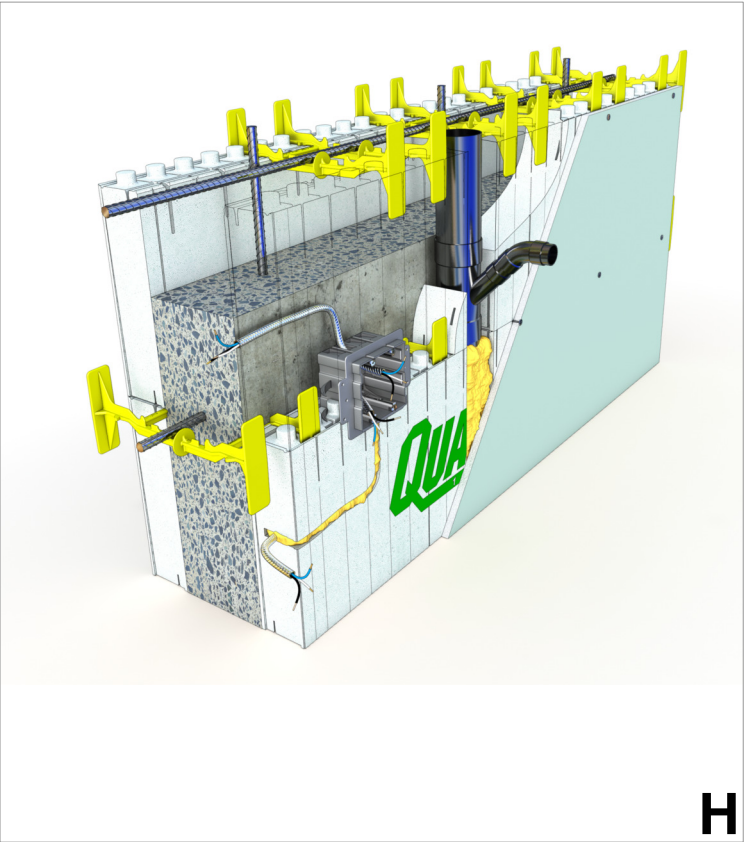

H

QUAD-LOCK
Building Systems

Quad-Lock Building Systems
19402 - 56th Avenue Surrey, BC V3S 6K4
Canada
888.711.5625 - Toll Free
604.590.3111 | 604.534.1212 - fax
www.quadlock.com

IT IS THE RESPONSIBILITY OF THE USER TO COMPLY WITH ALL APPLICABLE REGULATIONS AND BUILDING CODE REQUIREMENTS CONCERNING THE USE OF THESE PRODUCTS.
IT IS FURTHER THE RESPONSIBILITY OF THE USER TO RESEARCH AND UNDERSTAND SAFE METHODS OF USE AND HANDLING OF THESE PRODUCTS.

- THIS DESIGN AND DRAWINGS IS AND AT ALL TIMES REMAINS THE EXCLUSIVE PROPERTY OF QUAD-LOCK BUILDING SYSTEMS AND CANNOT BE USED WITHOUT THE DESIGNER'S WRITTEN CONSENT.
- DO NOT SCALE DRAWINGS.
- WRITTEN DIMENSIONS ALWAYS TAKE PRECEDENCE OVER SCALED DIMENSIONS.
- ALL DIMENSIONS MUST BE VERIFIED BY THE CONTRACTOR.
- QUAD-LOCK BUILDING SYSTEMS DOES NOT ASSUME LIABILITY.
- PLEASE ADVISE QUAD-LOCK BUILDING SYSTEMS IF ANY DISCREPANCIES ARE FOUND OR EXPLANATIONS REQUIRED.
- ALL WORK MUST COMPLY WITH LOCAL BY-LAW AND CURRENT BUILDING CODE.
- ALL INSTALLATION DETAILS ARE CONTROLLED BY ICF INSTALLER & G.C.

No.	DATE (yyyy-mm-dd)	DESCRIPTION
R E V I S I O N S		


EMPRESA AZZUL

CANTON SAN RAFAEL, CONDOMINIO RECREATIVO, LOMAS DE SAN BLAS, CALLE MAJAHUAL,
POLIGONO 6, NUMERO 19, LA LIBERTAD COSTA. DEPARTAMENTO DE LA LIBERTAD


QUAD-LOCK OPENINGS & FINISH DETAILS

DATE:	2025-09-16	DRAWN BY:	Z. PROSTRAN
SCALE:	AS SHOWN	APPROVED BY:	
SHEET SIZE:	11"x17"	APPROVED ON:	YYYY-MM-DD
PROJECT No:	K018750	SHEET:	Q-3
DRAWING No:			




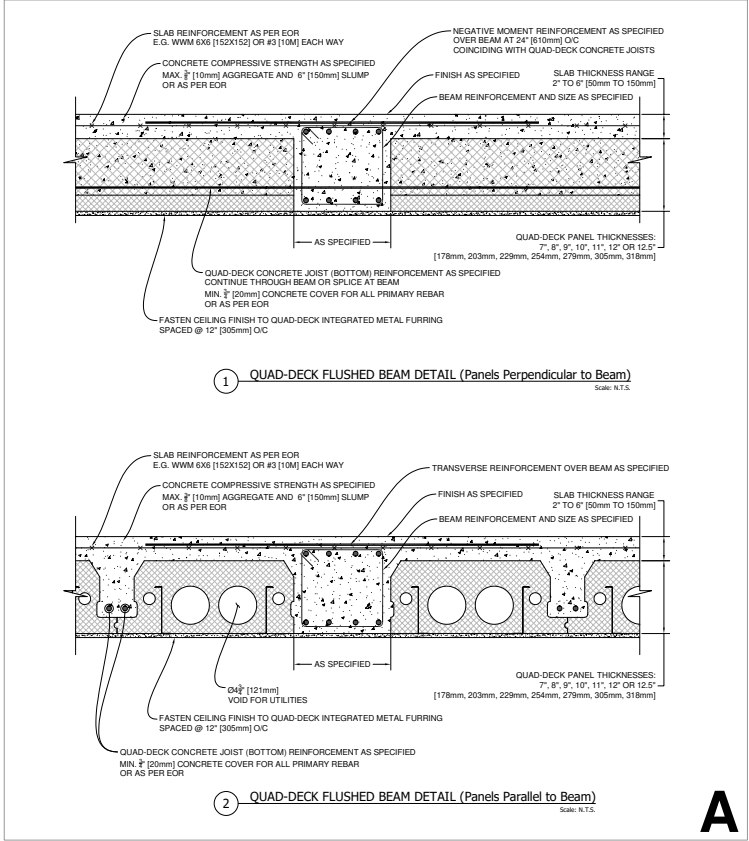


A

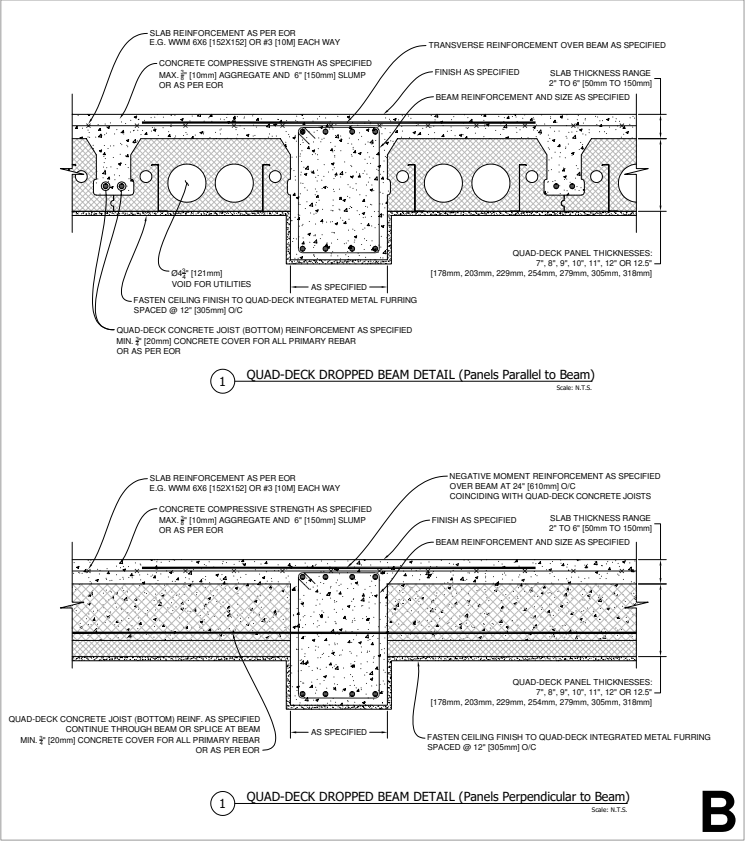


B

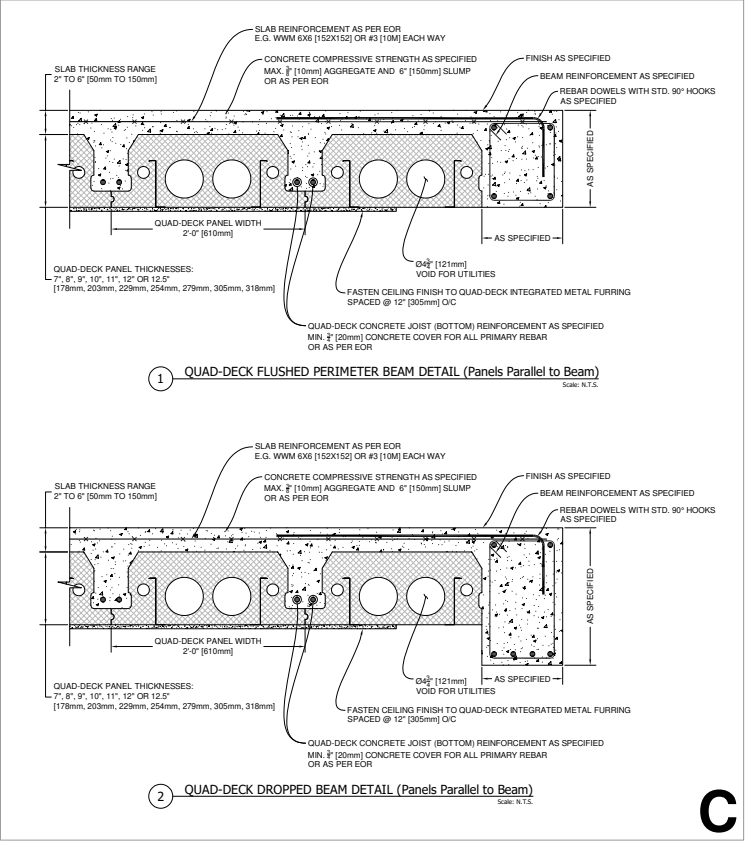


C

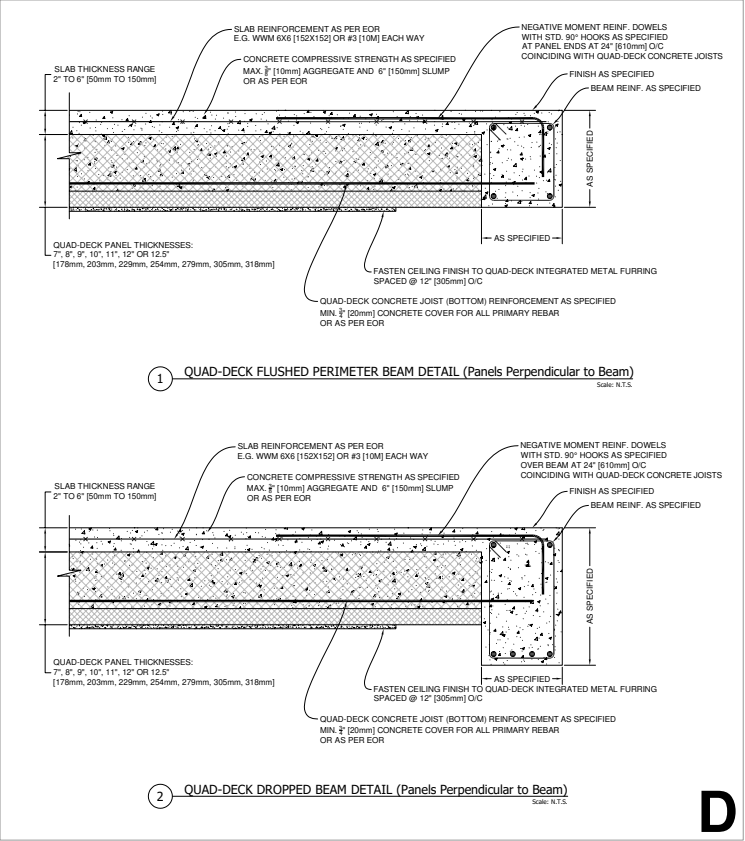


D

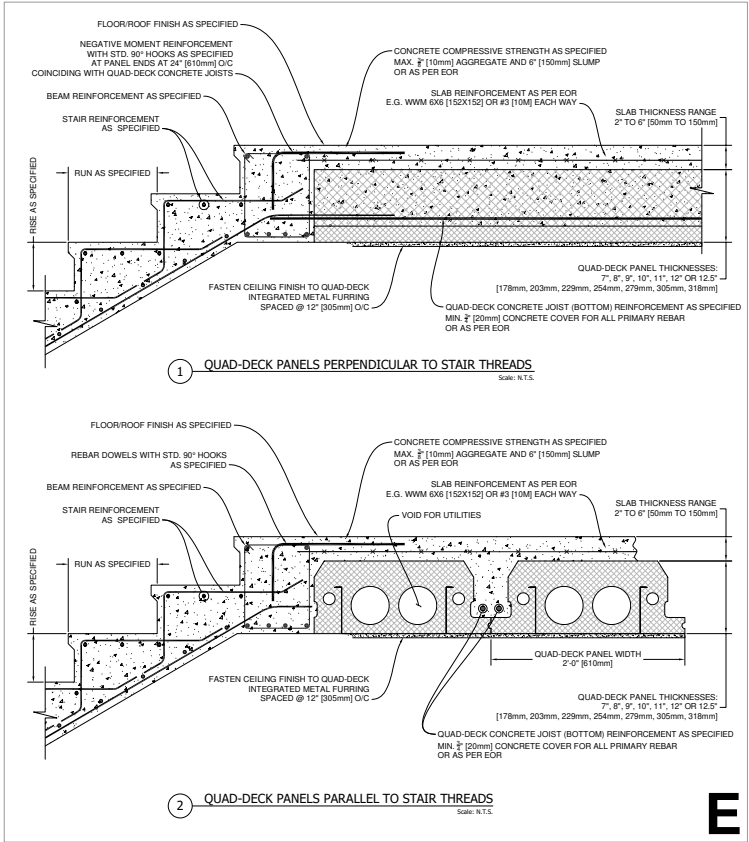


E

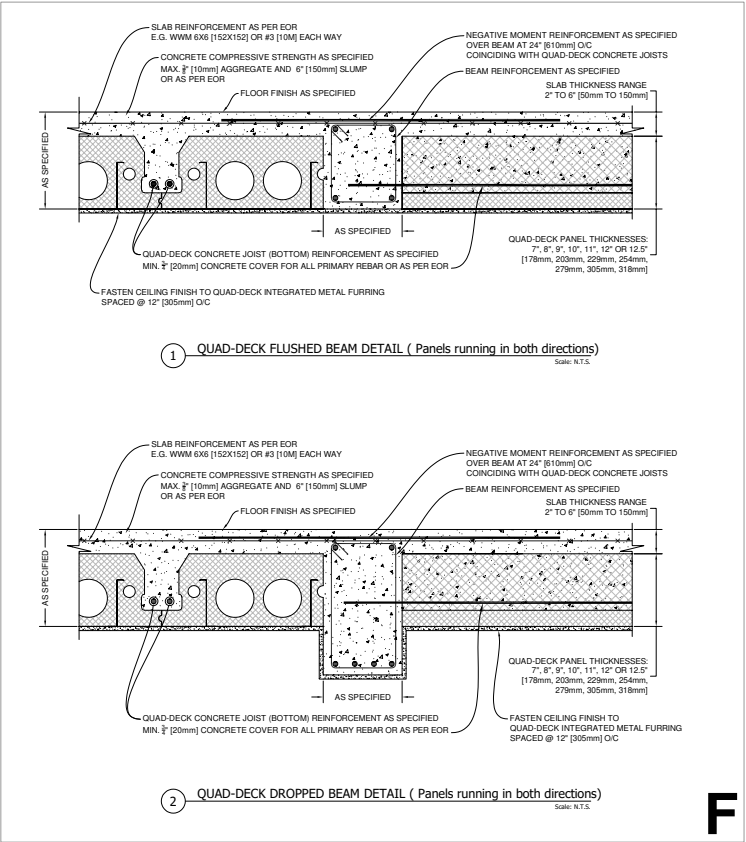

F

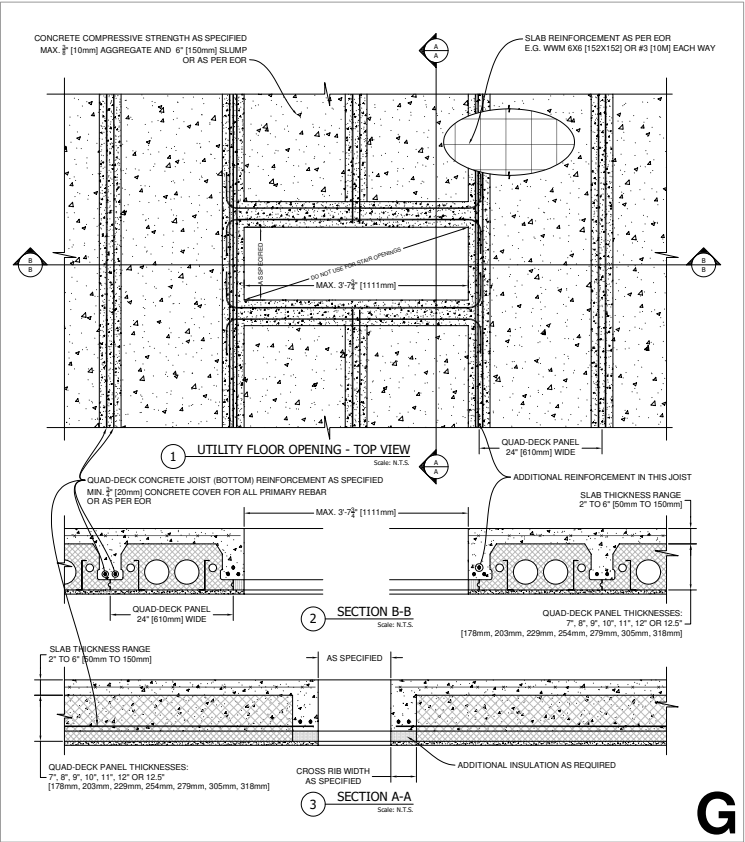

G

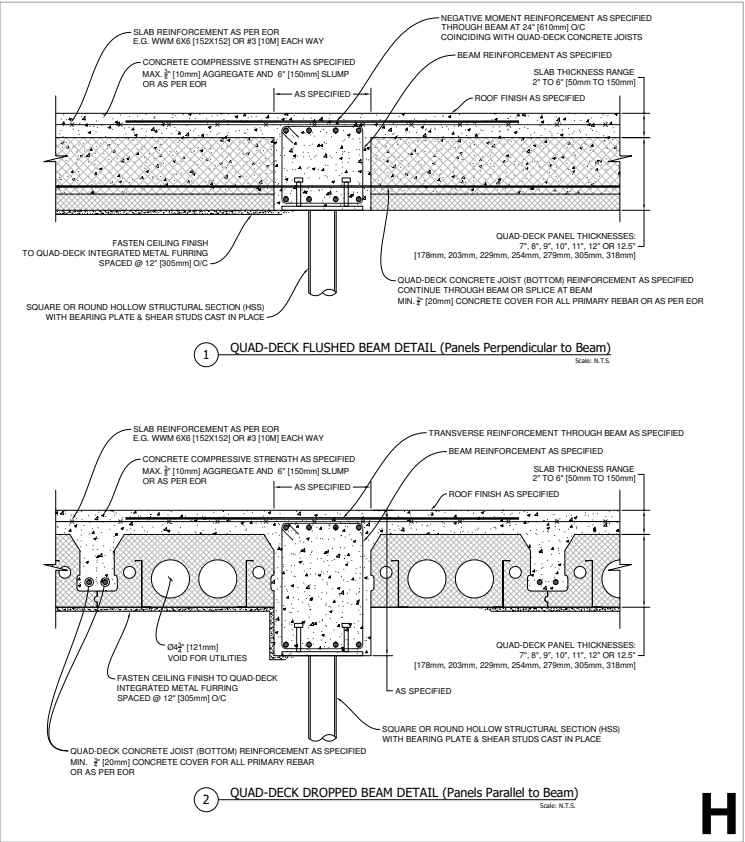

H

QUAD-LOCK
Building Systems

Quad-Lock Building Systems
19402 - 56th Avenue Surrey, BC V3S 6K4
Canada
888.711.5625 - Toll Free
604.590.3111 | 604.534.1212 - fax
www.quadlock.com

- THIS DESIGN AND DRAWINGS IS AND AT ALL TIMES REMAINS THE EXCLUSIVE PROPERTY OF QUAD-LOCK BUILDING SYSTEMS AND CANNOT BE USED WITHOUT THE DESIGNER'S WRITTEN CONSENT.
- DO NOT SCALE DRAWINGS.
- WRITTEN DIMENSIONS ALWAYS TAKE PRECEDENCE OVER SCALED DIMENSIONS.
- ALL DIMENSIONS MUST BE VERIFIED BY THE CONTRACTOR.
- QUAD-LOCK BUILDING SYSTEMS DOES NOT ASSUME LIABILITY.
- PLEASE ADVISE QUAD-LOCK BUILDING SYSTEMS IF ANY DISCREPANCIES ARE FOUND OR EXPLANATIONS REQUIRED.
- ALL WORK MUST COMPLY WITH LOCAL BY-LAW AND CURRENT BUILDING CODE.
- ALL INSTALLATION DETAILS ARE CONTROLLED BY ICF INSTALLER & G.C.


No.	DATE (yyyy-mm-dd)	DESCRIPTION
R E V I S I O N S		

EMPRESA AZZUL


CANTON SAN RAFAEL, CONDOMINIO RECREATIVO, LOMAS DE SAN BLAS, CALLE MAJAHUAL,
POLIGONO 6, NUMERO 19, LA LIBERTAD COSTA. DEPARTAMENTO DE LA LIBERTAD

QUAD-DECK FLOOR/ROOF DETAILS


DATE:	2025-09-16	DRAWN BY:	Z. PROSTRAN
SCALE:	AS SHOWN	APPROVED BY:	
SHEET SIZE:	11"x17"	APPROVED ON:	YYYY-MM-DD
PROJECT No:	K018750	SHEET:	Q-5
DRAWING No:			

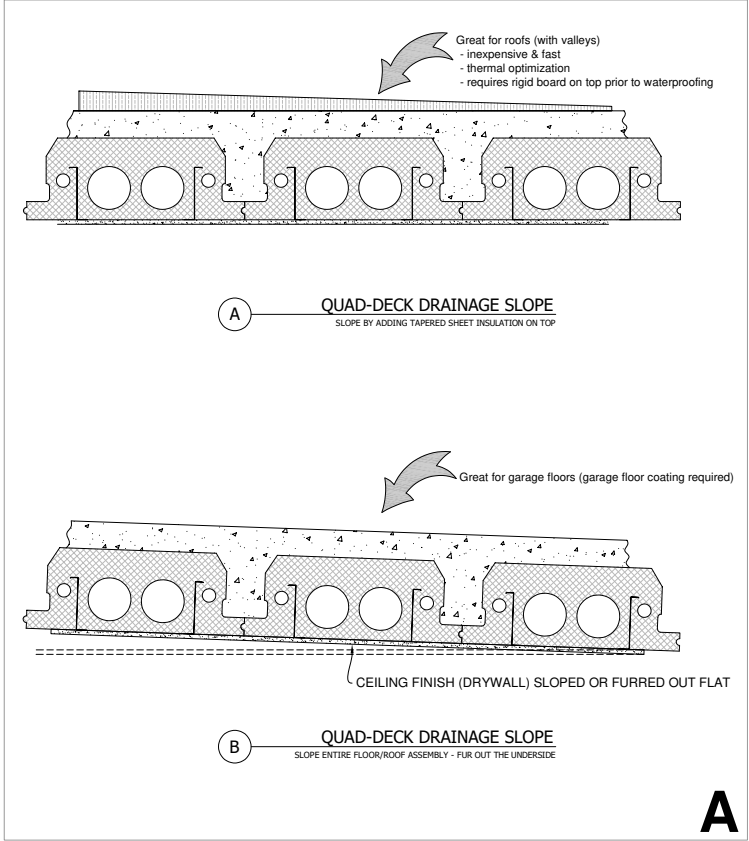


A

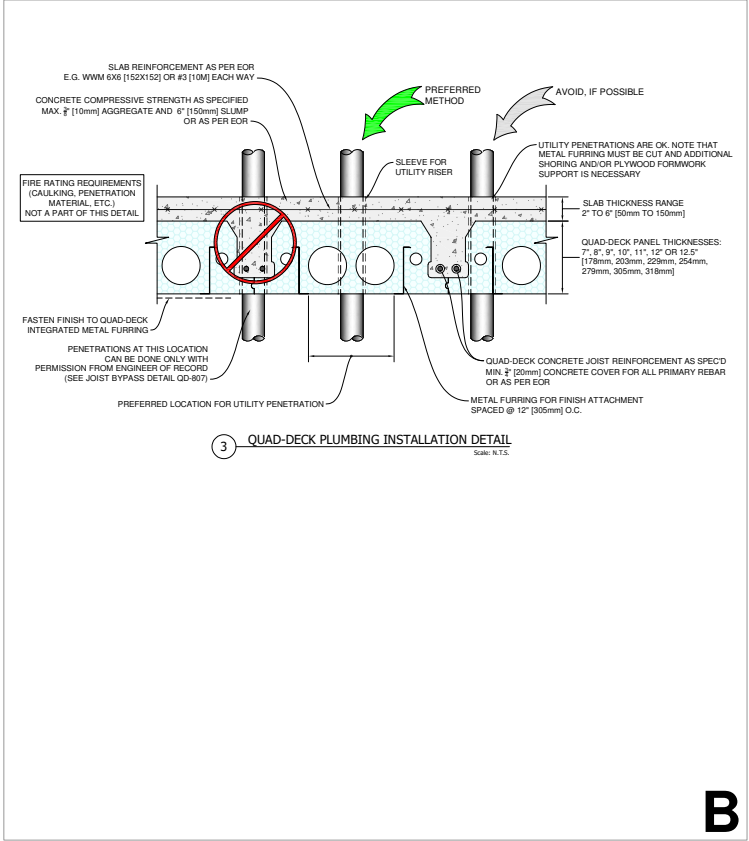

B

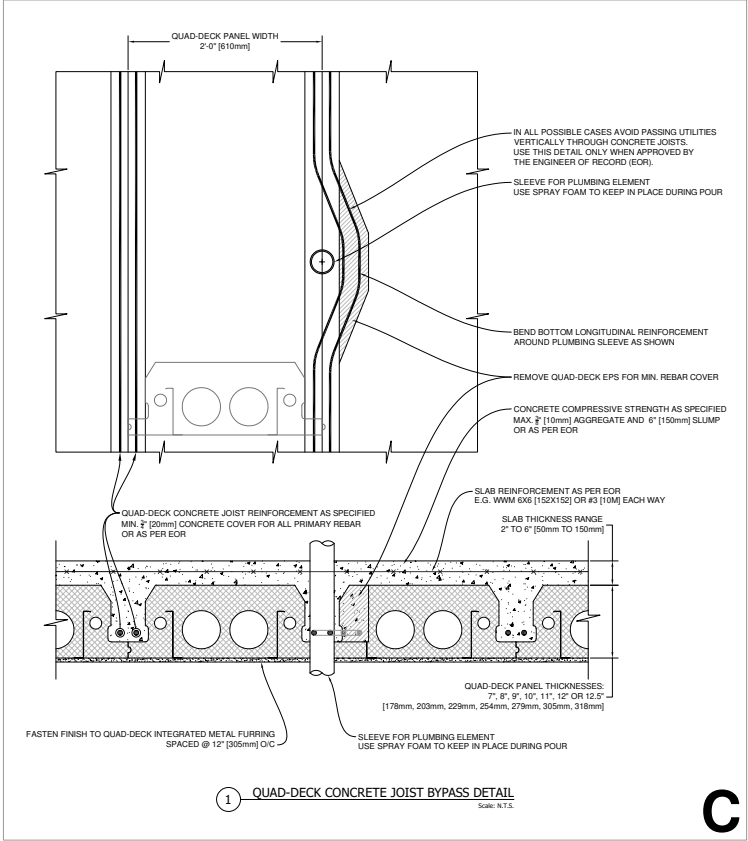

C

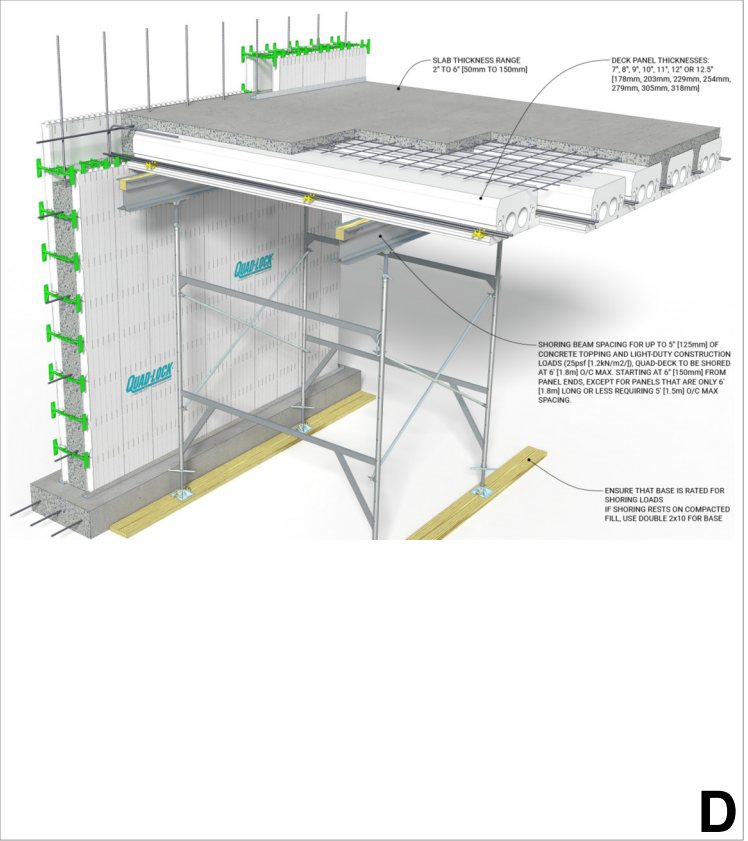

D



E



F



G



H

QUAD-LOCK
Building Systems

Quad-Lock Building Systems
19402 - 56th Avenue Surrey, BC V3S 6K4
Canada
888.711.5625 - Toll Free
604.590.3111 | 604.534.1212 - fax
www.quadlock.com

- THIS DESIGN AND DRAWINGS IS AND AT ALL TIMES REMAINS THE EXCLUSIVE PROPERTY OF QUAD-LOCK BUILDING SYSTEMS AND CANNOT BE USED WITHOUT THE DESIGNER'S WRITTEN CONSENT.
- DO NOT SCALE DRAWINGS.
- WRITTEN DIMENSIONS ALWAYS TAKE PRECEDENCE OVER SCALED DIMENSIONS.
- ALL DIMENSIONS MUST BE VERIFIED BY THE CONTRACTOR.
- QUAD-LOCK BUILDING SYSTEMS DOES NOT ASSUME LIABILITY.
- PLEASE ADVISE QUAD-LOCK BUILDING SYSTEMS IF ANY DISCREPANCIES ARE FOUND OR EXPLANATIONS REQUIRED.
- ALL WORK MUST COMPLY WITH LOCAL BY-LAW AND CURRENT BUILDING CODE.
- ALL INSTALLATION DETAILS ARE CONTROLLED BY ICF INSTALLER & G.C.

No.	DATE (yyyy-mm-dd)	DESCRIPTION
R E V I S I O N S		

EMPRESA AZZUL

CANTON SAN RAFAEL, CONDOMINIO RECREATIVO, LOMAS DE SAN BLAS, CALLE MAJAHUAL,
POLIGONO 6, NUMERO 19, LA LIBERTAD COSTA. DEPARTAMENTO DE LA LIBERTAD

QUAD-DECK FLOOR/ROOF DETAILS

DATE:	2025-09-16	DRAWN BY:	Z. PROSTRAN
SCALE:	AS SHOWN	APPROVED BY:	
SHEET SIZE:	11"x17"	APPROVED ON:	YYYY-MM-DD
PROJECT No:	K018750	SHEET:	Q-6
DRAWING No:			