
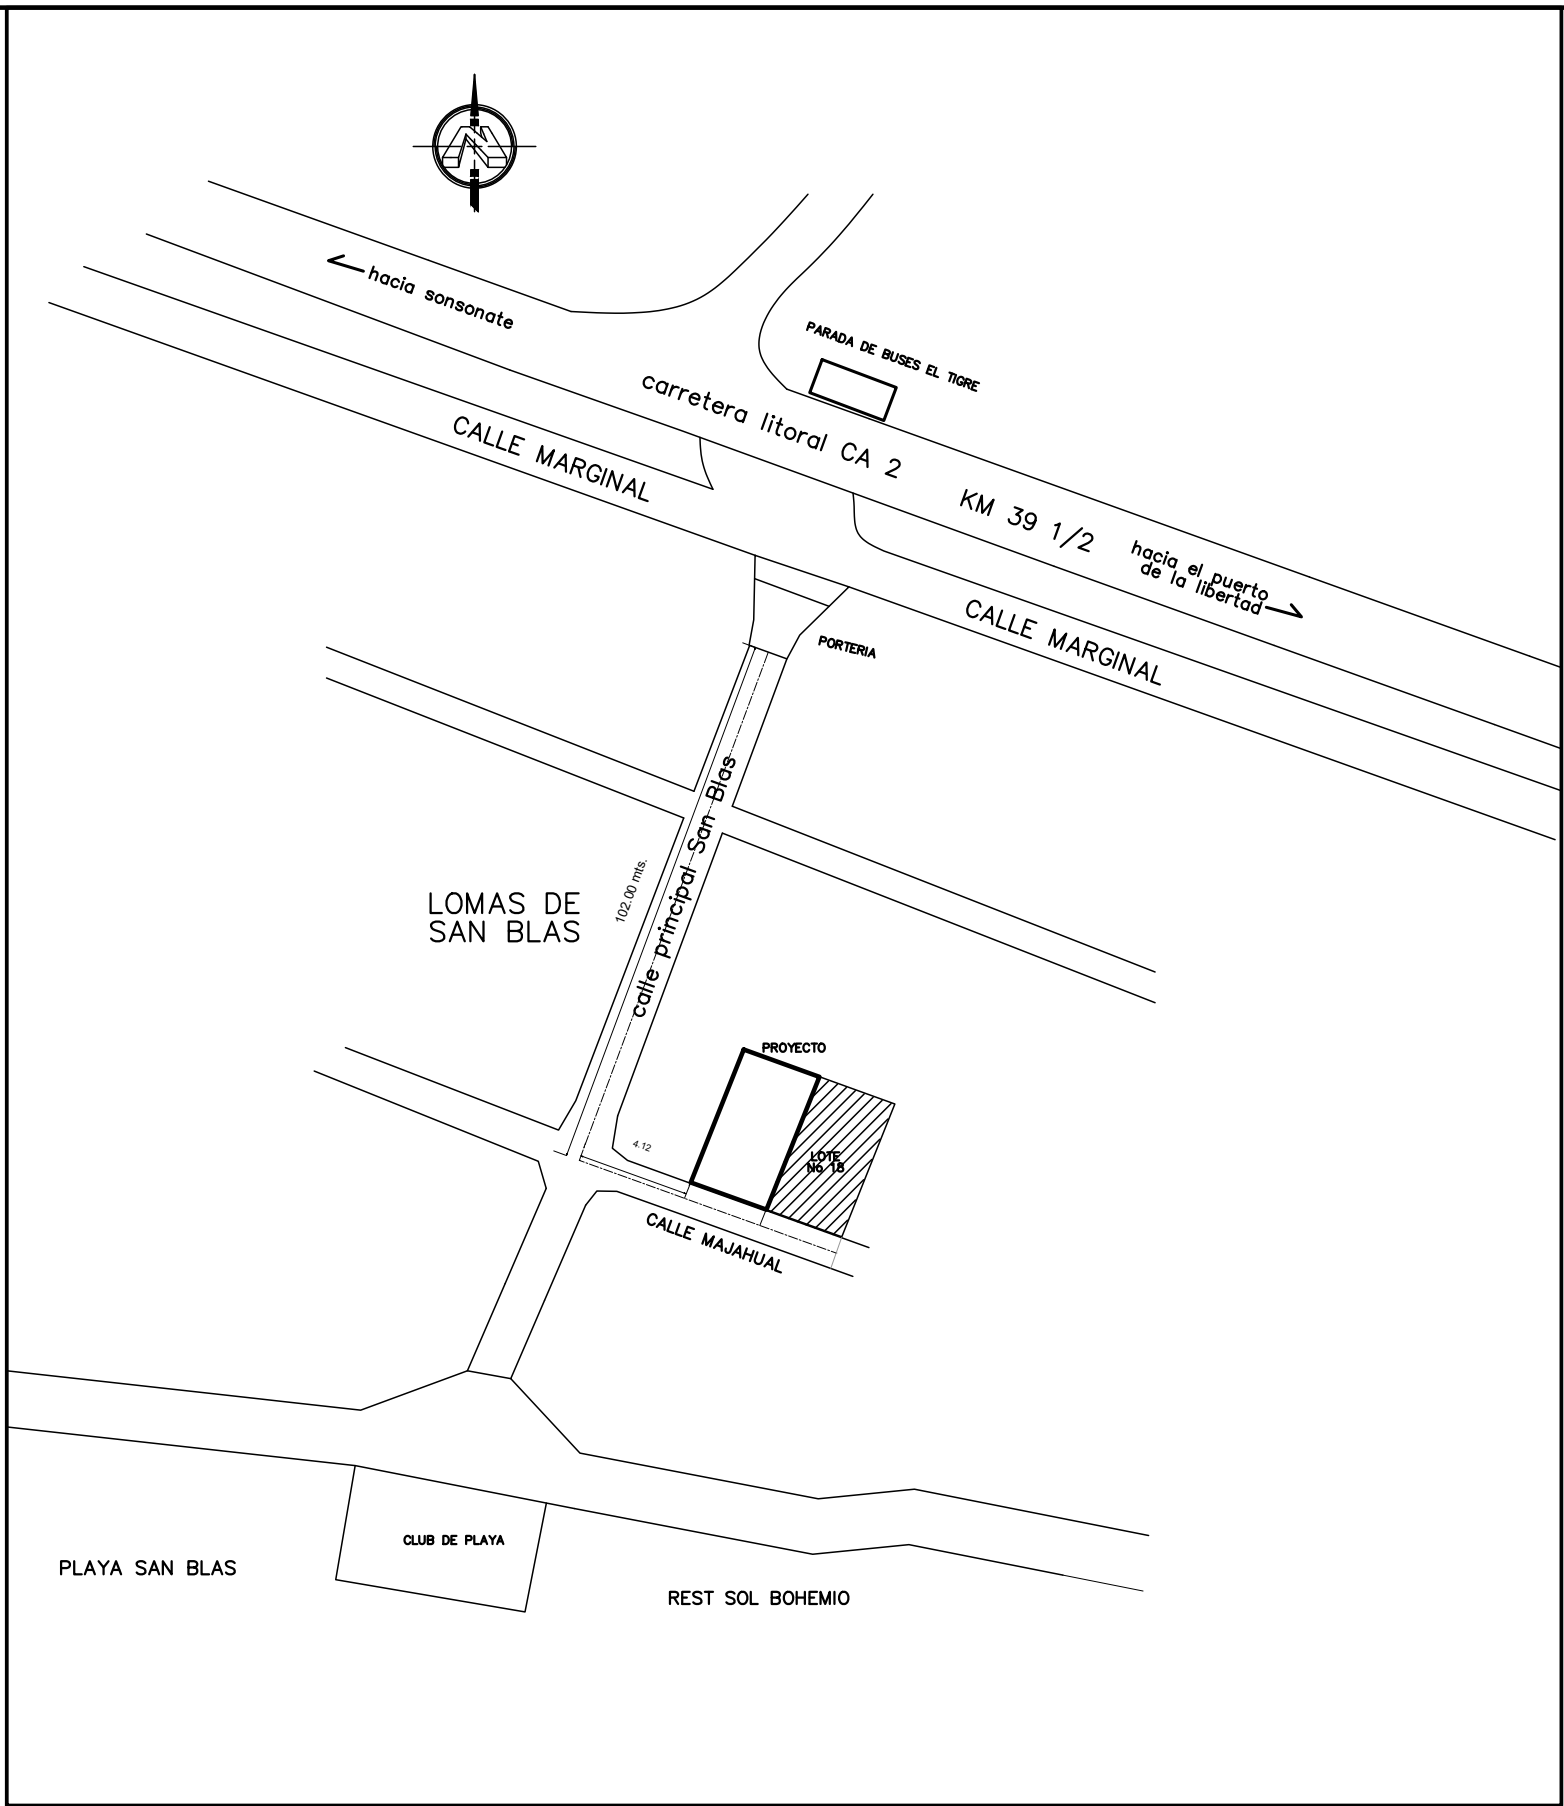


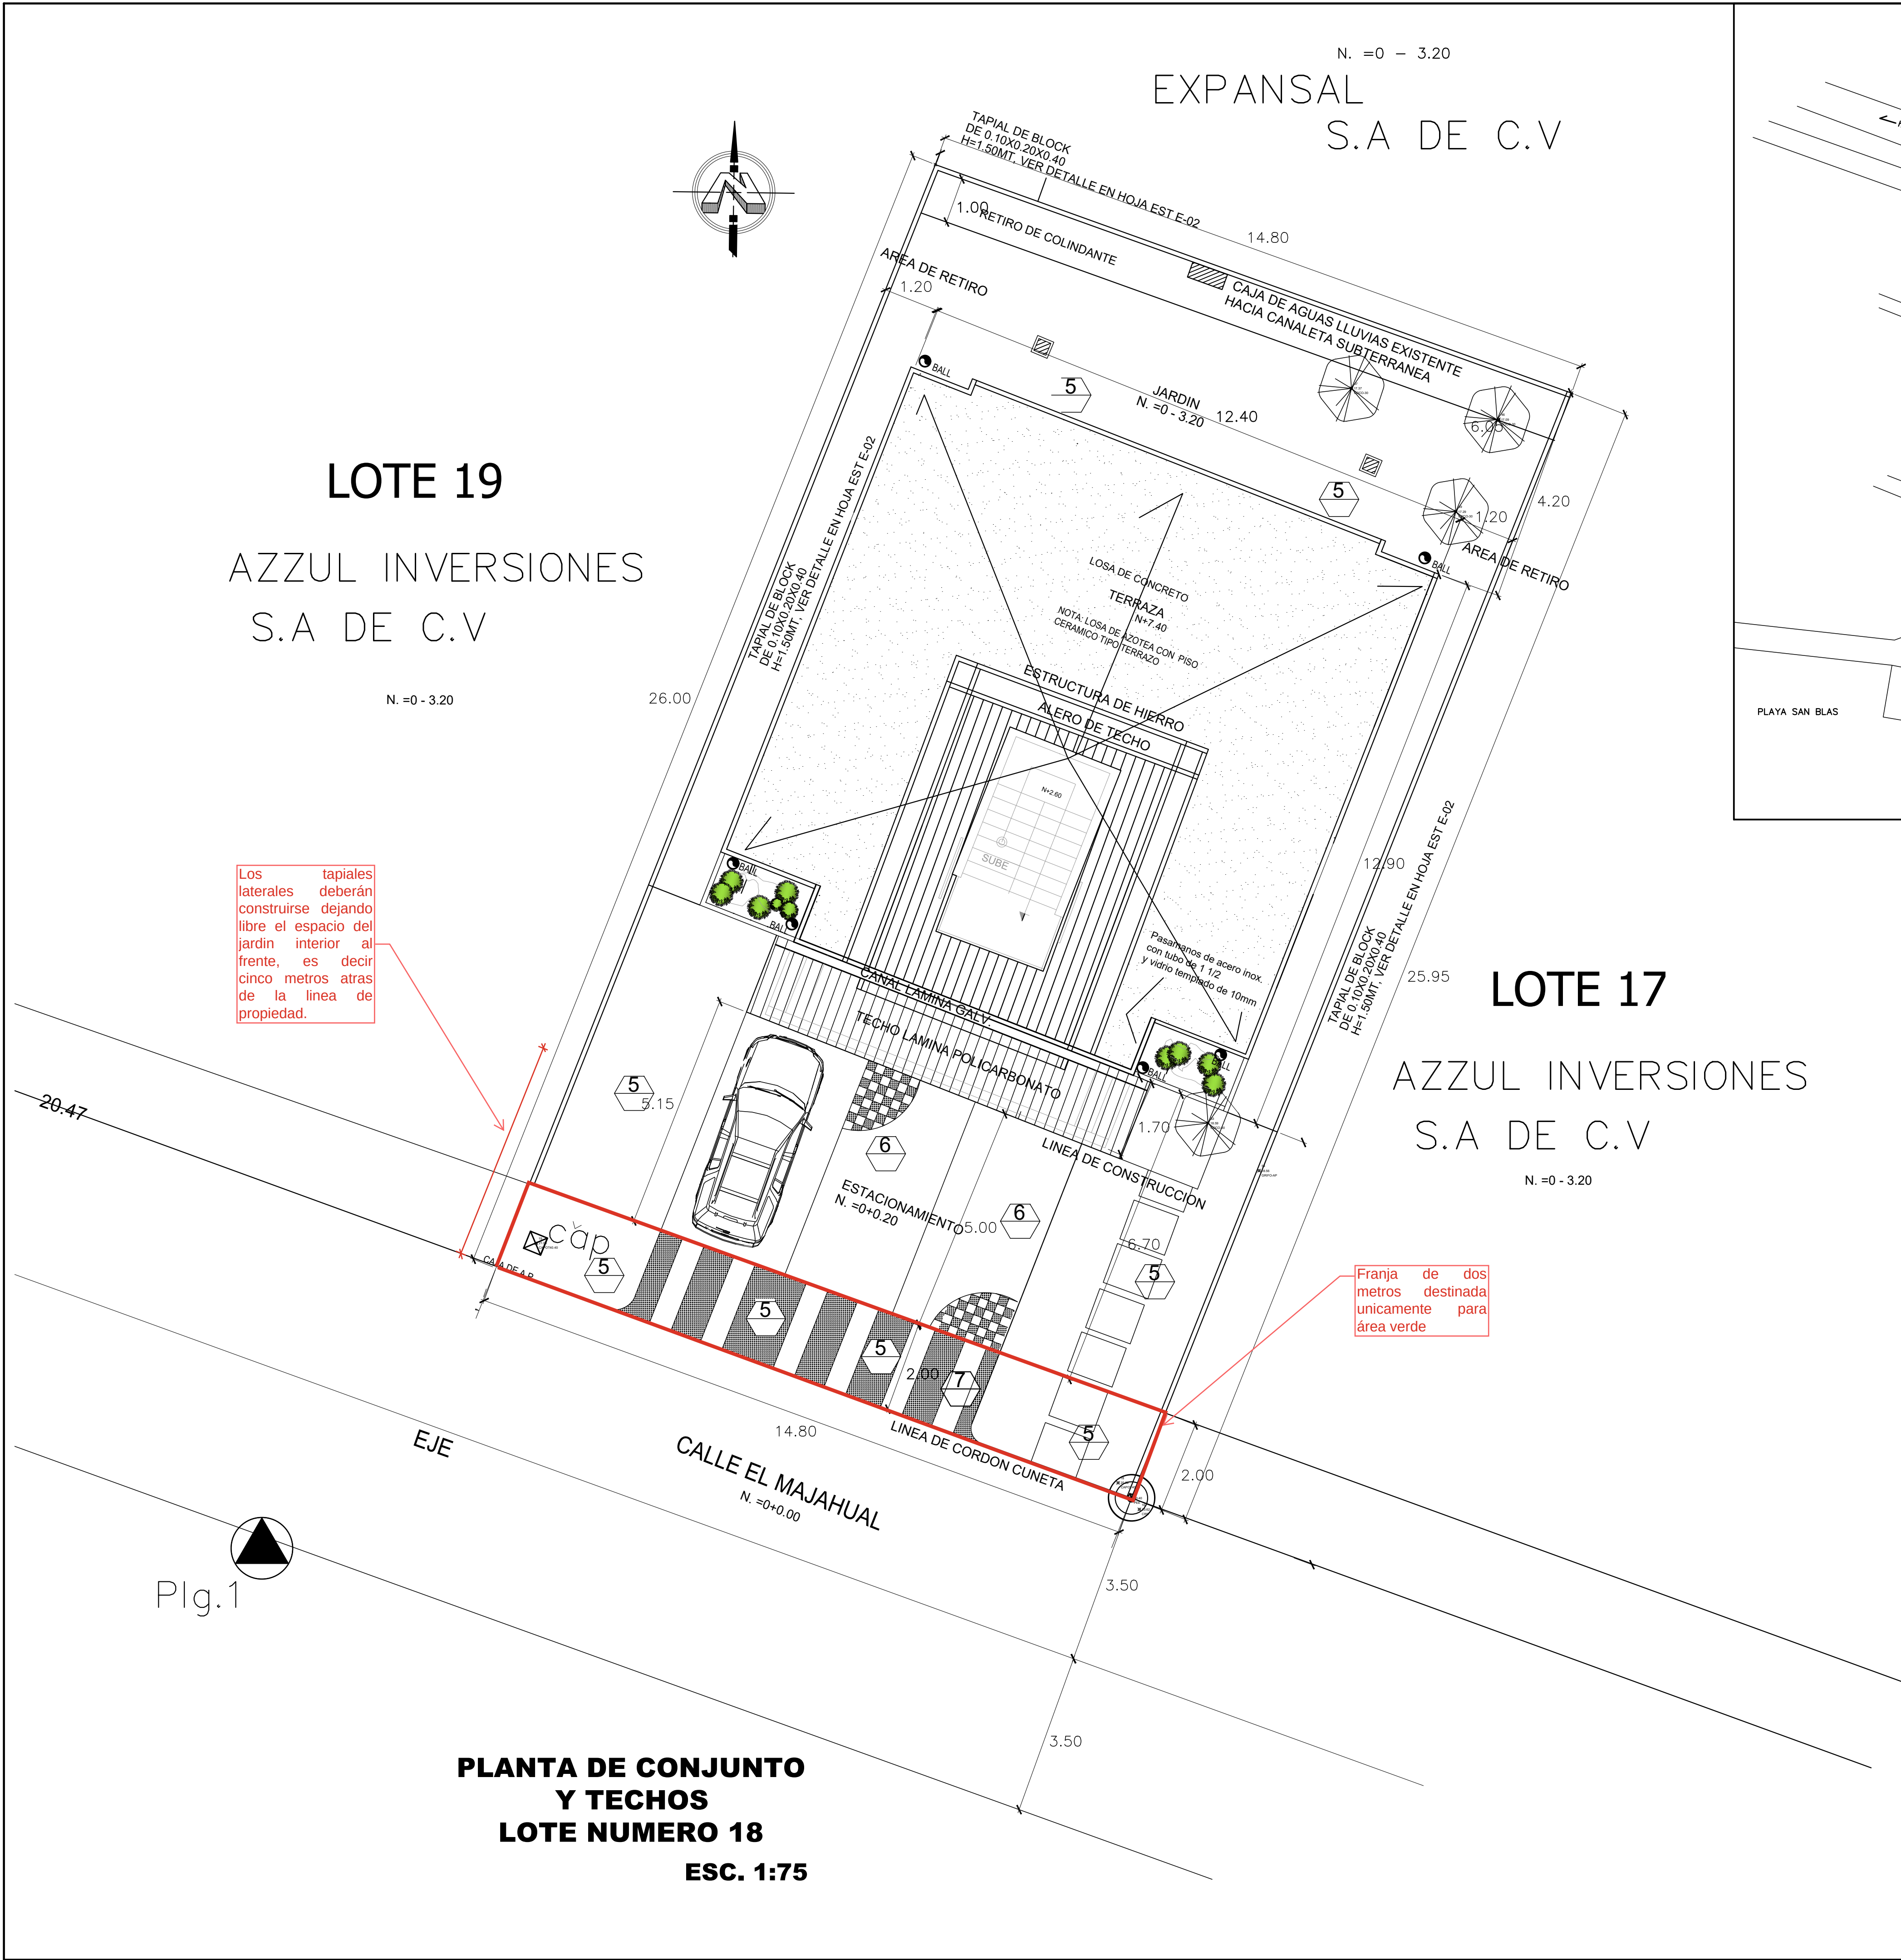

SELLOS DE APROBACION:

ESTE PLANO FORMA PARTE INTEGRAL DE LA RESOLUCION EMITIDA EN FECHA 24 DE JULIO DE 2025 EN FORMATO DIGITAL Y CORRESPONDE AL EXPEDIENTE DE PERMISO DE CONSTRUCCION REFERENCIA 0333-2025, PRESENTADO BAJO LA RESPONSABILIDAD DE LA ARQ. MORENA GUADALUPE VASQUEZ LOPEZ CON REGISTRO PROFESIONAL VMVDU A-4576.

PRESENTA:

ARQ. KARLA RODRIGUEZ DE CHOCOBAR

PROYECTO:

CONSTRUCCION DE VIVIENDA DE DOS NIVELES Y TERRAZA EMPRESA AZZUL

PROPIETARIOS:

EMPRESA AZZUL S.A DE C.V

UBICACION:

CANTON SAN RAFAEL, CONDOMINIO RECREATIVO, LOMAS DE SAN BLAS, CALLE MAJAHUAL, POLIGONO 6, NUMERO 18, LA LIBERTAD COSTA, DEPARTAMENTO DE LA LIBERTAD

CONTENIDO:

CONJUNTO Y TECHOS

ESCALA:

INDICADA

FECHA:


MARZO 2025

HOJA N°:


CT -01

FIRMA Y SELLO DE PROFESIONALES RESPONSABLES


DISEÑO ARQUITECTÓNICO: FIRMA: DISEÑO ARQUITECTÓNICO: SELLO:	DIRECTOR DE LA OBRA: FIRMA: DIRECTOR DE LA OBRA: SELLO:	RESPONSABLE DEL TRAMITE: FIRMA: RESPONSABLE DEL TRAMITE: SELLO:
REGISTRO NACIONAL DE ARQUITECTOS E INGENIEROS CARLA PATRICIA RODRIGUEZ DE CHOCOBAR A-2359 ARQUITECTA	REGISTRO NACIONAL DE ARQUITECTOS E INGENIEROS CARLOS FRANCISCO CALACUA MAISA A-3297 ARQUITECTO	REGISTRO NACIONAL DE ARQUITECTOS E INGENIEROS Morena Guadalupe Vázquez López A - 4576 ARQUITECTA

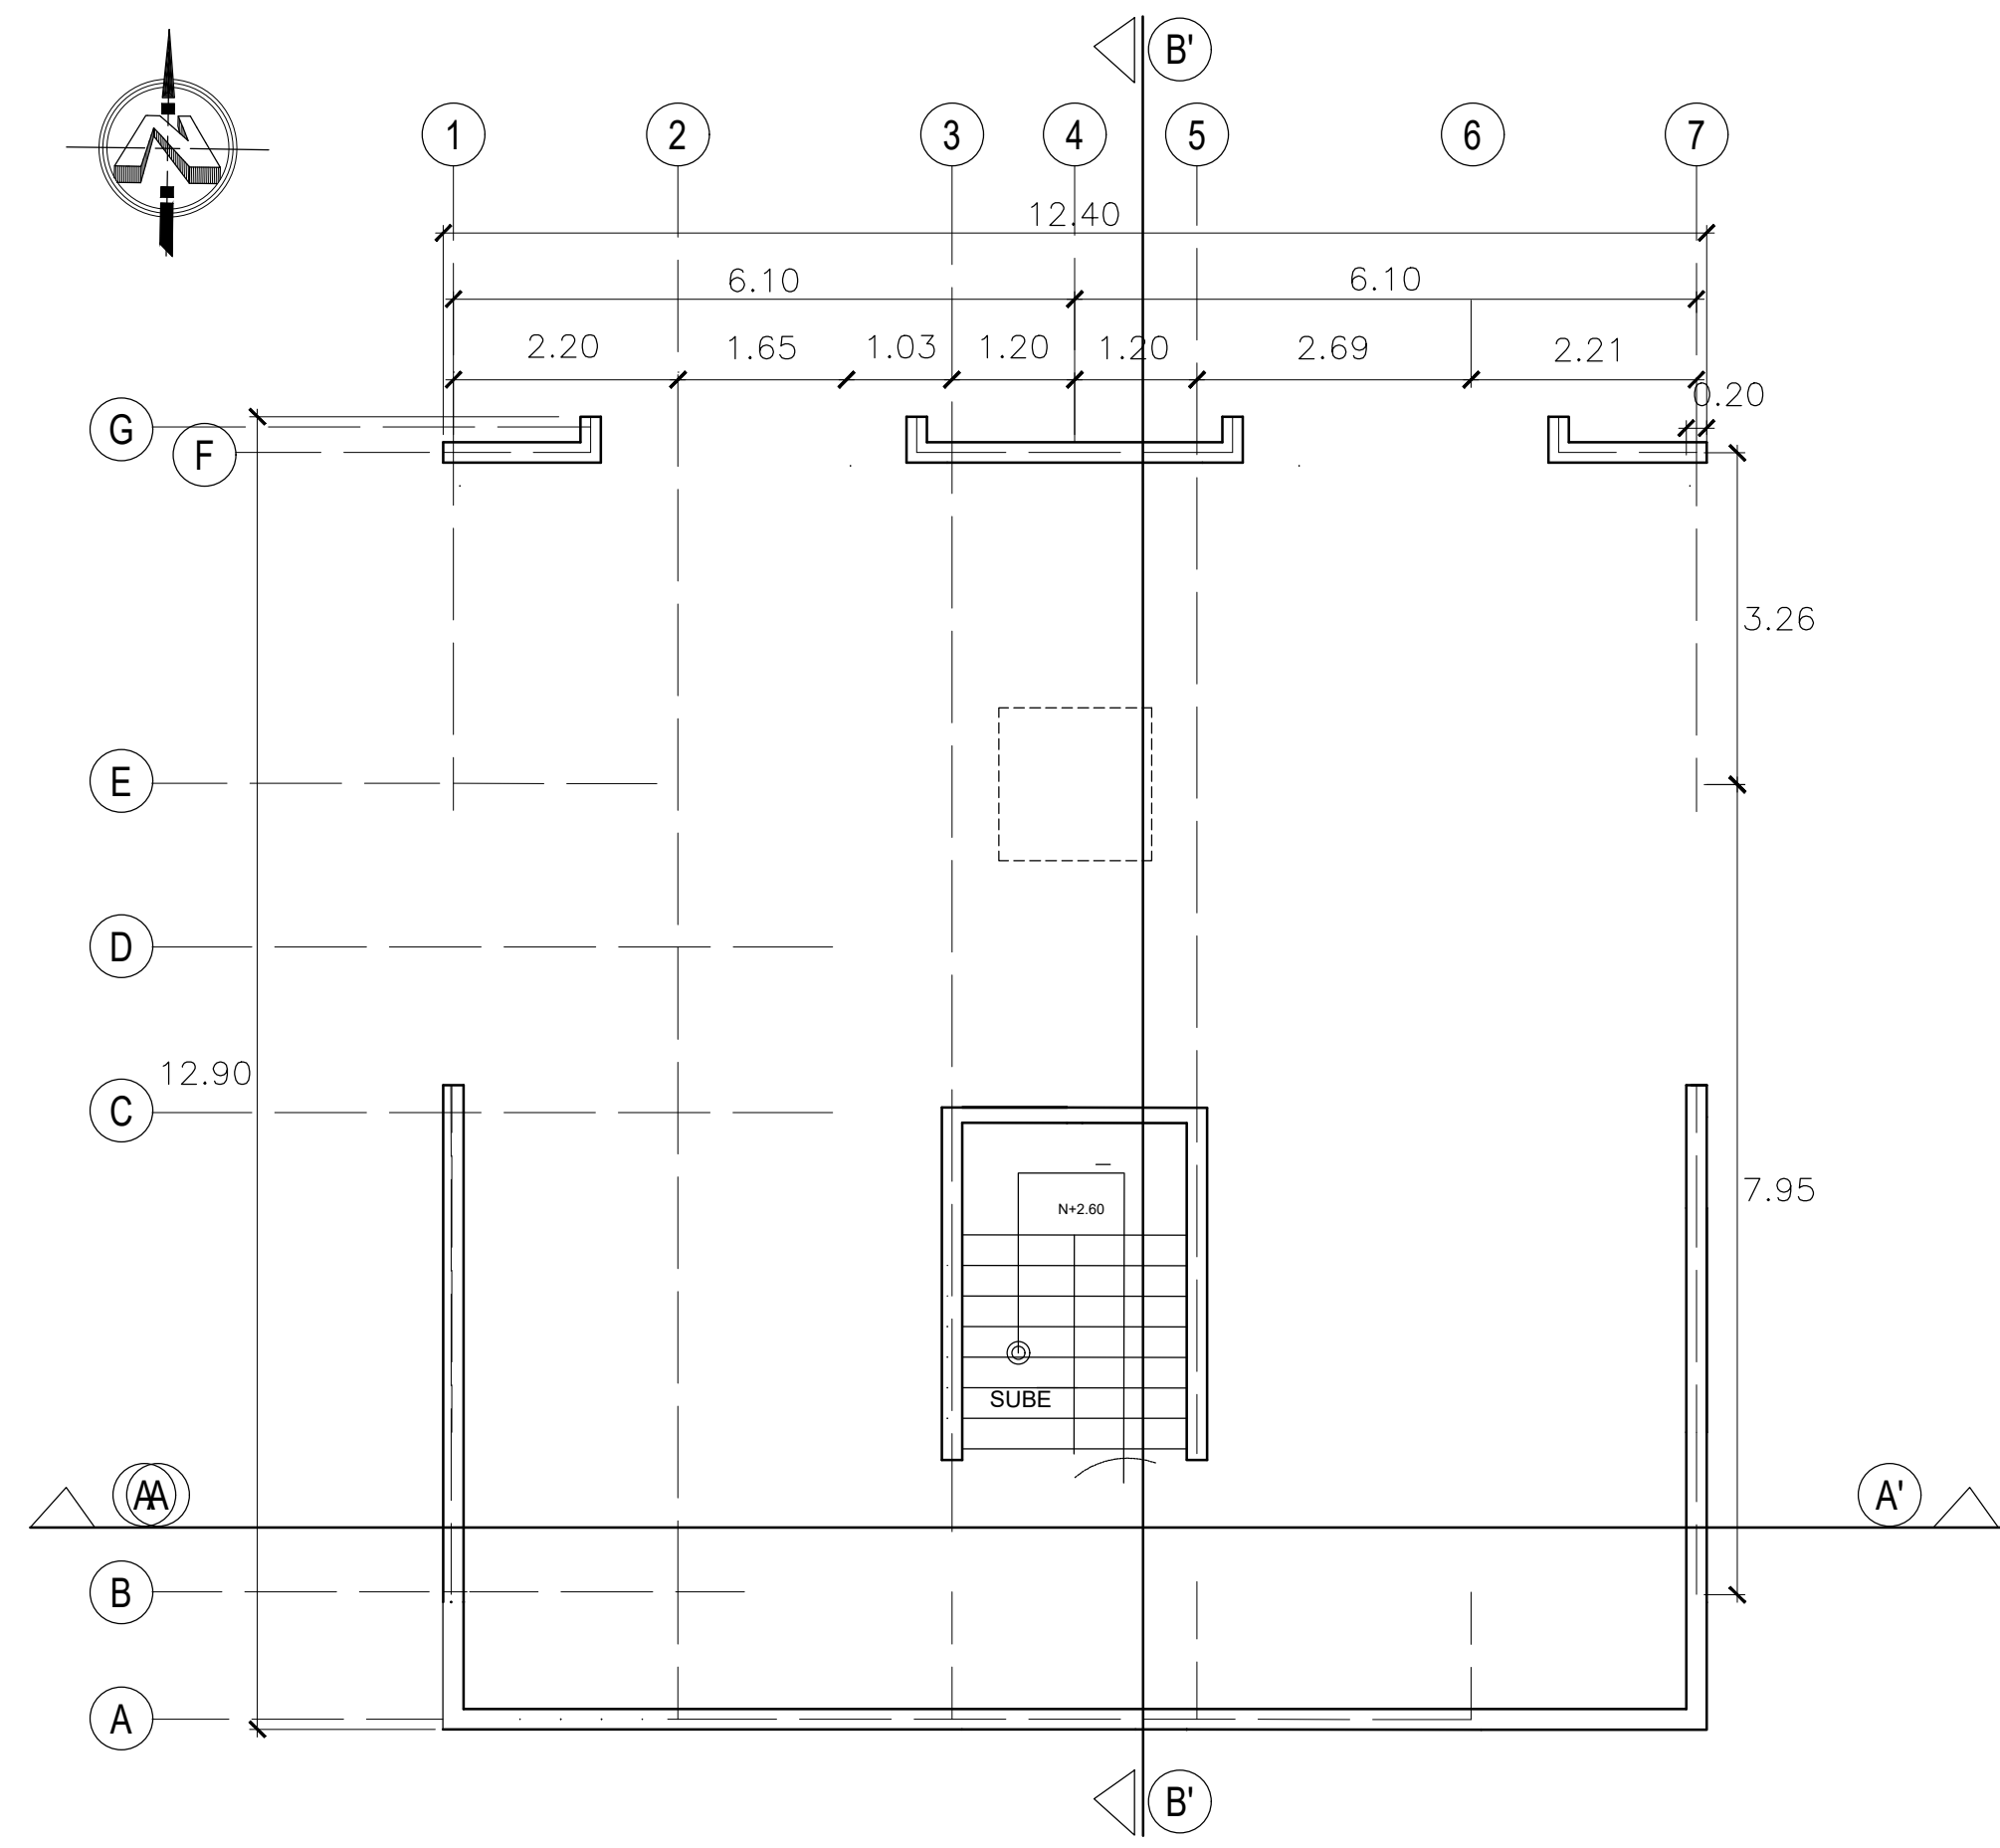


PLANTA ARQUITECTONICA
NIVEL FUNDACION
ESC. 1:75

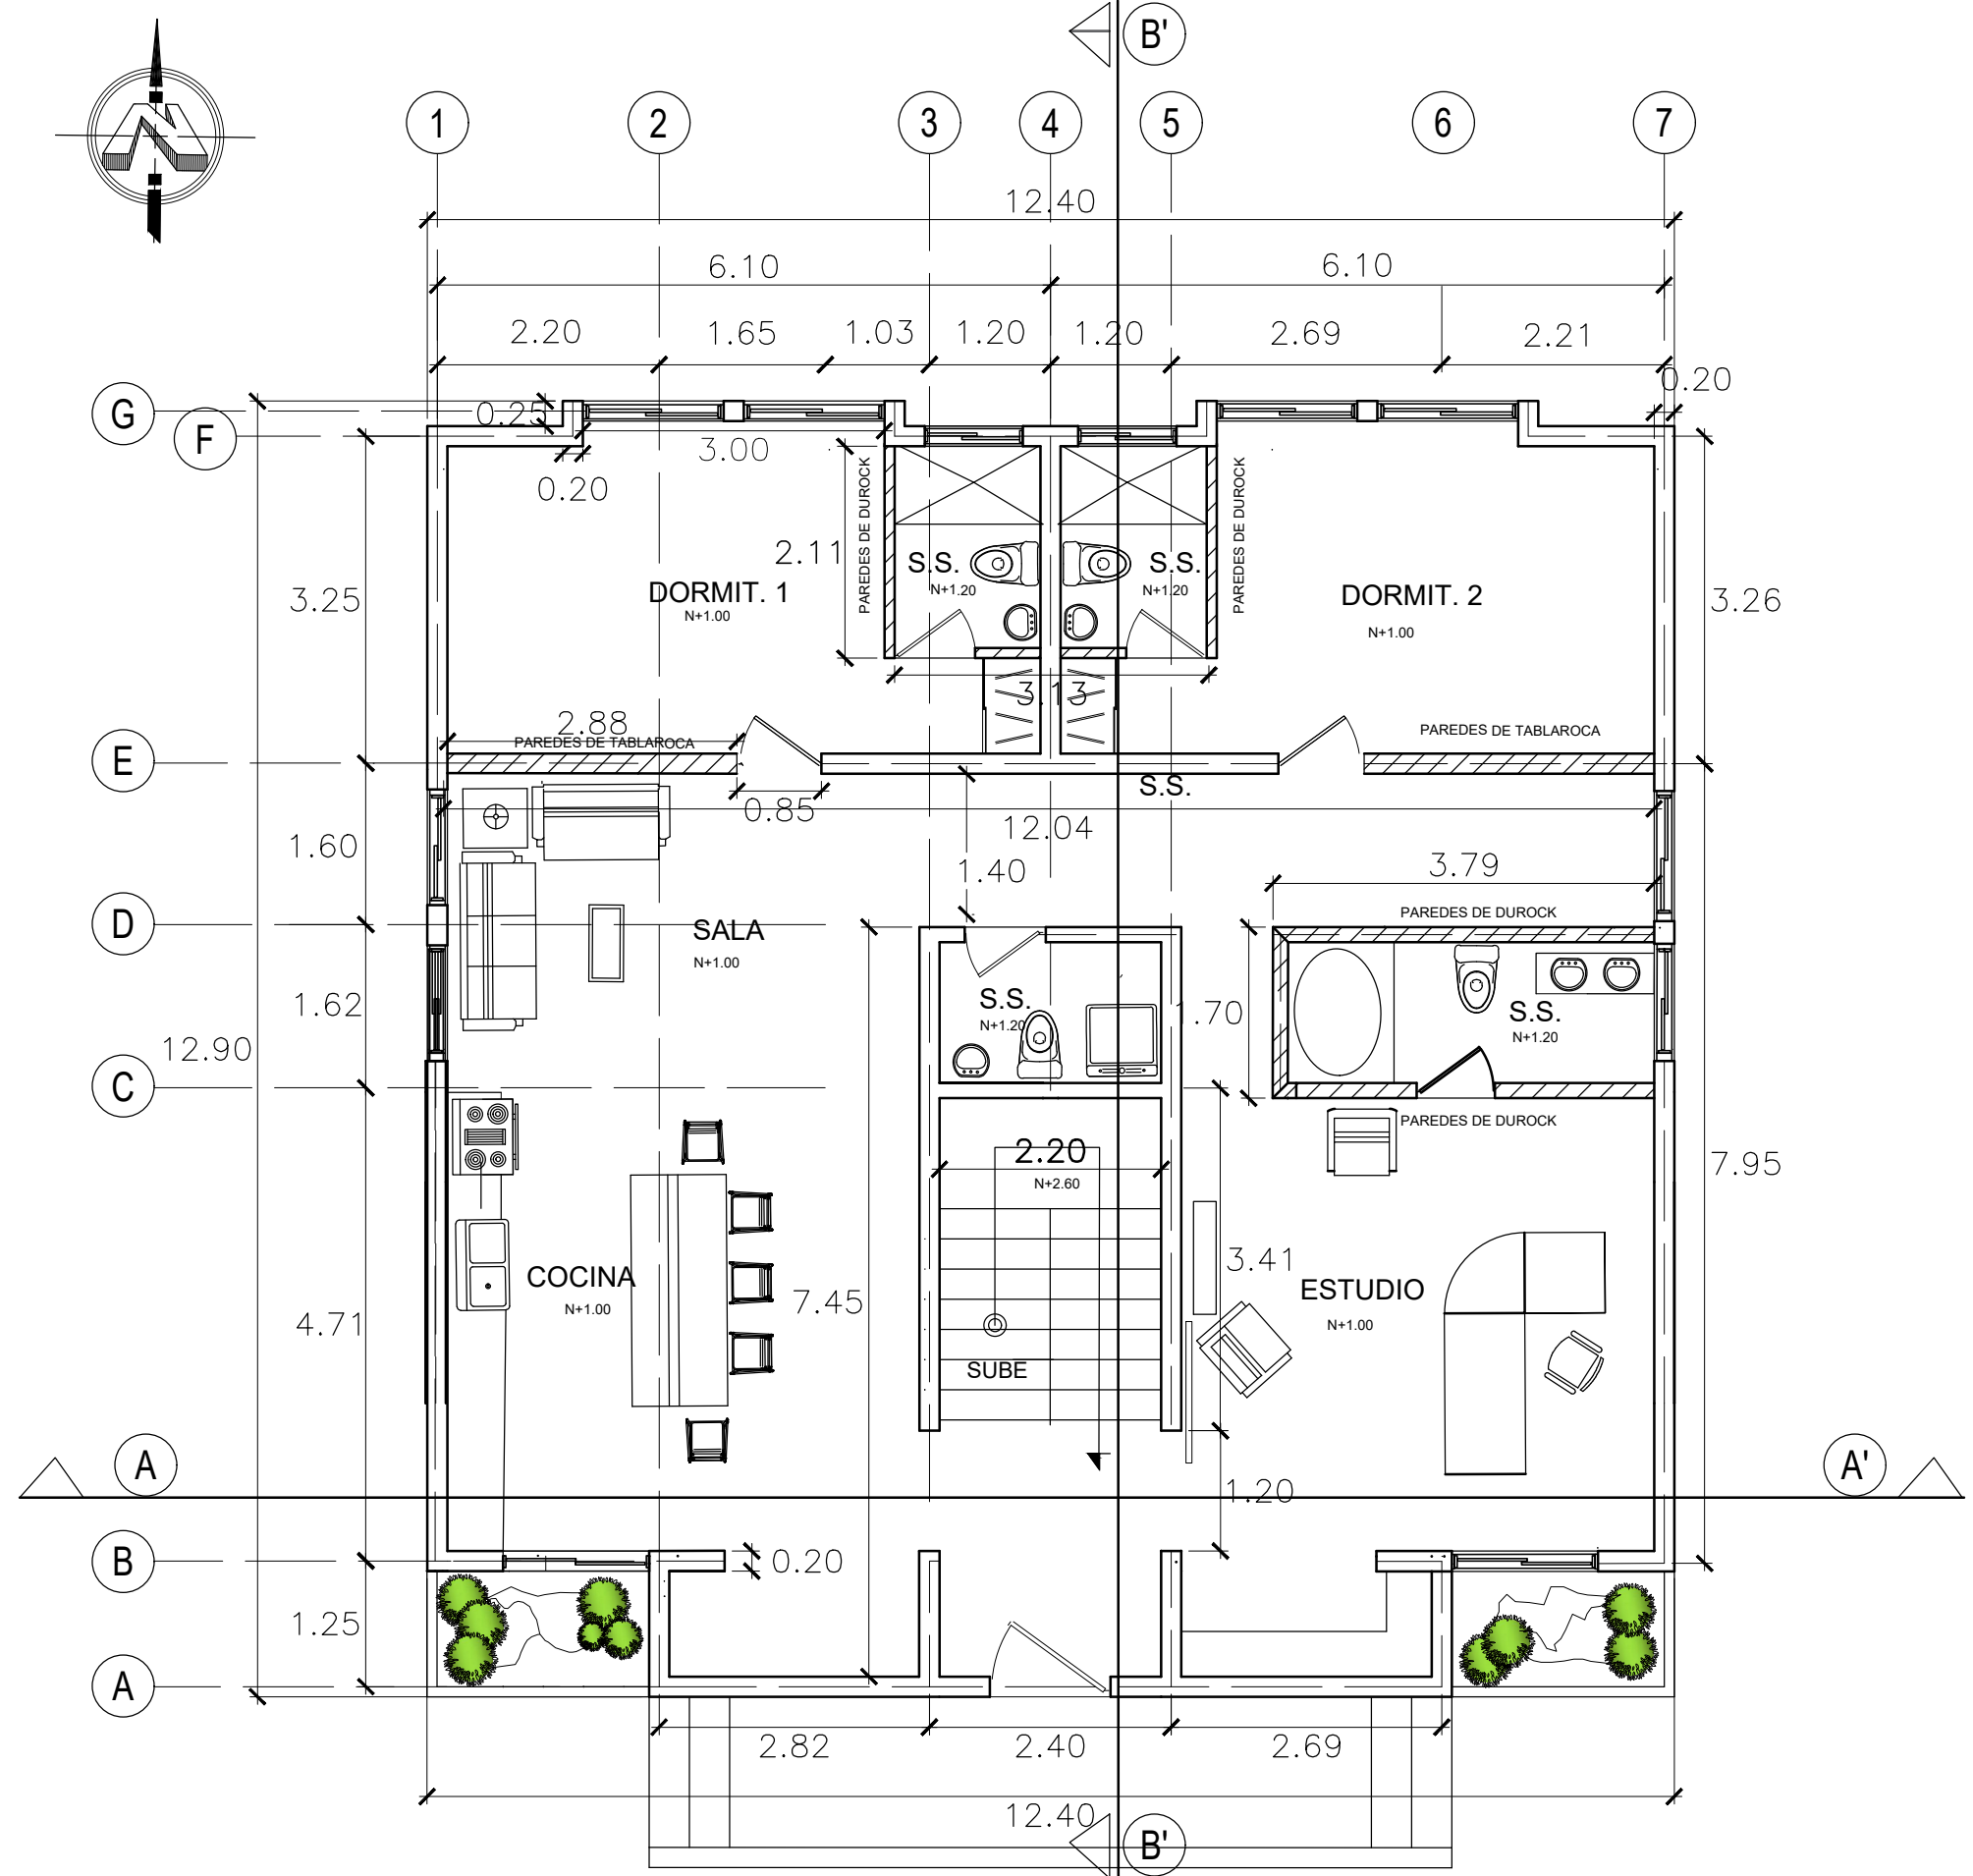

PLANTA ARQUITECTONICA
PRIMER NIVEL ESC. 1:75

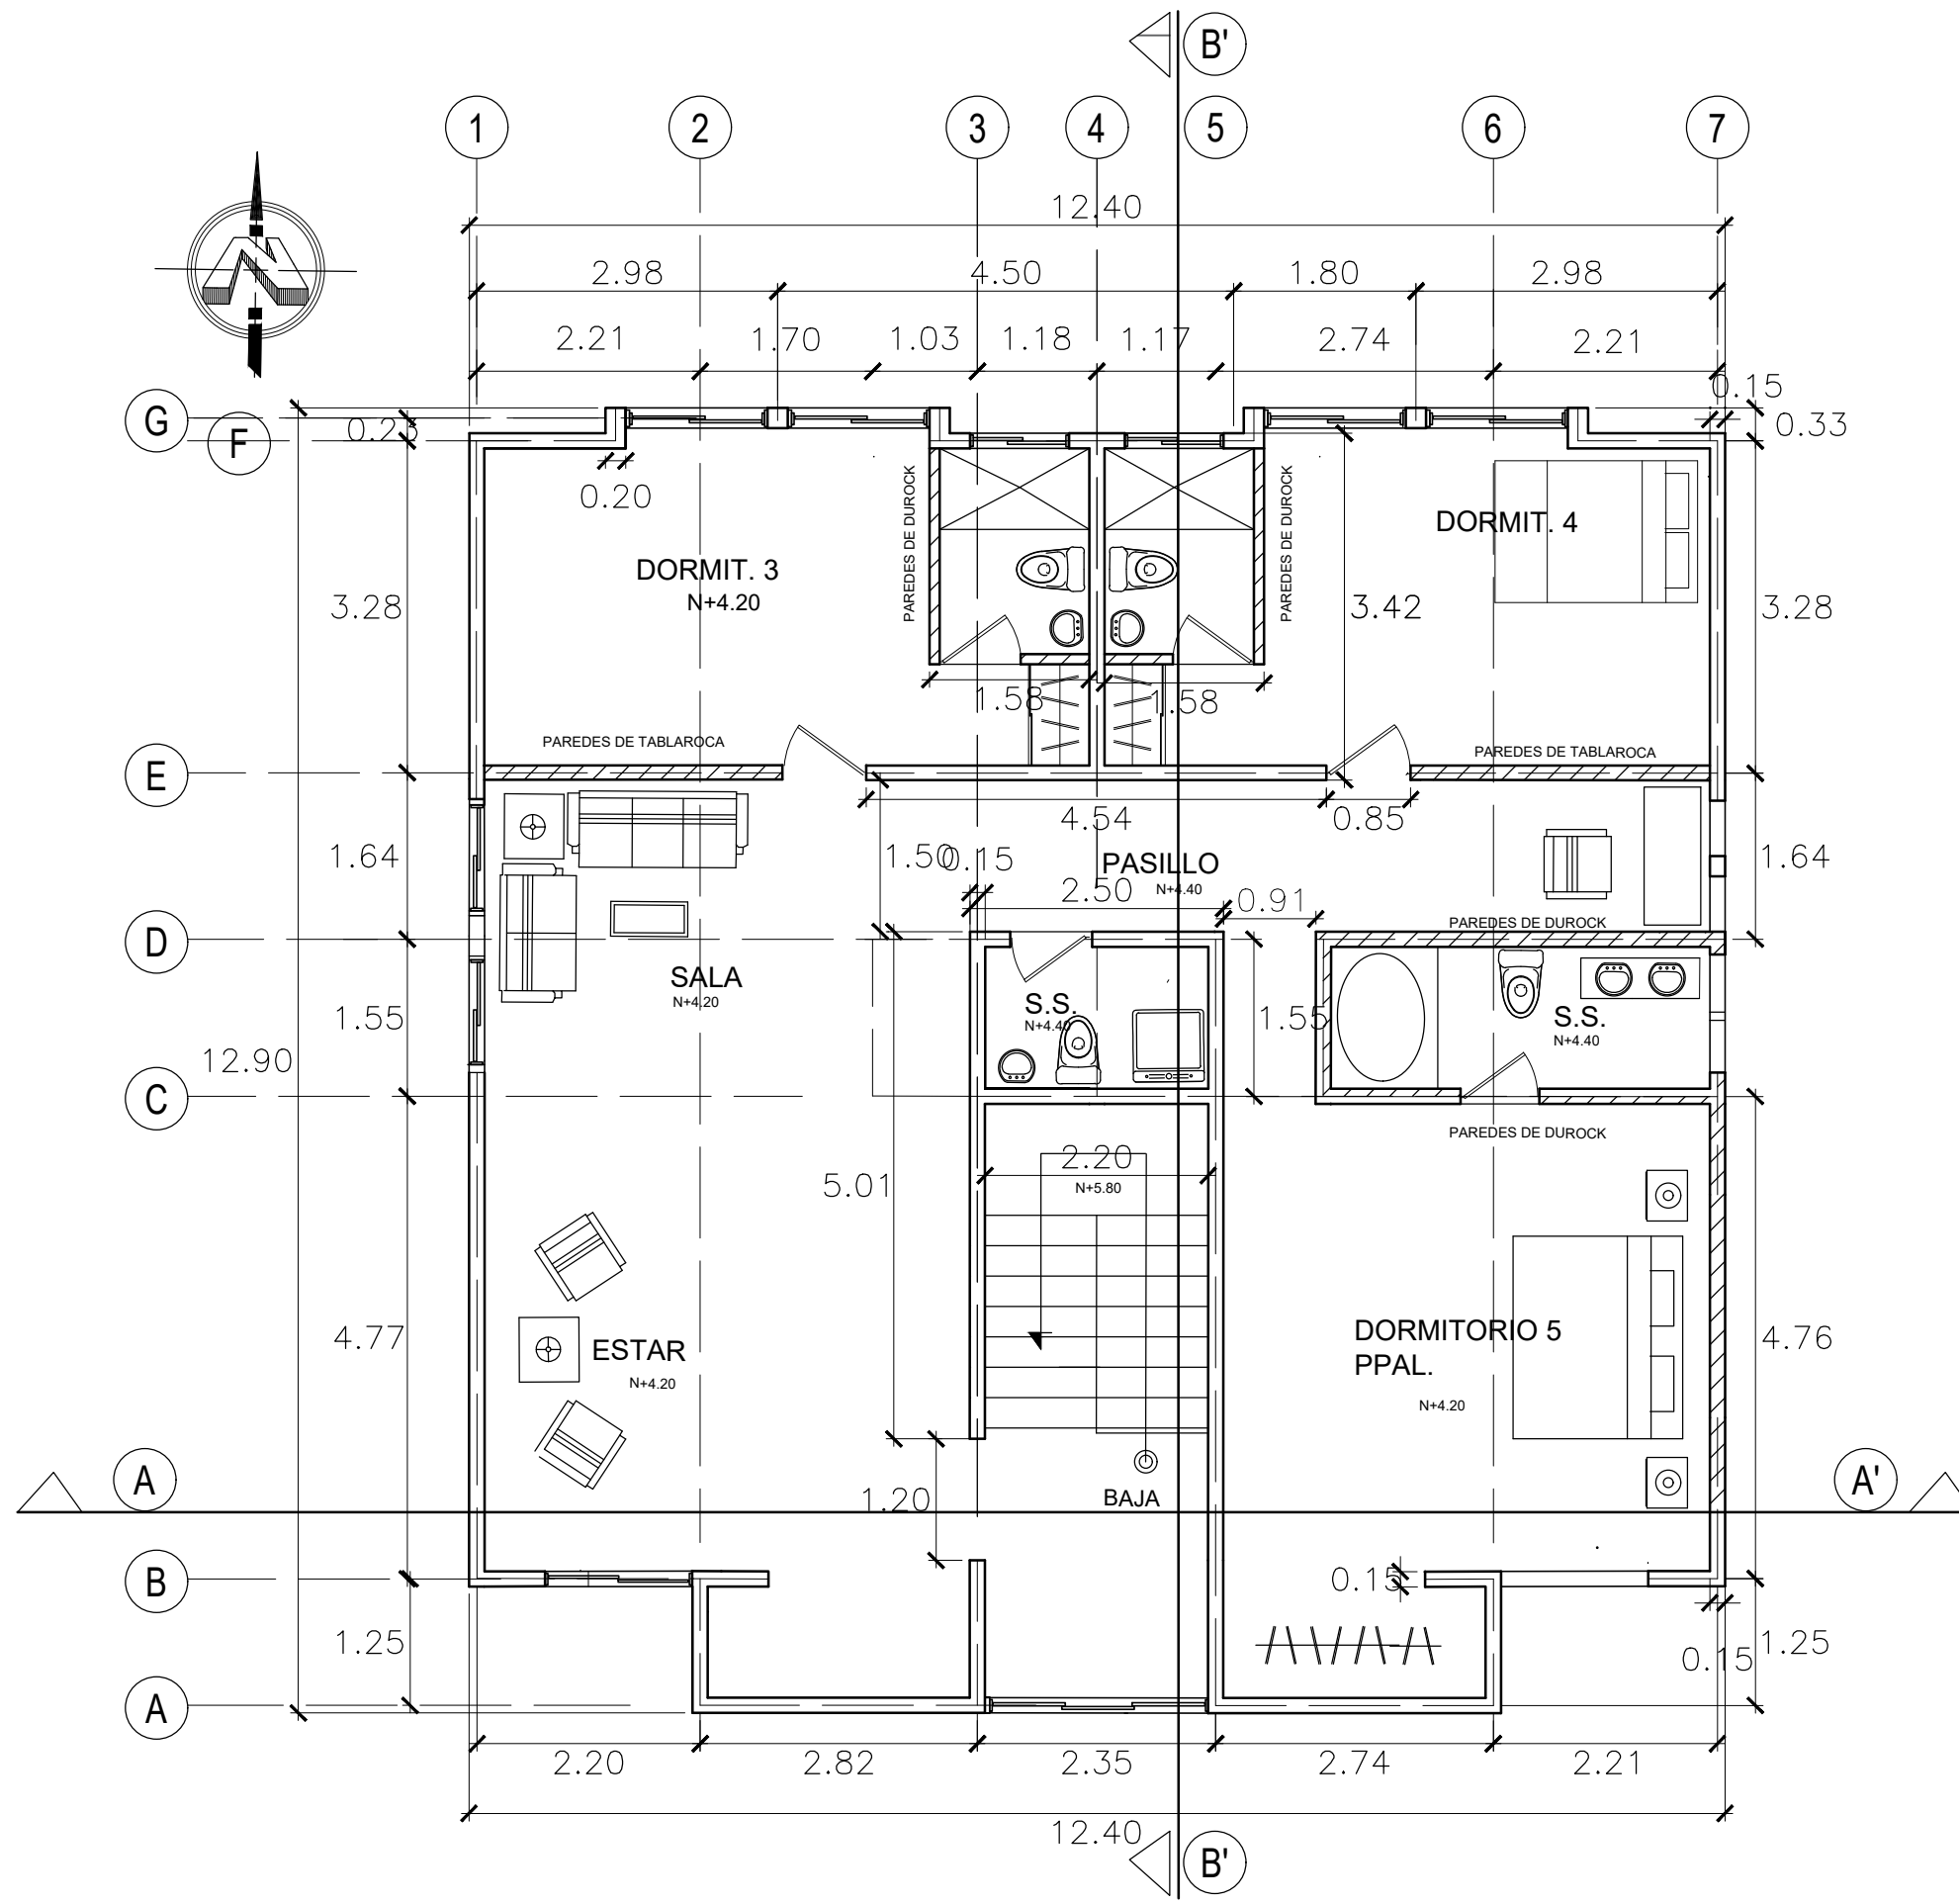

PLANTA ARQUITECTONICA
SEGUNDO NIVEL ESC. 1:75

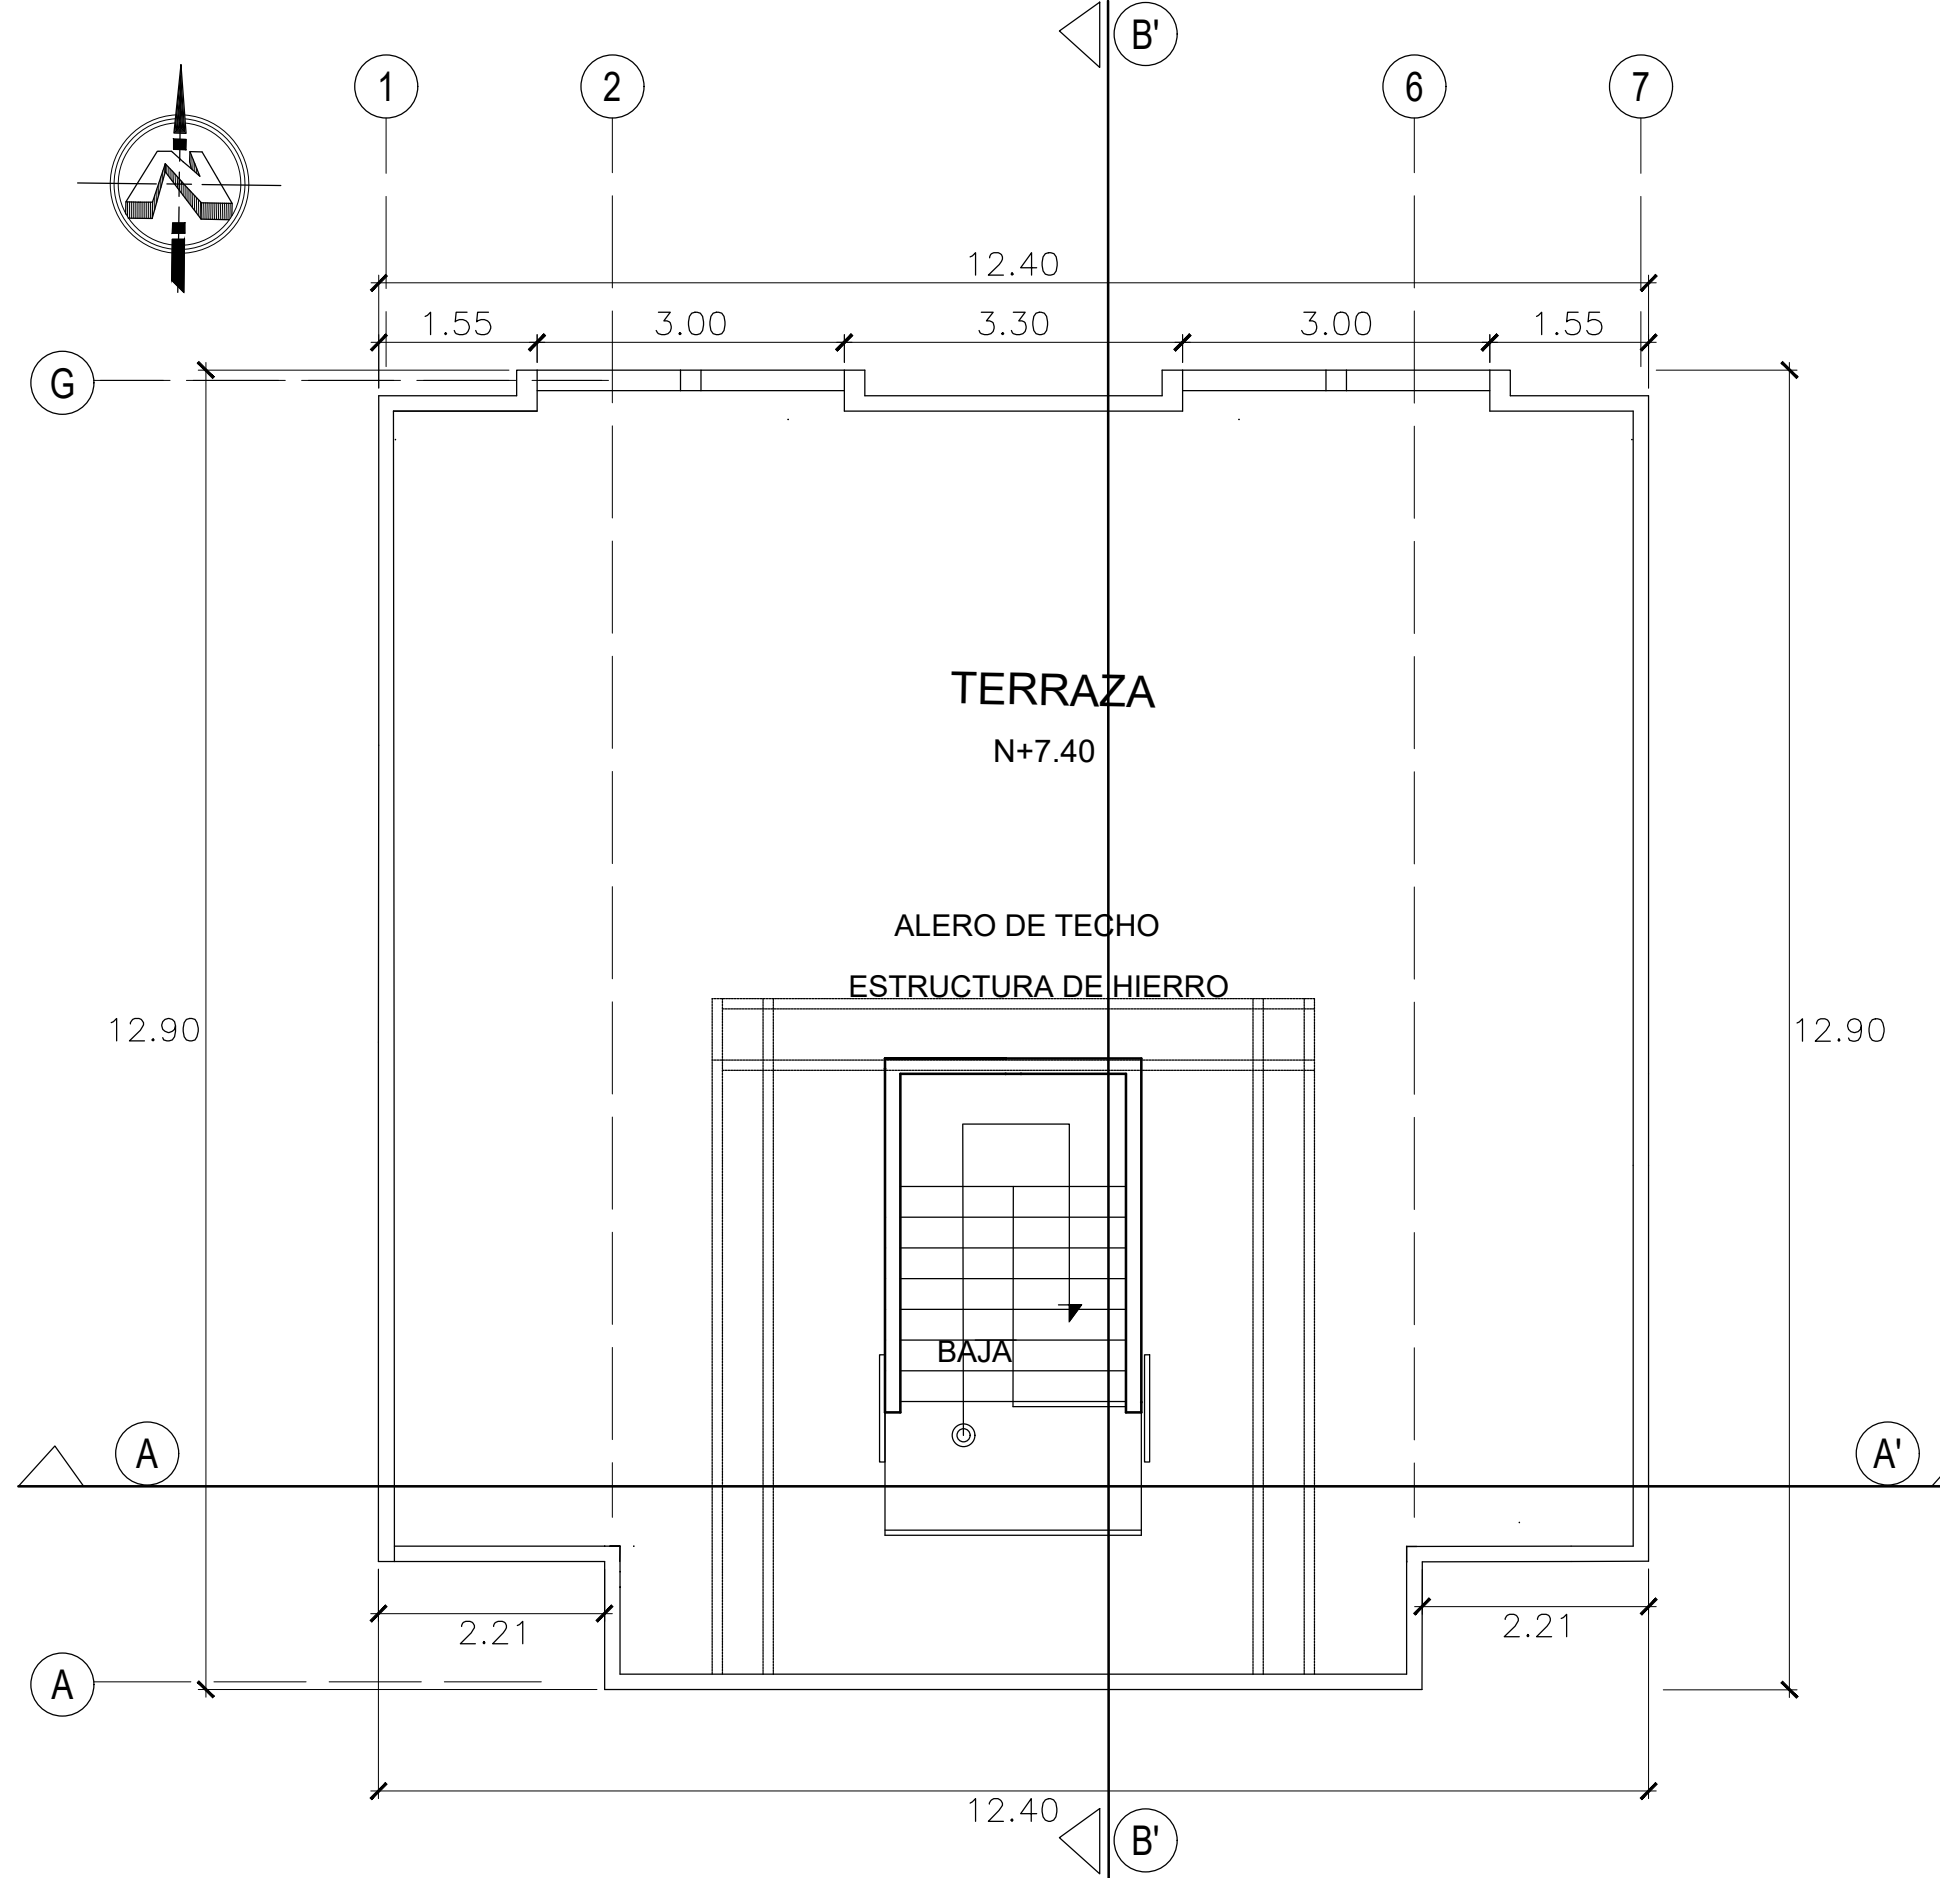

PLANTA ARQUITECTONICA
TERRAZA ESC. 1:75

CUADRO DE AREAS LOTE 18	
	VALOR USO HABITACIONAL (M2)
AREA DE CONSTRUCCION(M2 EXCEPTO SOTANO)	458.61 M2
AREA DE CIRCULACIONES VERTICALES(M2)	26.22 M2
AREA DE CIRCULACIONES HORIZONTALES(M2)	
AREA PARA CIRCULACION (M2)	
AREA DEL SOTANO (M2)	
AREA PARA ESTACIONAMIENTO (M2)	43.37M2
AREA TOTAL CONSTRUCCION (M2)	458.61 M2
AREA DE OBRA DE URBANIZACION (M2)	
AREA DEMUROS Y TAPIALES (M2)	62.57 M2
No DE HABITACIONES PROYECTADAS (U)	5
AREA TIPO (M2) DE HABITACIONES	15.16 M2

SELLOS DE APROBACION:

ESTE PLANO FORMA PARTE INTEGRAL DE LA RESOLUCION EMITIDA EN FECHA 24 DE JULIO DE 2025 EN FORMATO DIGITAL Y CORRESPONDE AL EXPEDIENTE DE PERMISO DE CONSTRUCCION REFERENCIA 0333-2025. PRESENTADO BAJO LA RESPONSABILIDAD DE LA ARQ. MORENA GUADALUPE VÁSQUEZ LÓPEZ CON REGISTRO PROFESIONAL VMVDU A-4576.

ESTE PLANO SE EMITE CON FORMATO DE FIRMA ELECTRÓNICA CERTIFICADA, DE CONFORMIDAD A LO ESTABLECIDO EN LA LEY DE FIRMA ELECTRÓNICA, LFE Y ART. 19 DE LA LEY DE PROCEDIMIENTOS ADMINISTRATIVOS LPA, SI REQUIERE UNA CERTIFICACIÓN DE ESTE DOCUMENTO ELECTRÓNICO, ART. 16 LFE, SOLICITARLO AL CORREO: tramites@opamss.org.sv, Y CANCELAR LOS DERECHOS CORRESPONDIENTES.

PARA LA VALIDACIÓN DE LAS FIRMAS ELECTRÓNICAS UTILICE EL SIGUIENTE ENLACE:
<https://vol.uanataca.com/detail-validation/signatures%5b0%5d>

Coordinador del Departamento de Construcción y Desarrollo Urbano, con Delegación del Director Ejecutivo, de fecha 06 de enero de 2025.

Técnico de la Subdirección de Control del Desarrollo Urbano

PRESENTA:

ARQ. KARLA RODRIGUEZ DE CHOCOBAR

PROYECTO
CONSTRUCCION DE VIVIENDA DE DOS NIVELES Y TERRAZA EMPRESA AZZUL

PROPIETARIOS
EMPRESA AZZUL S.A DE C.V

UBICACION:
CANTON SAN RAFAEL, CONDOMINIO RECREATIVO, LOMAS DE SAN BLAS, CALLE MAJAHUAL, POLIGONO 6, NUMERO 18, LA LIBERTAD COSTA, DEPARTAMENTO DE LA LIBERTAD

CONTENIDO:

PLANTAS ARQUITECTONICAS
NIVEL FUNDACION, NIVEL 1, NIVEL 2 Y TERRAZA


ESCALA:
INDICADA

FECHA:
MARZO 2025


HOJA N°:
ARQ-01

FIRMA Y SELLO DE PROFESIONALES RESPONSABLES


DISEÑO ARQUITECTÓNICO: FIRMA: 	DIRECTOR DE LA OBRA: FIRMA: 	RESPONSABLE DEL TRAMITE: FIRMA:
DISEÑO ARQUITECTÓNICO: SELLO: 	DIRECTOR DE LA OBRA: SELLO: 	RESPONSABLE DEL TRAMITE: SELLO:

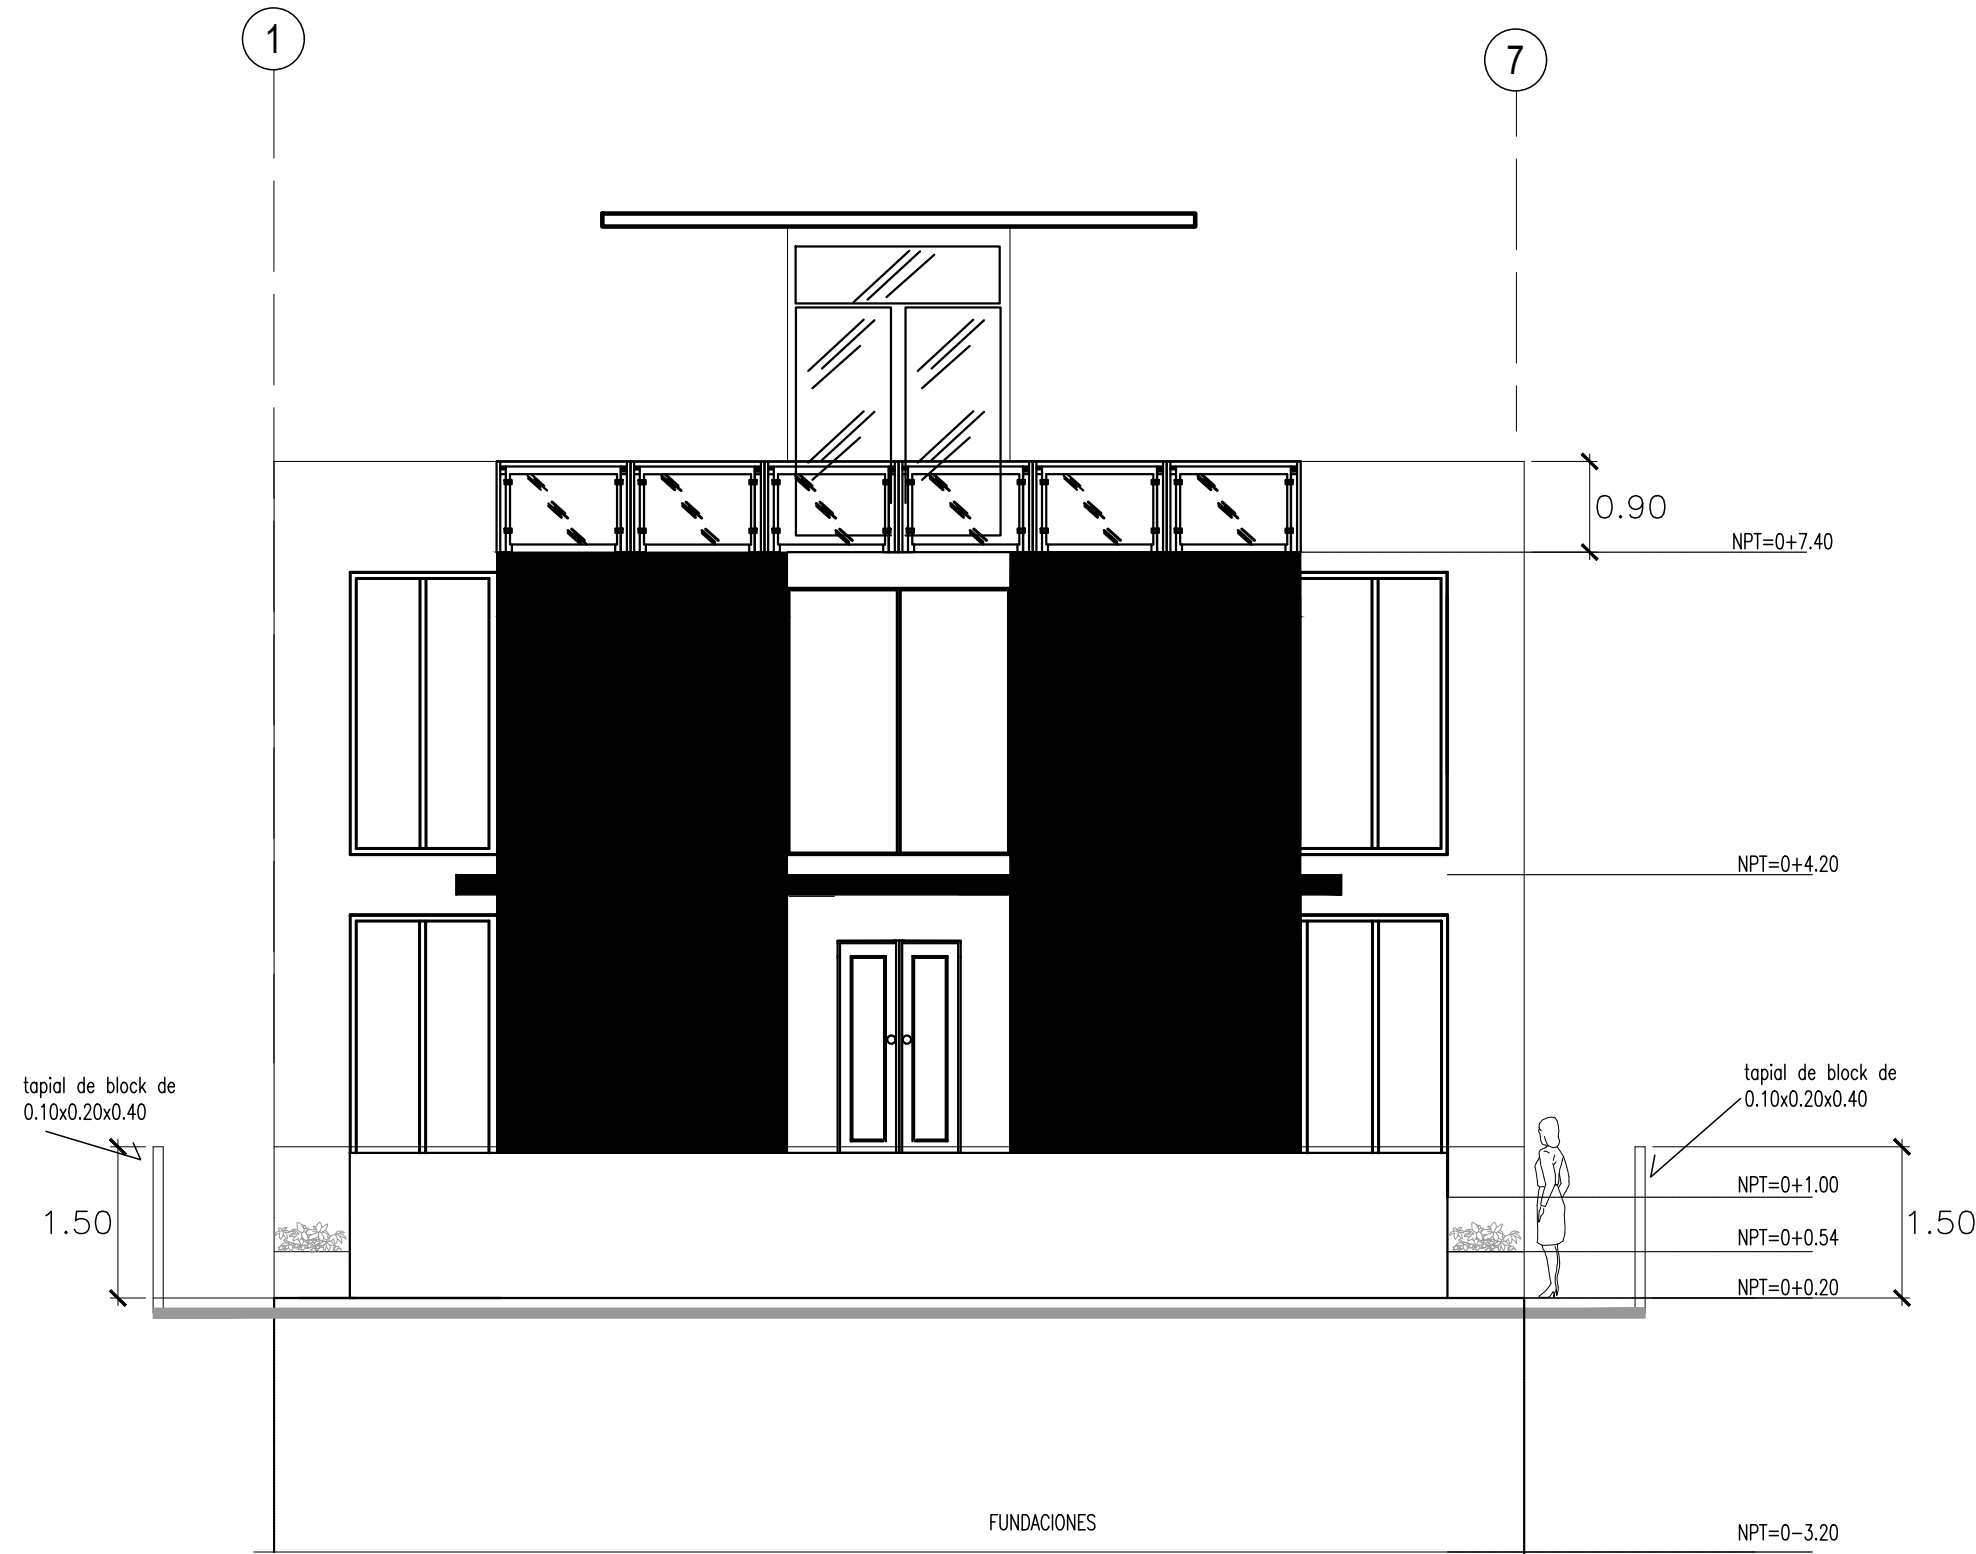


FACHADA PRINCIPAL
ESC. 1:75

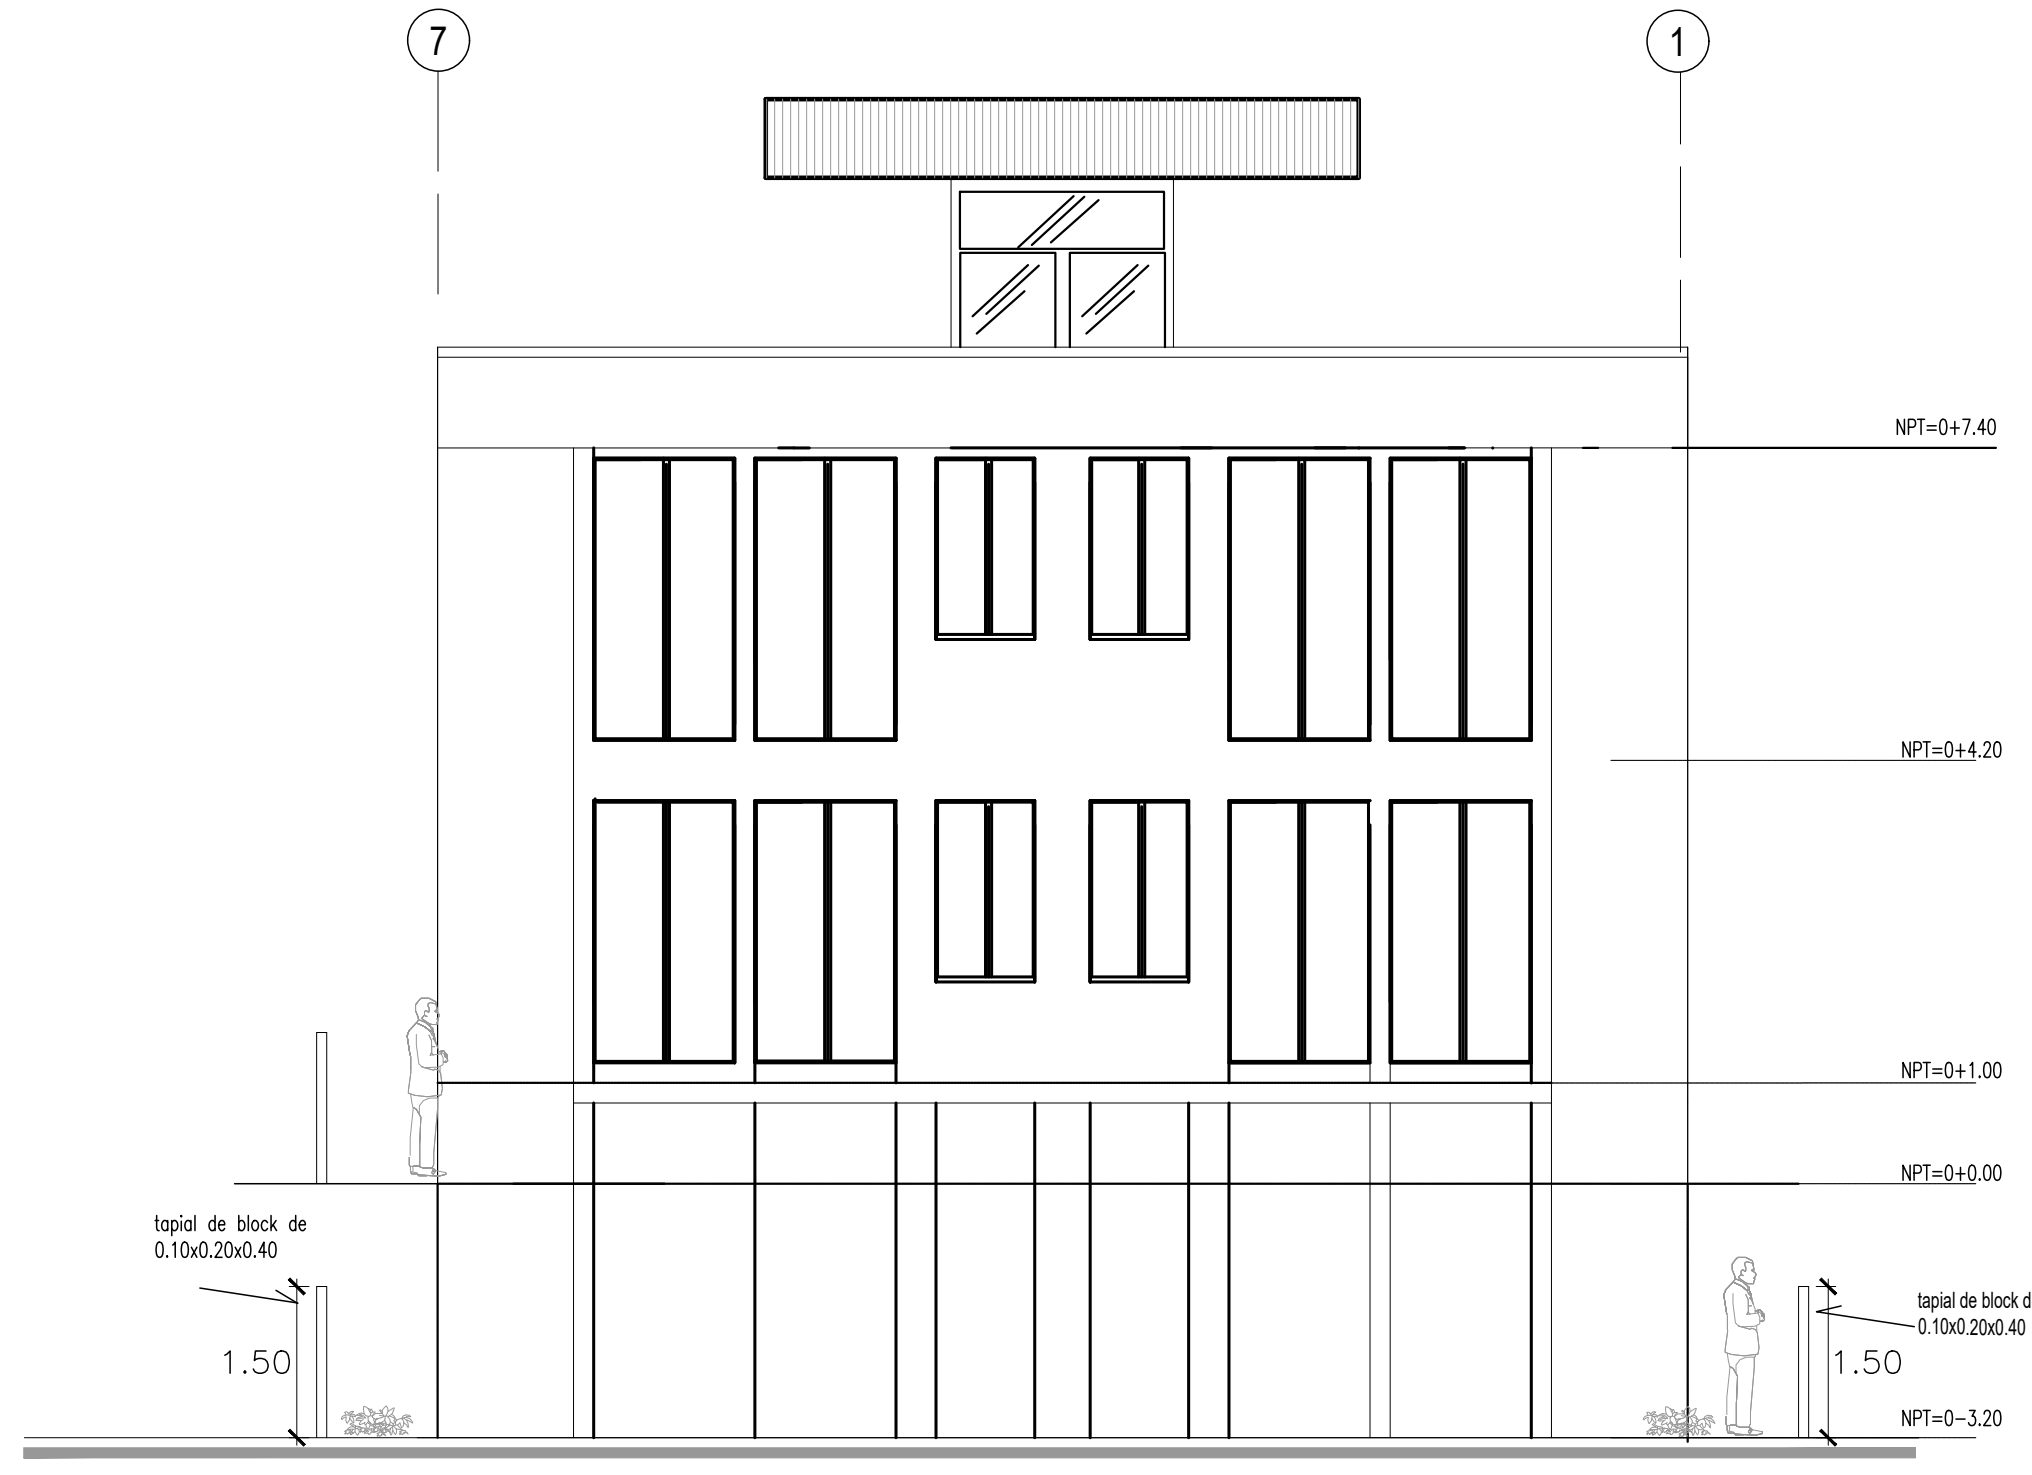

FACHADA POSTERIOR
ESC. 1:75

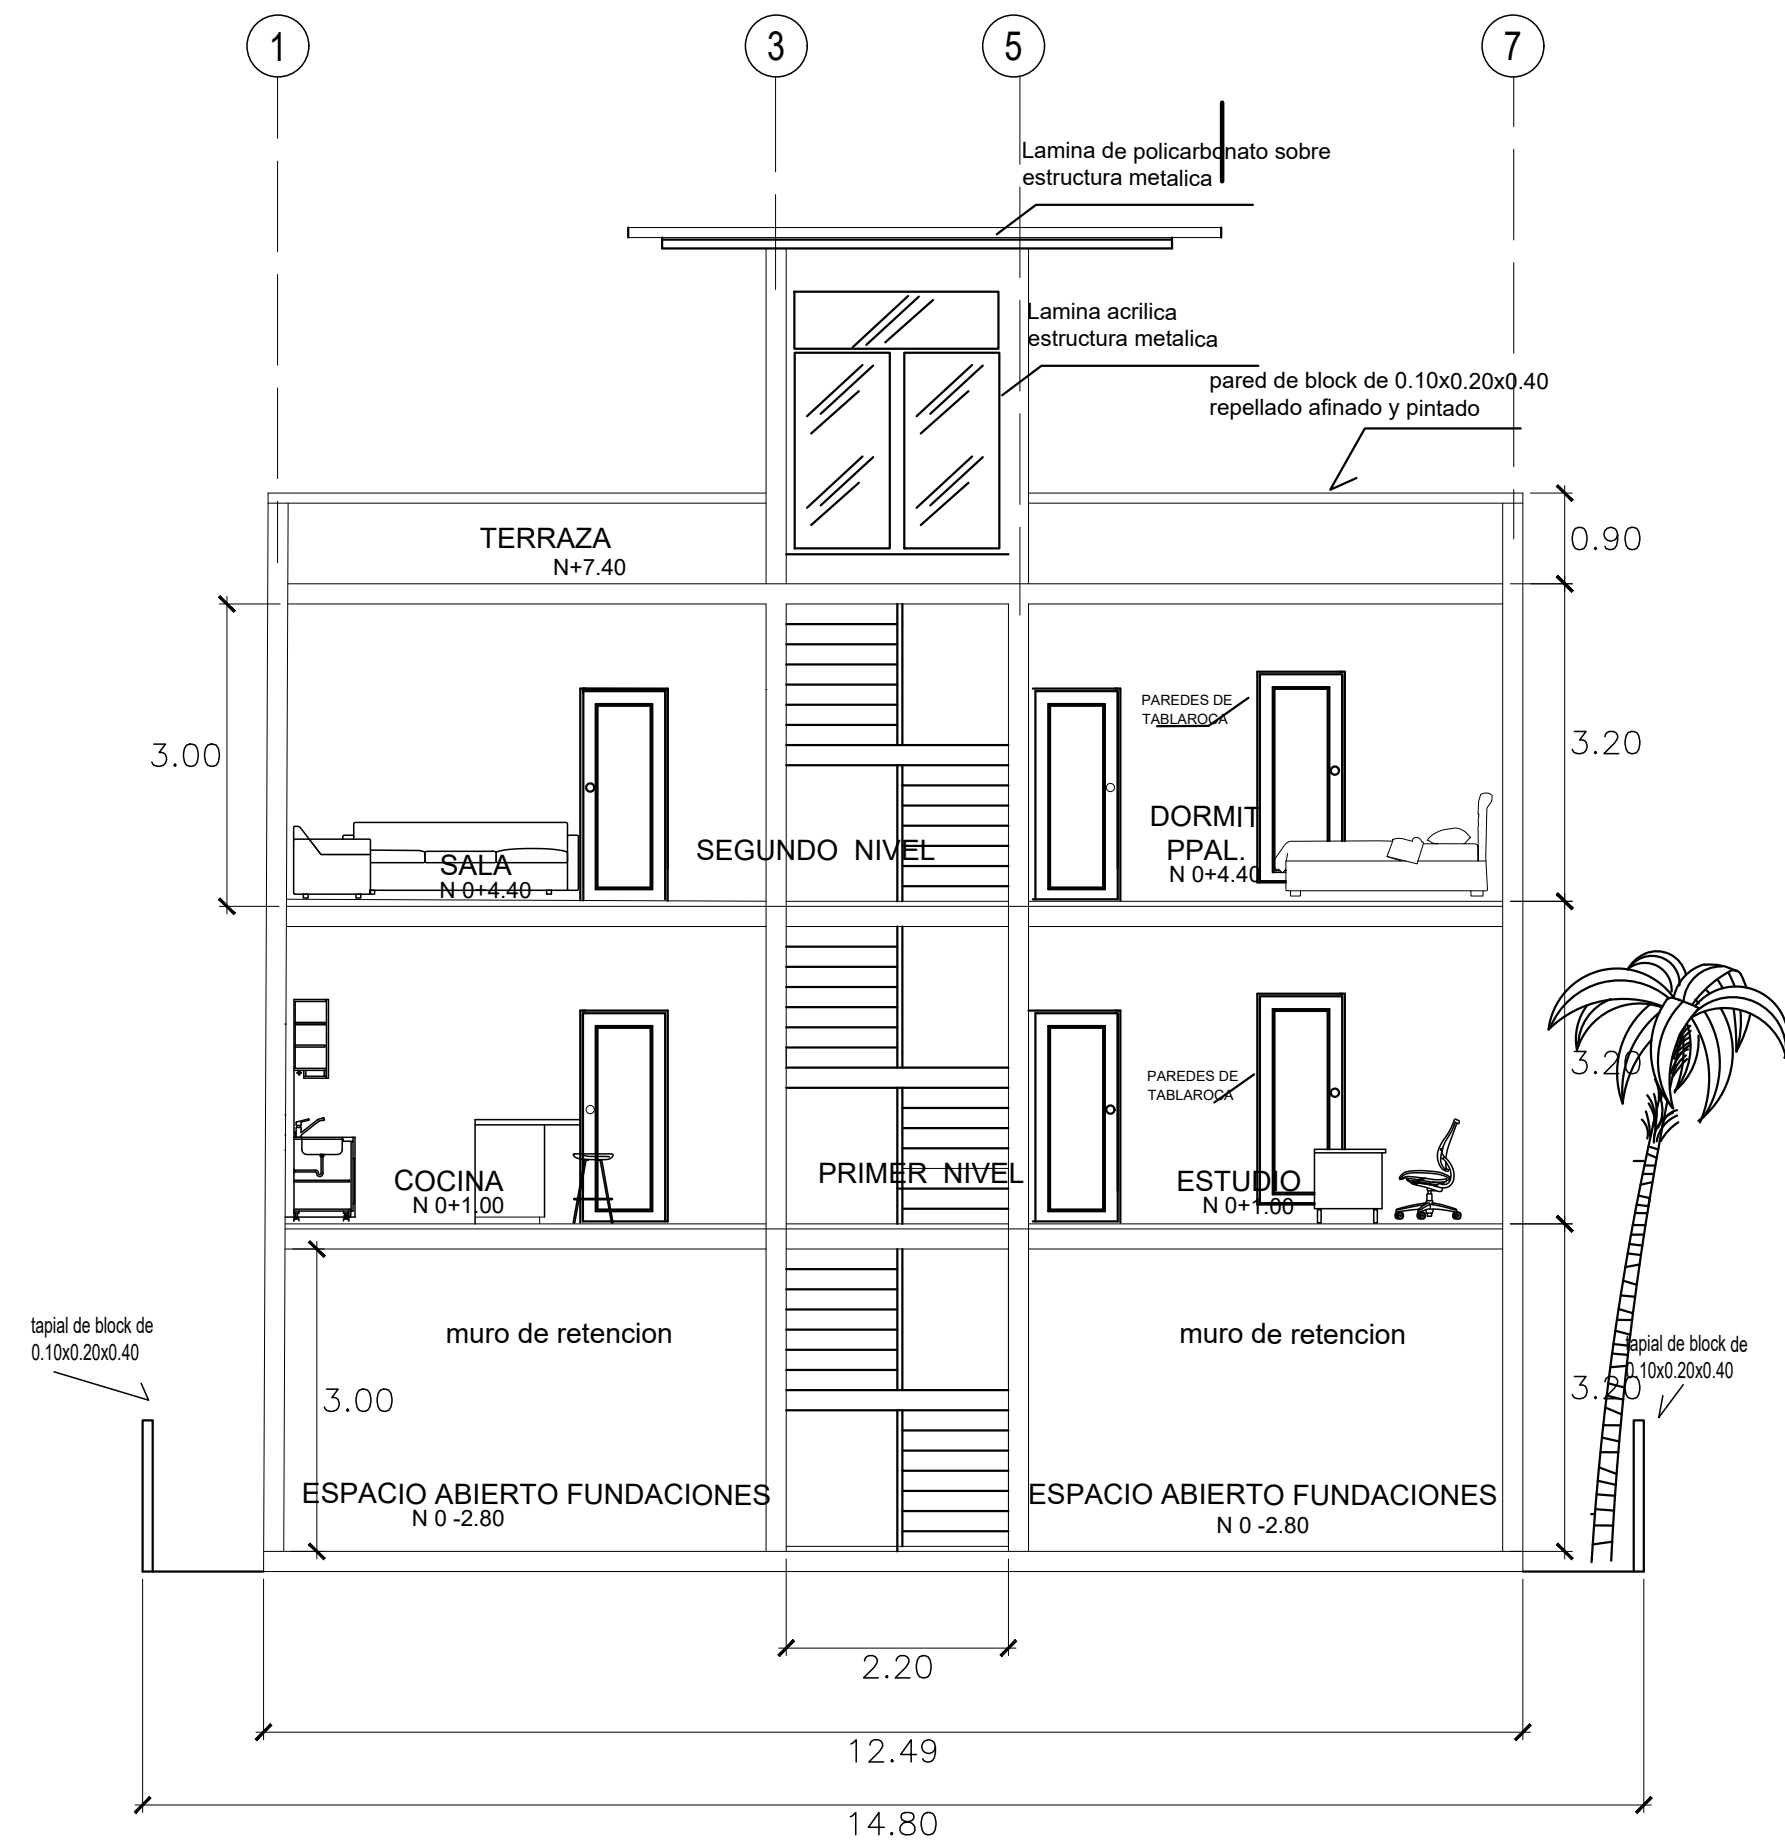

SECCION A A'
ESC. 1:75

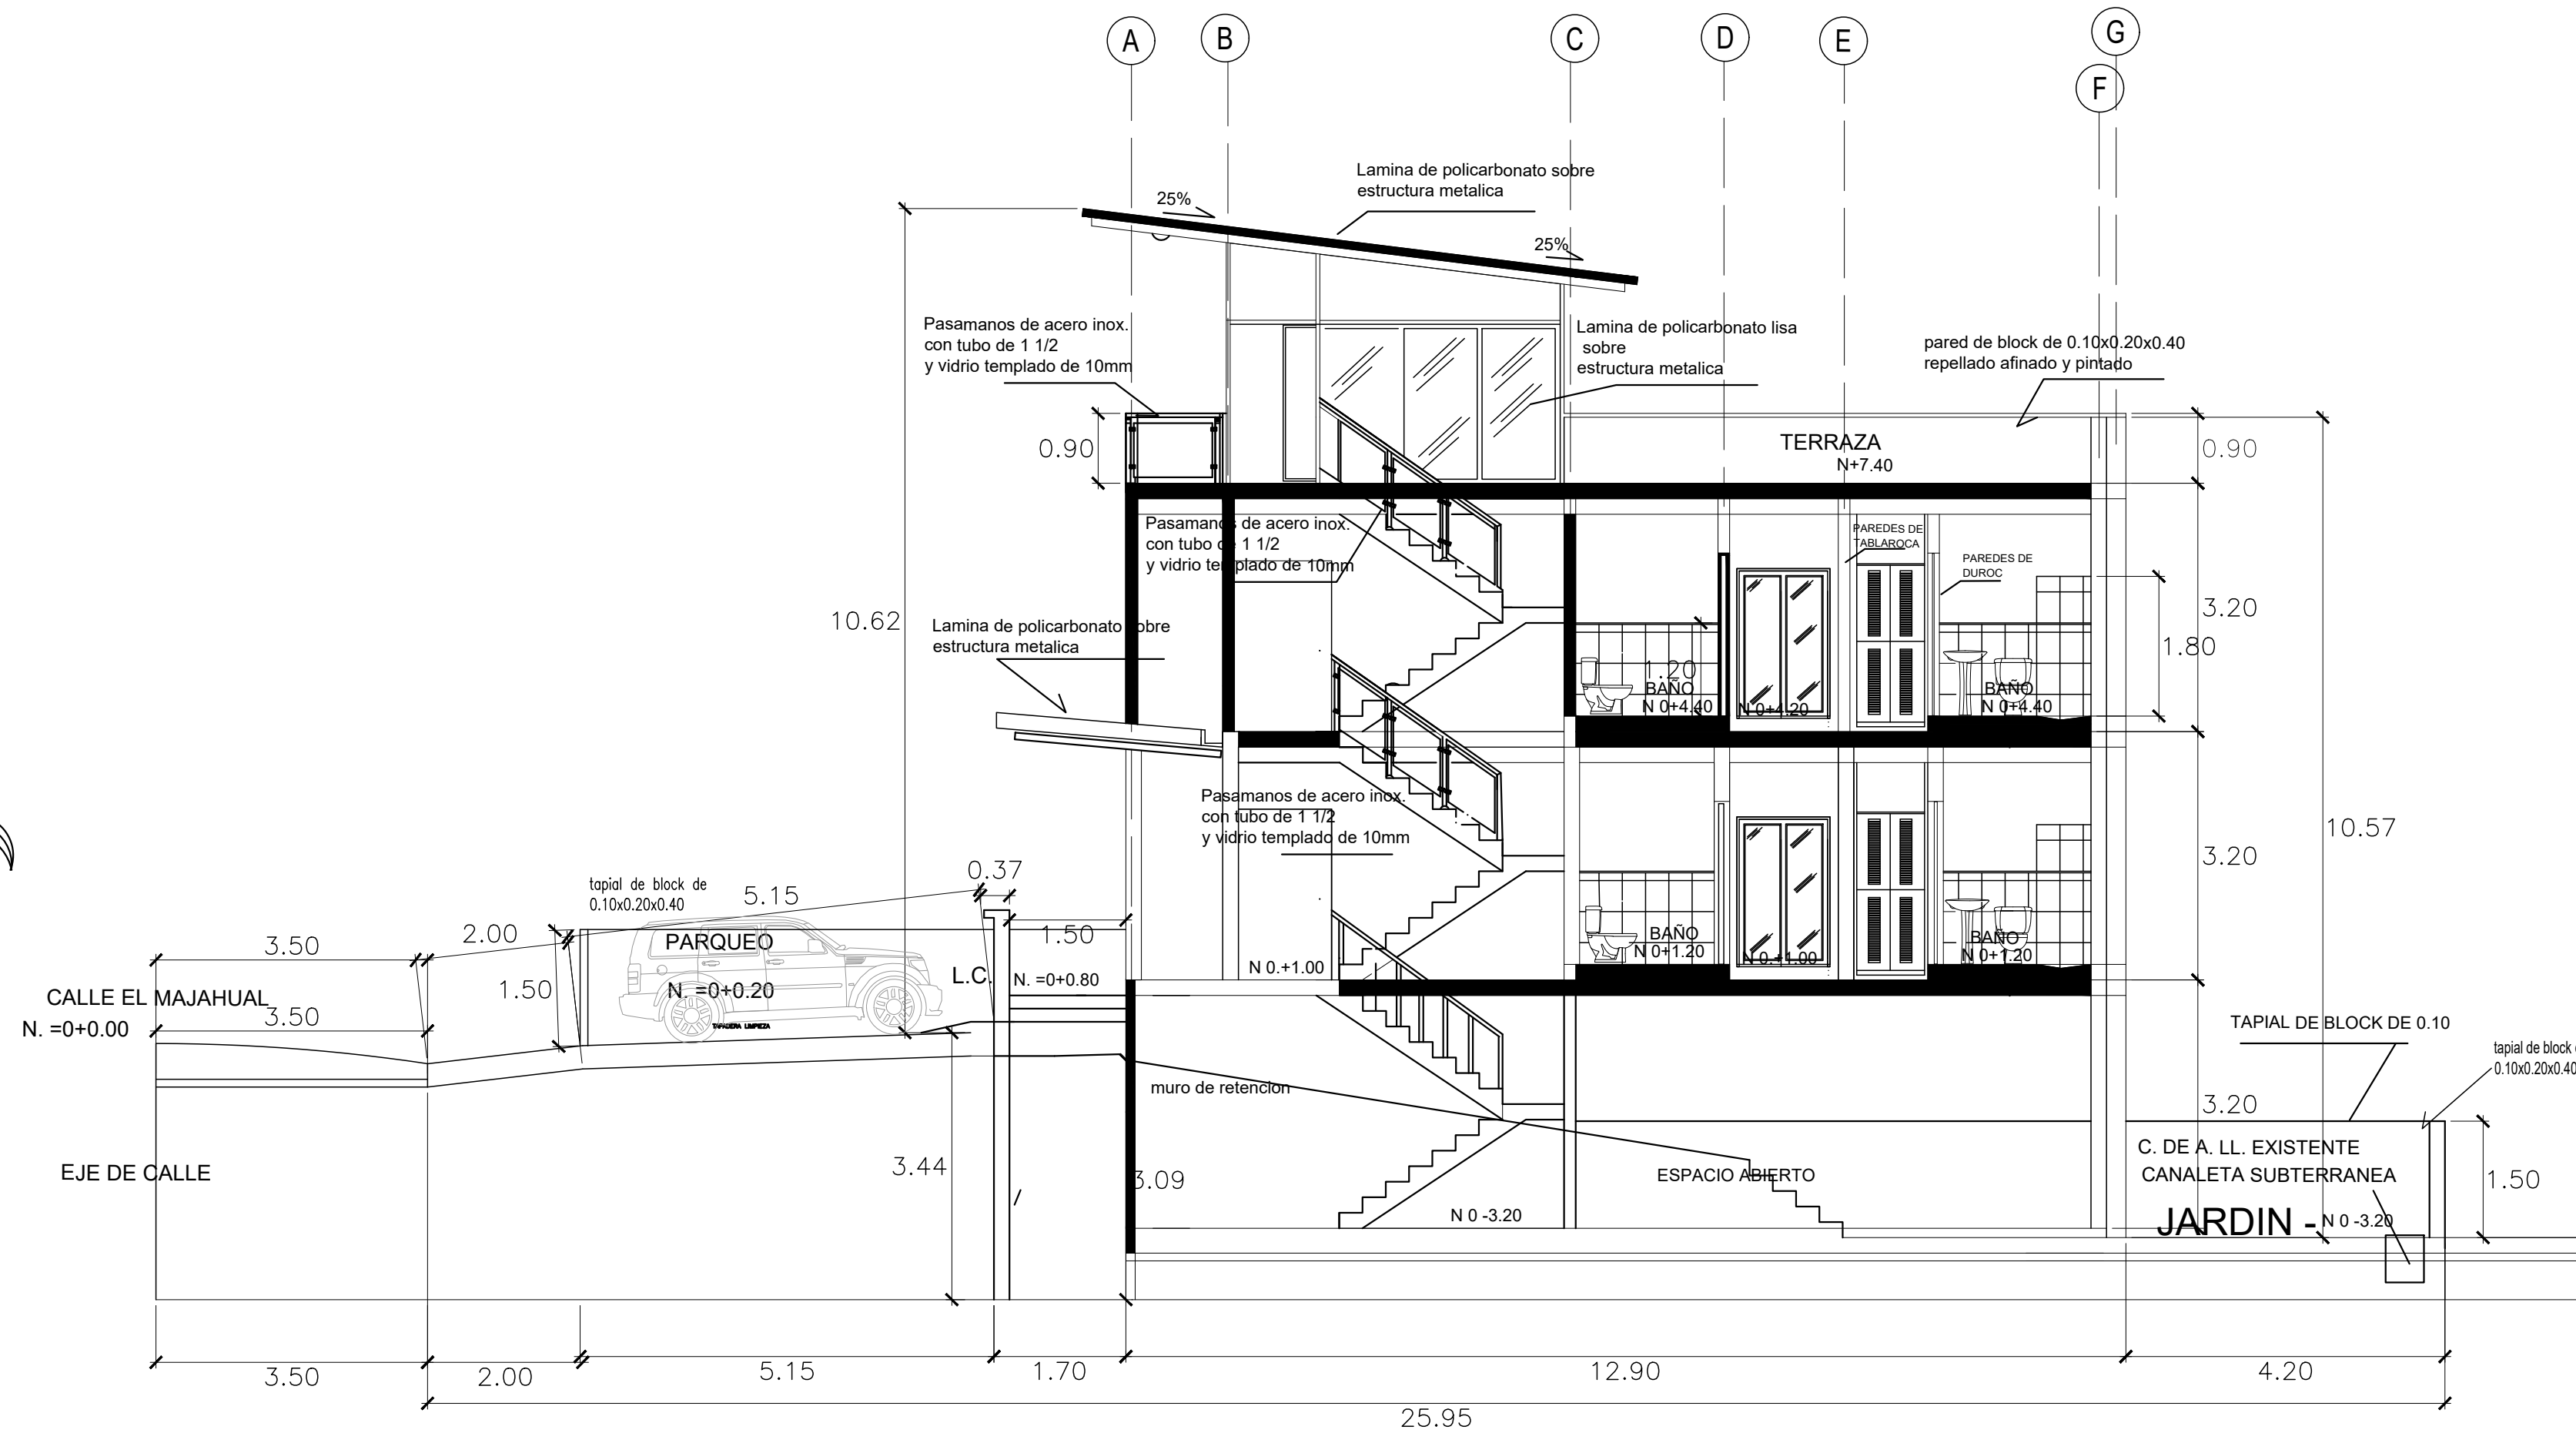

SECCION B B'
ESC. 1:75

SELLOS DE APROBACION:

ESTE PLANO FORMA PARTE INTEGRAL DE LA RESOLUCION EMITIDA EN FECHA 24 DE JULIO DE 2025 EN FORMATO DIGITAL Y CORRESPONDE AL EXPEDIENTE DE PERMISO DE CONSTRUCCION REFERENCIA 0333-2025, PRESENTADO BAJO LA RESPONSABILIDAD DE LA ARQ. MORENA GUADALUPE VASQUEZ LOPEZ CON REGISTRO PROFESIONAL VMVDU A-4576.

PRESENTA:

ARQ. KARLA RODRIGUEZ DE CHOCOBAR

PROYECTO
CONSTRUCCION DE VIVIENDA DE DOS NIVELES
Y TERRAZA EMPRESA AZZUL

PROPIETARIOS

EMPRESA AZZUL S.A DE C. V

UBICACION:
CANTON SAN RAFAEL, CONDOMINIO RECREATIVO, LOMAS DE SAN BLAS, CALLE MAJAHUAL, POLIGONO 6, NUMERO 18, LA LIBERTAD COSTA, DEPARTAMENTO DE LA LIBERTAD

CONTENIDO:

SECCIONES Y FACHADAS

ESCALA:
INDICADA

FECHA:
MARZO 2025

HOJA N°:
ARQ-02

FIRMA Y SELLO DE PROFESIONALES RESPONSABLES

DISEÑO ARQUITECTÓNICO:
FIRMA:

DISEÑO ARQUITECTÓNICO:
SELLO:

REGISTRO NACIONAL DE ARQUITECTOS E INGENIEROS
CARLA PATRICIA RODRIGUEZ DE CHOCOBAR
A-2339
ARQUITECTA

DIRECTOR DE LA OBRA:
FIRMA:


DIRECTOR DE LA OBRA:
SELLO:

REGISTRO NACIONAL DE ARQUITECTOS E INGENIEROS
CARLOS FRANCISCO GALICIA MAEDA
A-3297
ARQUITECTO


RESPONSABLE DEL TRAMITE:
FIRMA:

RESPONSABLE DEL TRAMITE:
SELLO:


REGISTRO NACIONAL DE ARQUITECTOS E INGENIEROS
Morena Guadalupe Vásquez López
A-4576
ARQUITECTA

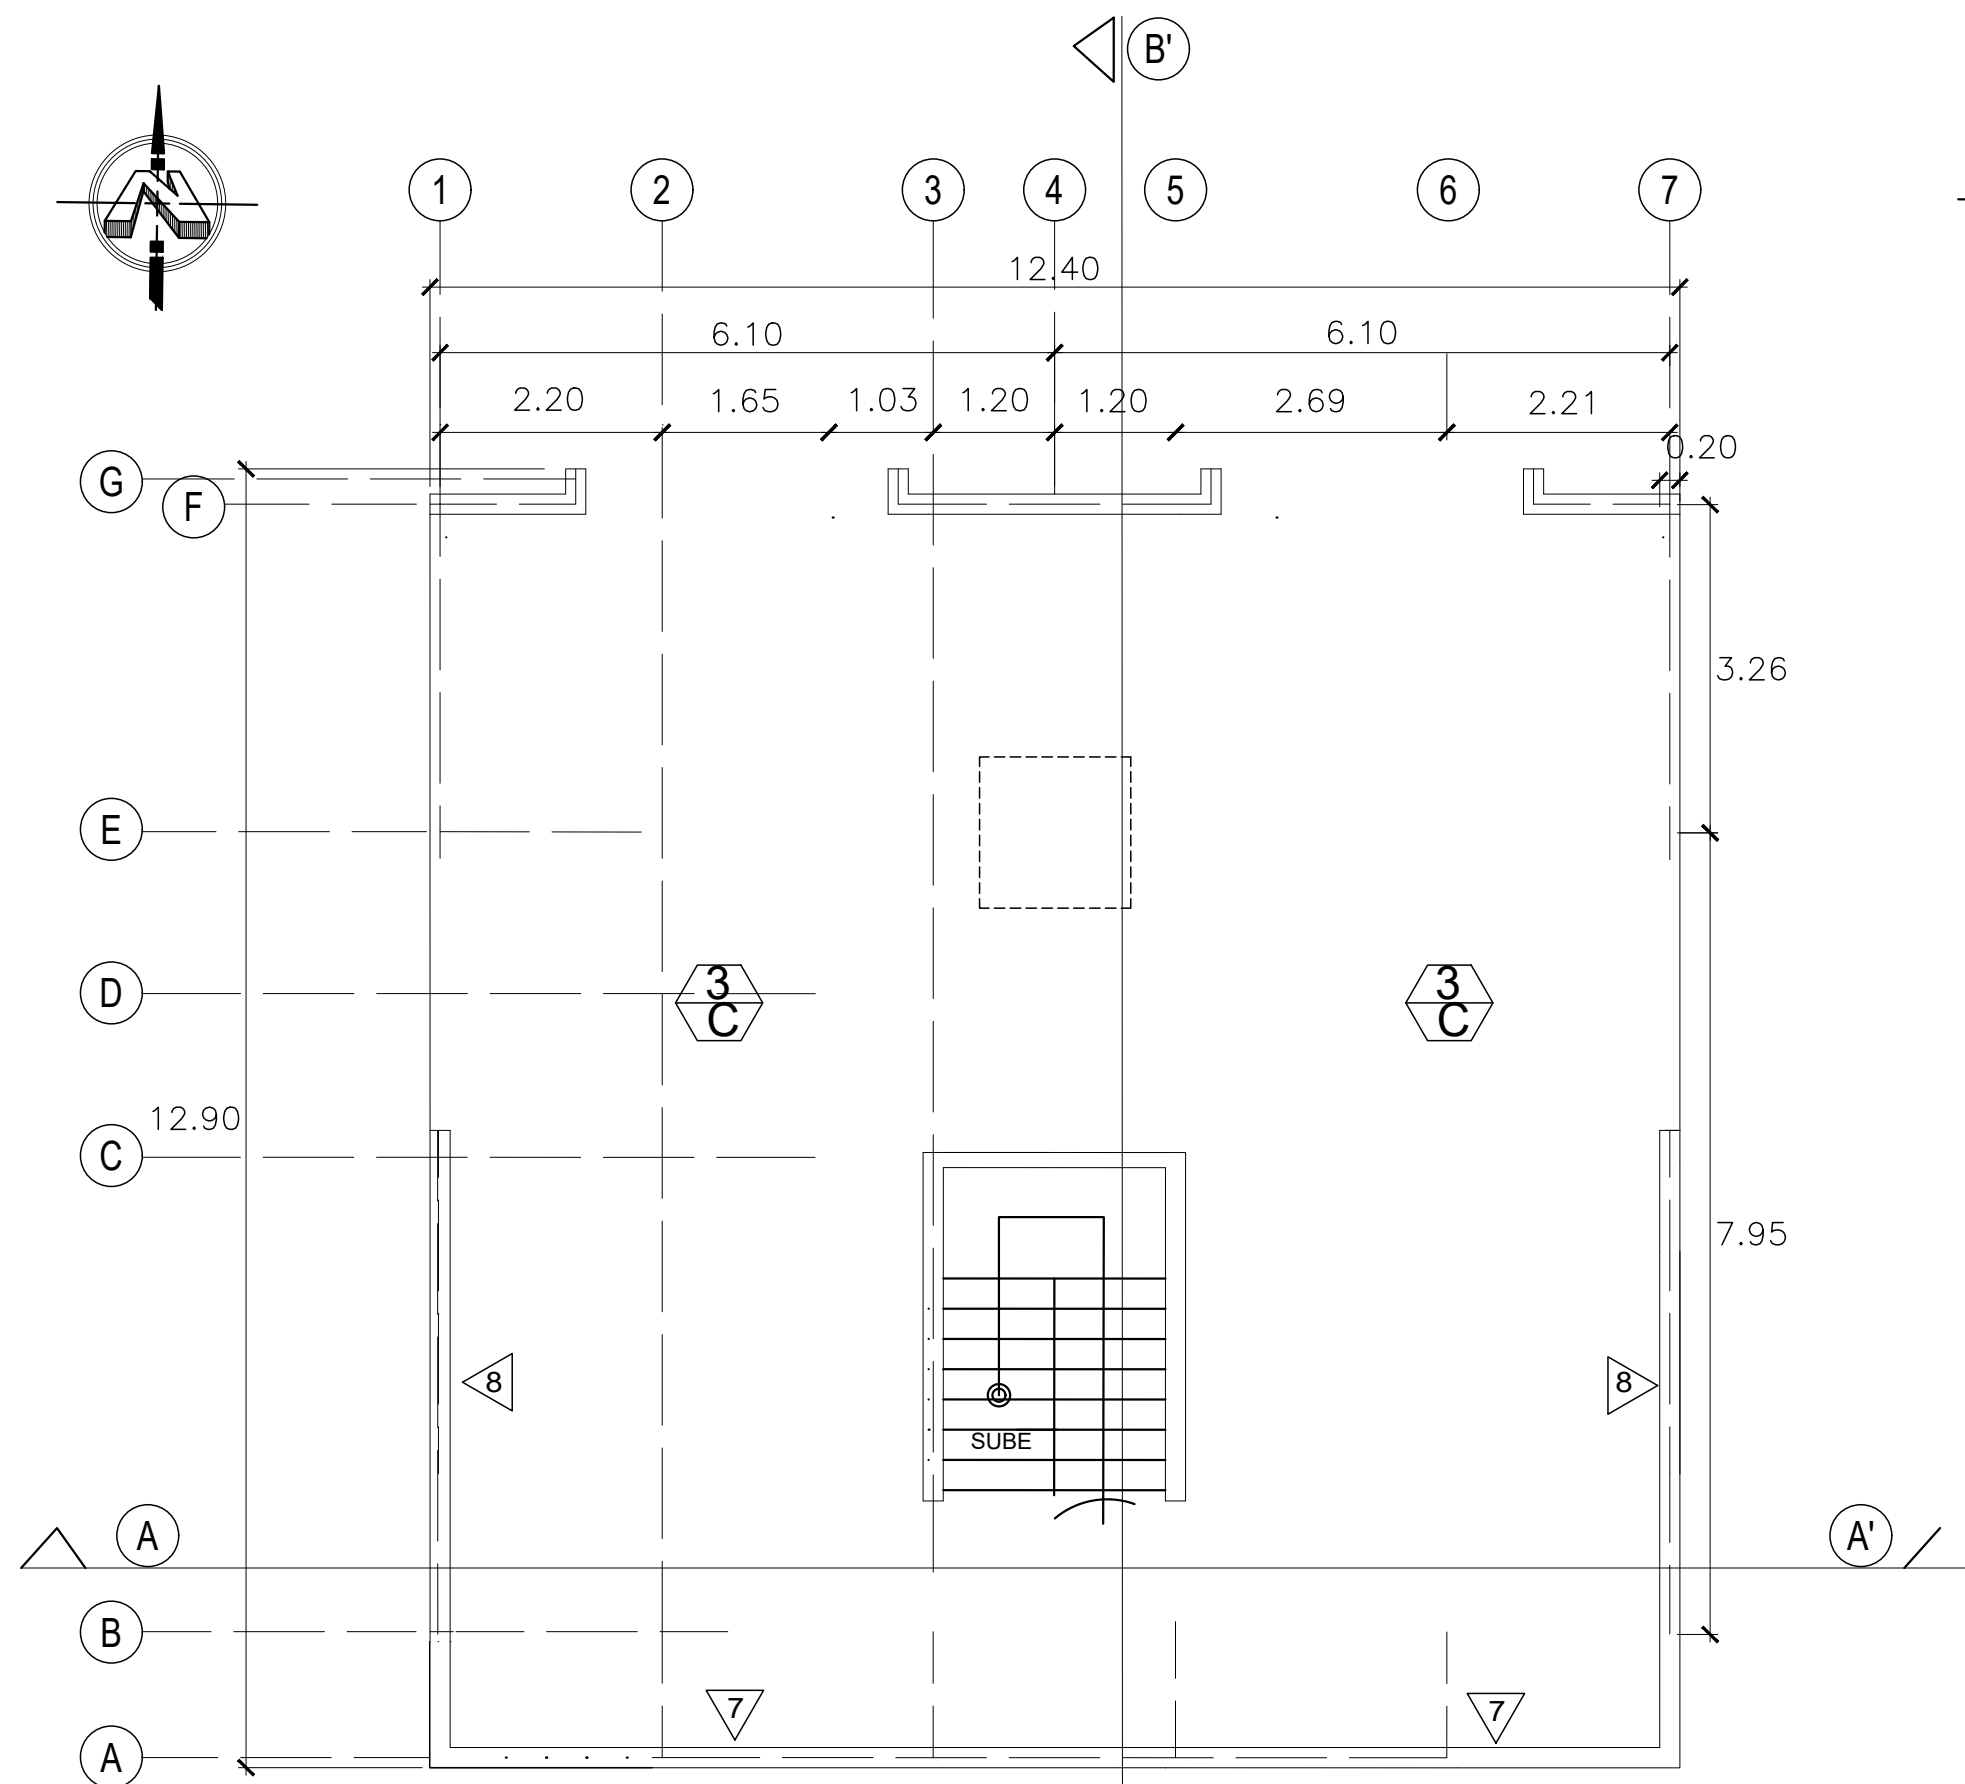


PLANTA DE ACABADOS
NIVEL FUNDACION
ESC. 1:75

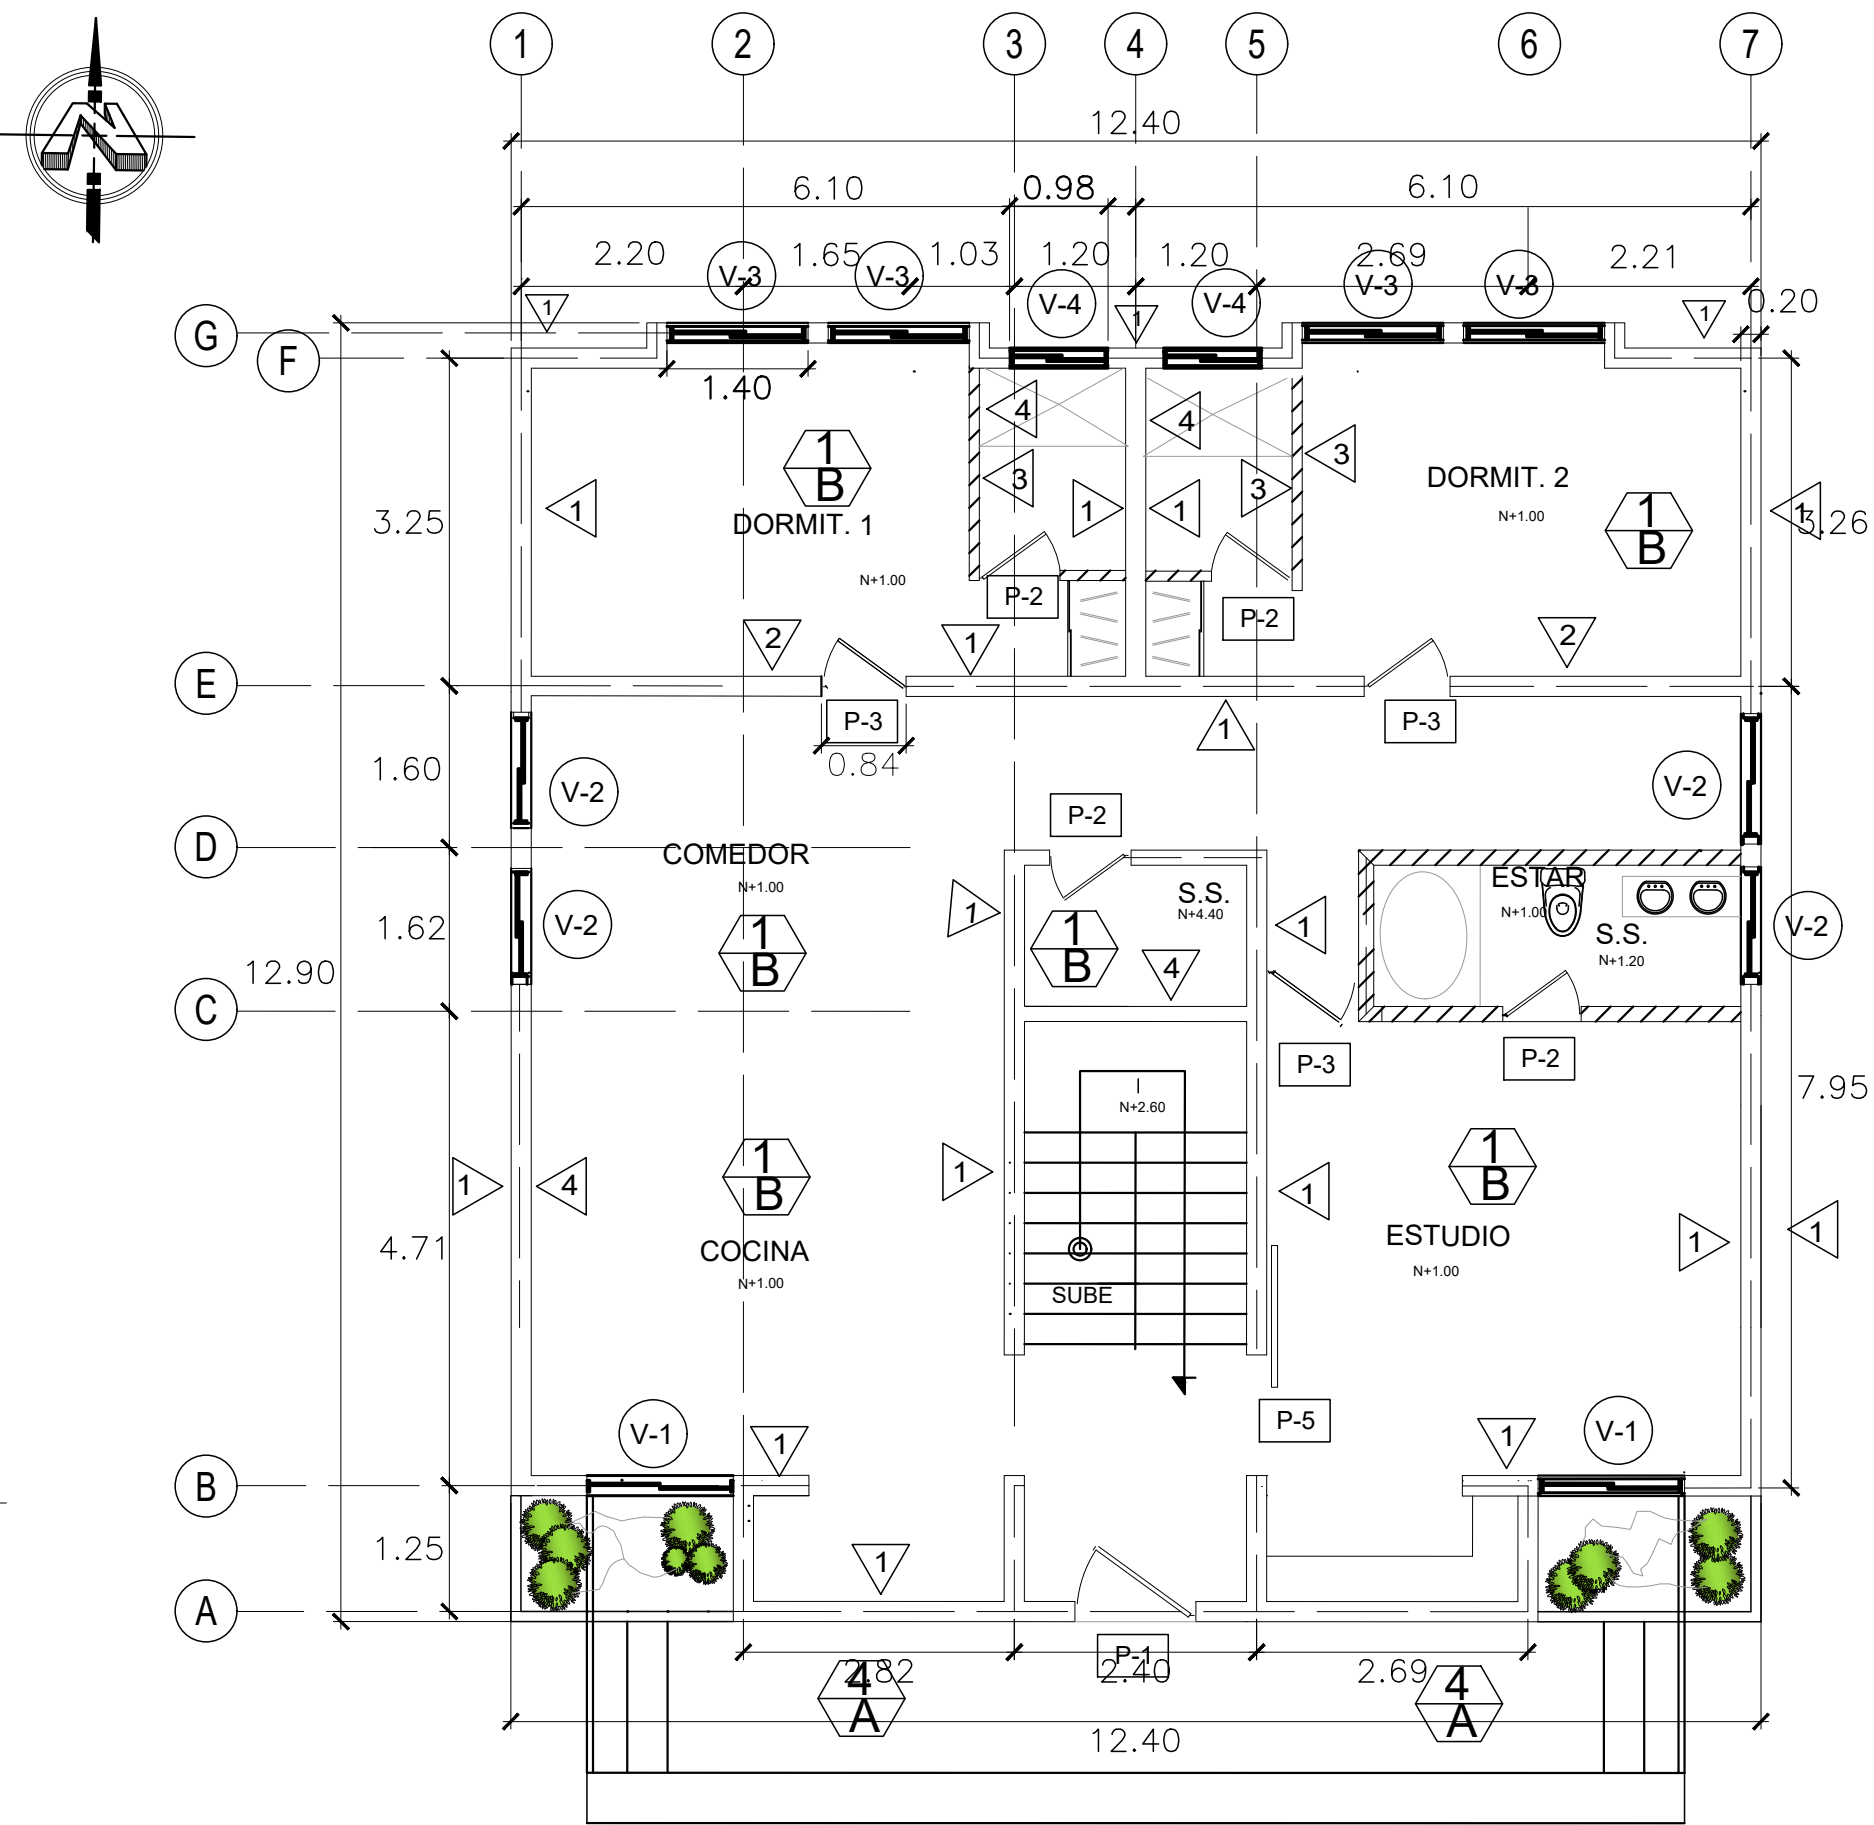

PLANTA DE ACABADOS
PRIMER NIVEL
ESC. 1:75

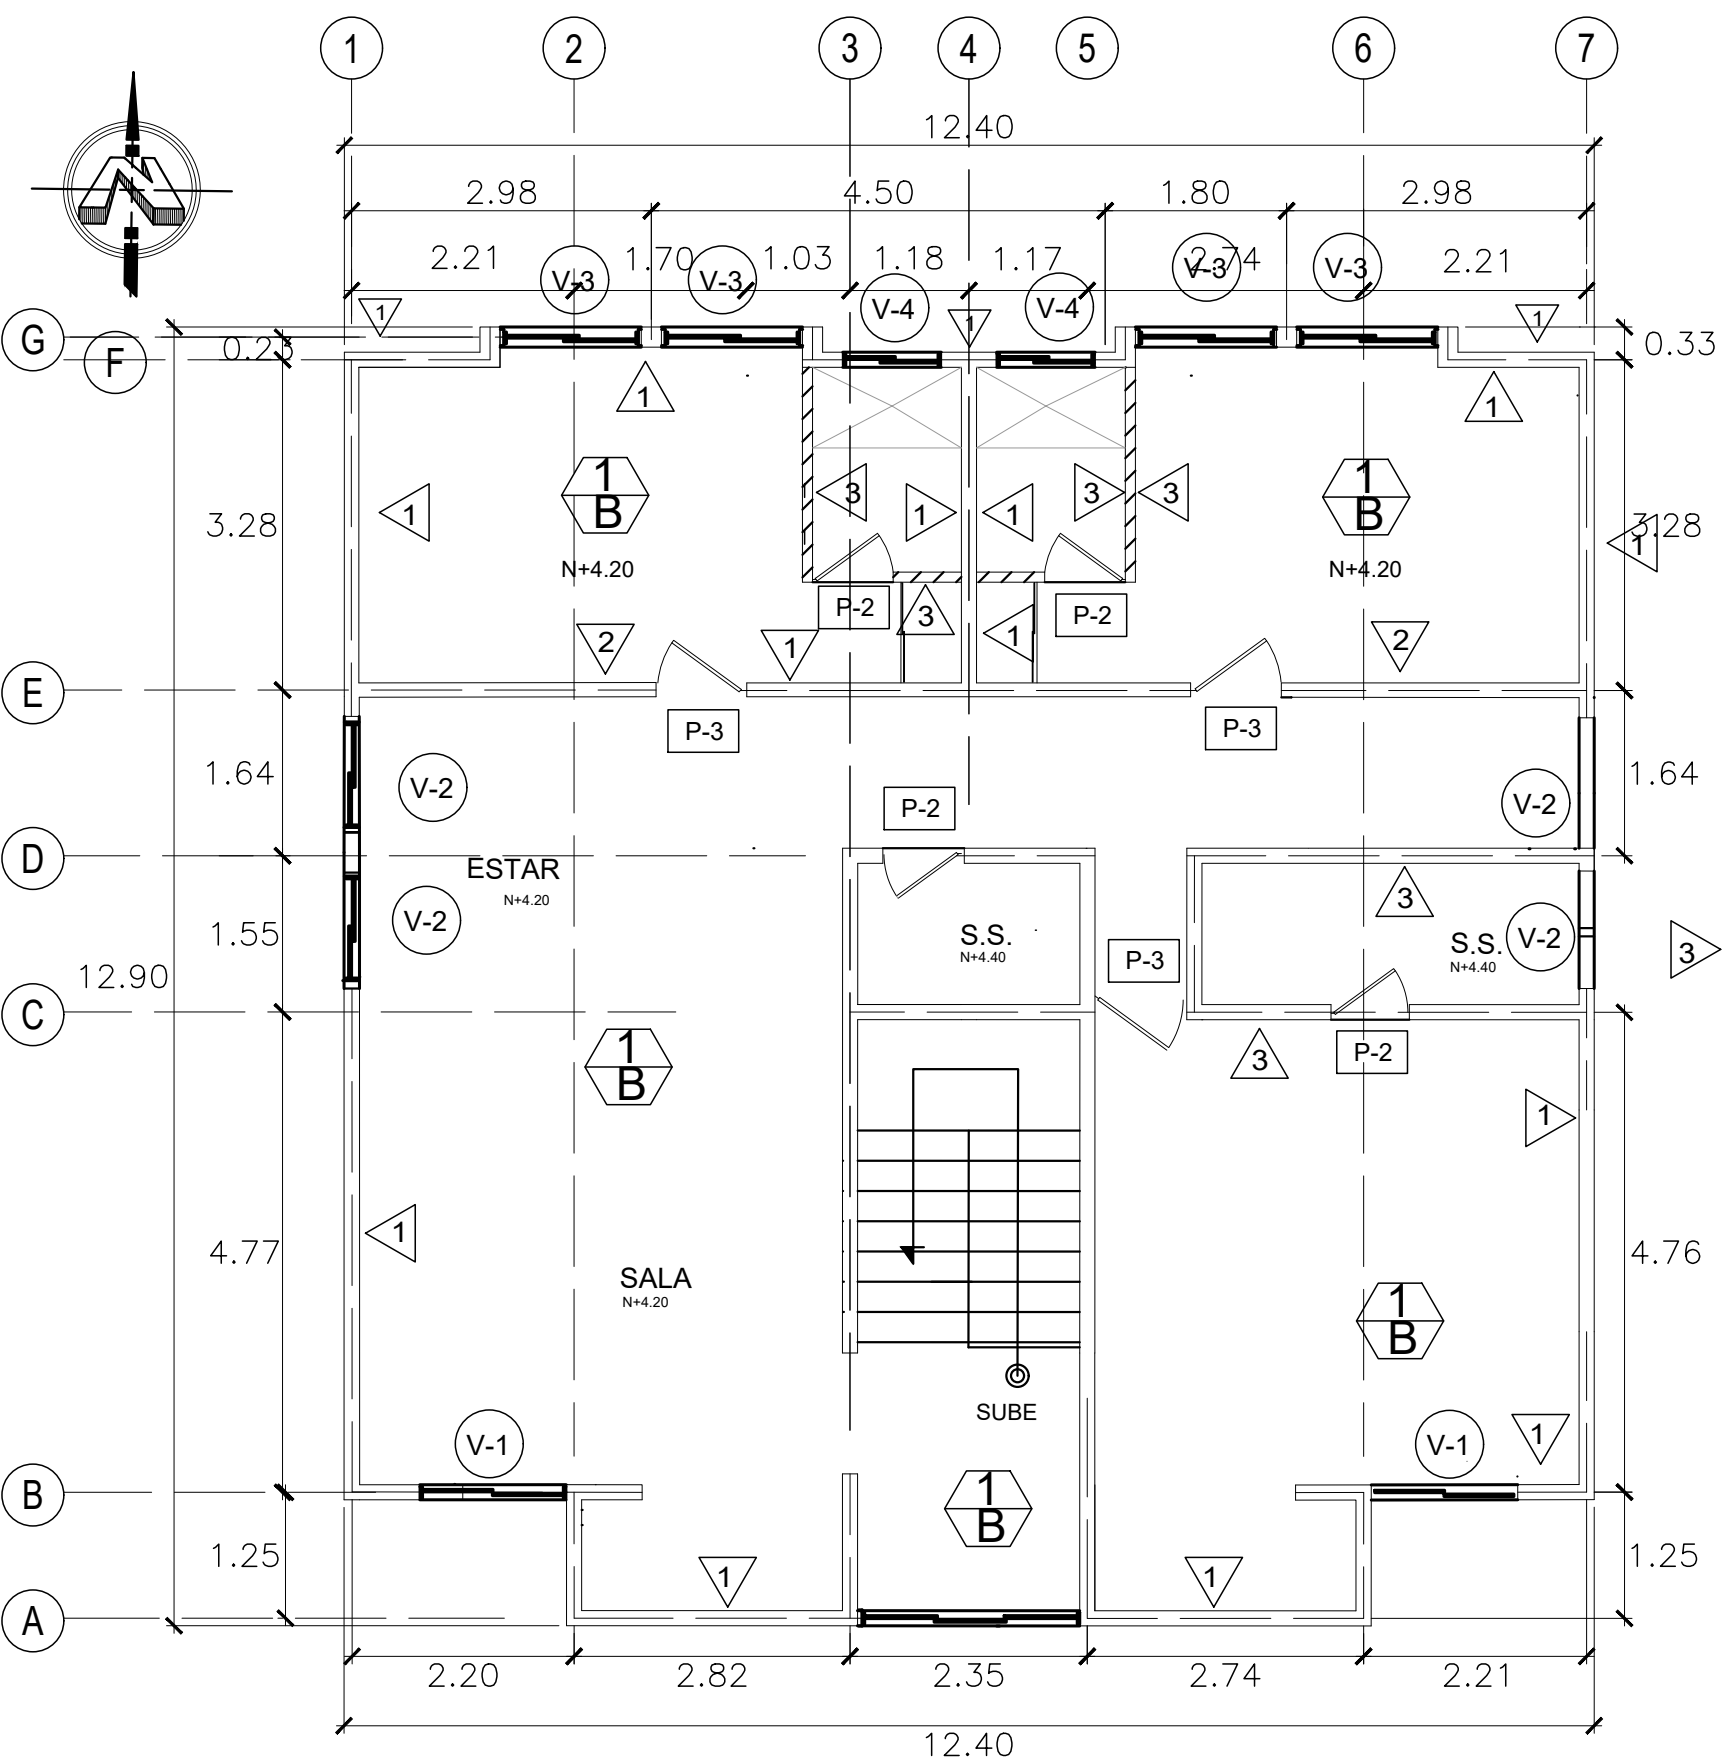

PLANTA ACABADOS
SEGUNDO NIVEL
ESC. 1:75

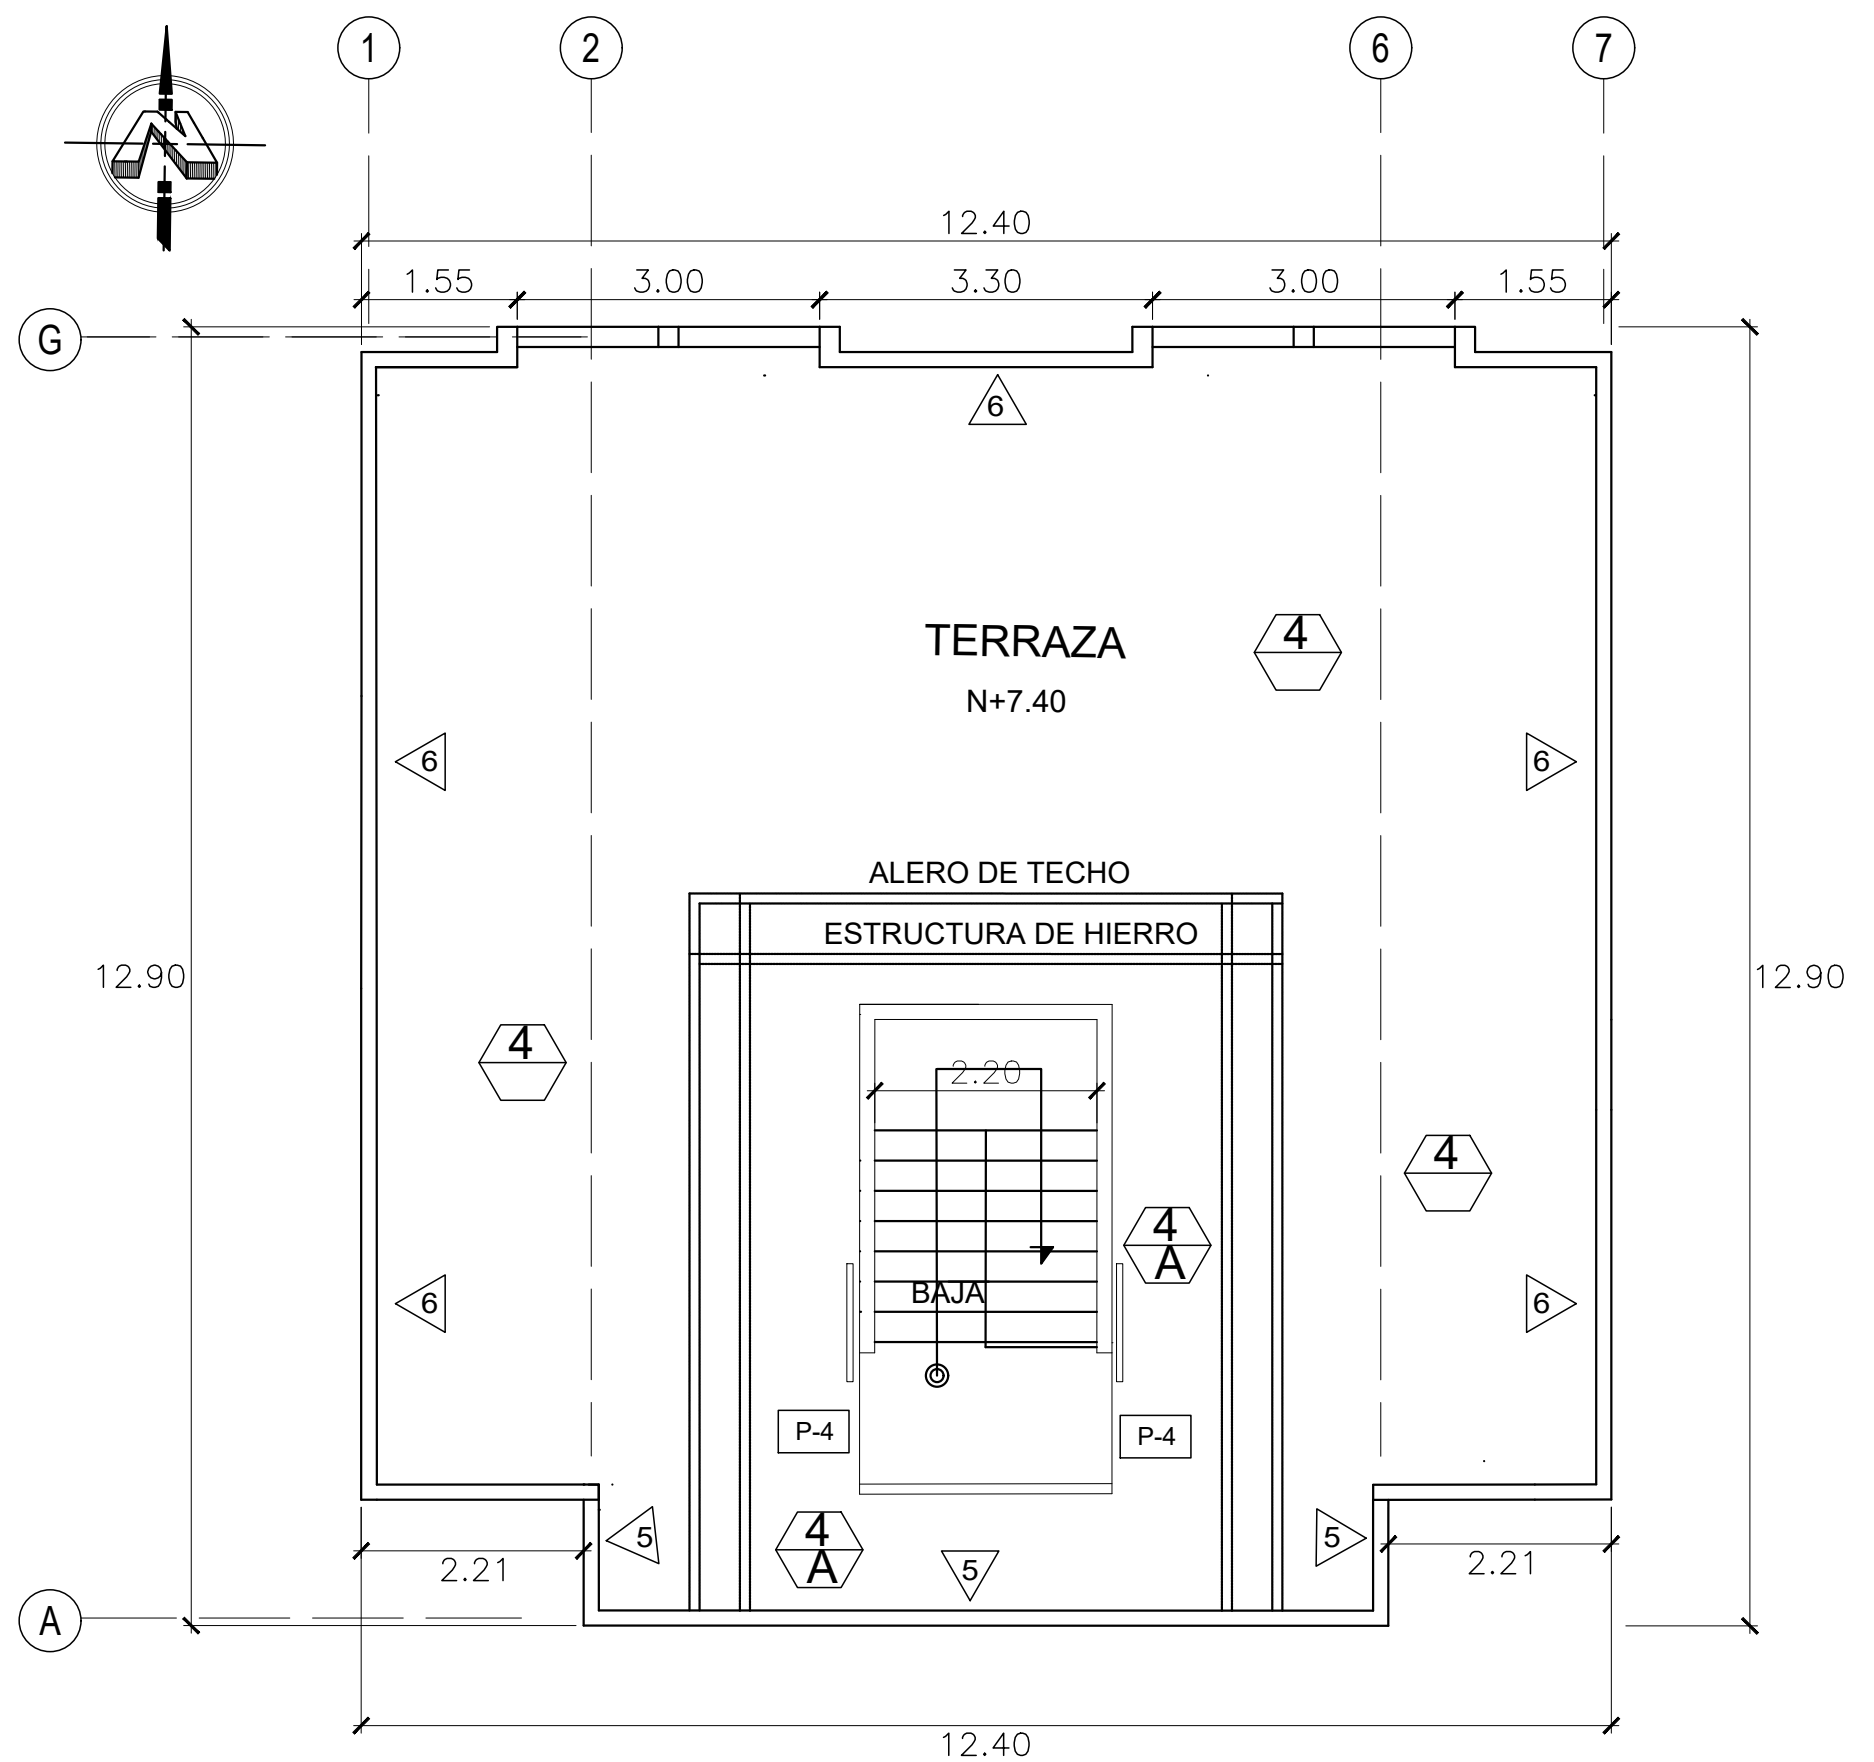

PLANTA ACABADOS
TERRAZA
ESC. 1:75

CUADRO DE ACABADOS	
PISOS	
1	PISO DE LADRILLO PORCELANATO PARA INTERIORES
2	PISO PARA BAÑO ANTIDELIZANTE
3	PISO DE CONCRETO
4	PISO TIPO TERRAZO
5	GRAMA SAN AGUSTIN
6	GRAMOQUIN
7	CARRILERA DE CONCRETO
PAREDES	
1	PAREDES DE BLOCK REPELLADA AFINADAS Y PINTADAS
2	PAREDES DE TABLAROCA CON PERFILERIA DE ALUMINIO
3	PAREDES DE DURLOCK CON PERFILERIA DE ALUMINIO
4	AZULEJO, EN BAÑOS H=1.20 Y DUCHA 1.80 Mts Y COCINA H=1.20Mts. ENCHAPE DE AZULEJO DECORADA DE 0.40MTS DE ANCHO
5	MURO DE BLOCK DE 0.15x0.20x0.40, DOBLE PANTALLA. SIZADO
6	MURO DE BLOCK DE 0.15x0.20x0.40, SIZADO
CIELOS	
A	CIELO FALSO DE TIPO PVC COLOR MADERA Y ESTRUCTURA DE HIERRO
B	CIELO FALSO DE TABLAROCA Y PERFILERIA DE ALUMINIO
C	CIELO FALSO DE TABLAROCA Y PERFILERIA DE ALUMINIO

CUADRO DE PUERTAS					
PUERTA	ANCHO	ALTO	AREA M2	N° PUERTAS	MATERIAL
1	1.20	2.10	2.52	1	Madera de cedro y melamina
2	0.80	2.10	1.68	6	Puerta de madera prensada, tipo americana color blancas
3	0.90	2.10	1.89	7	Puerta de madera prensada, tipo americana color blancas
4	1.20	2.10	2.52	1	Puerta de policarbonato y estructura metálica
5	1.20	2.10	2.52	1	Puerta corrediza, prensada

CUADRO DE VENTANAS					
VENTANA	ANCHO	ALTO	AREA M2	N° VENTANAS	H. REPISA
1	1.50	1.70	2.55	4	0.40
2	1.20	1.70	2.04	8	0.40
3	1.40	1.70	1.54	8	0.40
4	1.00	1.10	1.10	4	0.40
5	1.00	1.70	2.55	1	0.40

SELLOS DE APROBACION:

ESTE PLANO FORMA PARTE INTEGRAL DE LA RESOLUCION EMITIDA EN FECHA 24 DE JULIO DE 2025 EN FORMATO DIGITAL Y CORRESPONDE AL EXPEDIENTE DE PERMISO DE CONSTRUCCION REFERENCIA 0333-2025, PRESENTADO BAJO LA RESPONSABILIDAD DE LA ARQ. MORENA GUADALUPE VASQUEZ LOPEZ CON REGISTRO PROFESIONAL VMVDU A-4576.

PRESENTA:

ARQ. KARLA RODRIGUEZ DE CHOCOBAR

PROYECTO
CONSTRUCCION DE VIVIENDA DE DOS NIVELES
Y TERRAZA EMPRESA AZZUL

PROPIETARIOS

EMPRESA AZZUL S.A DE C. V

UBICACION:

CANTON SAN RAFAEL, CONDOMINIO RECREATIVO, LOMAS DE SAN BLAS, CALLE MAJAHUAL, POLIGONO 6, NUMERO 18, LA LIBERTAD COSTA, DEPARTAMENTO DE LA LIBERTAD

CONTENIDO:

PLANTAS DE ACABADOS
NIVEL FUNDACION, NIVEL 1, NIVEL 2
Y TERRAZA
CUADROS DE SIMBOLOGIA DE ACABADOS

ESCALA:
INDICADA

FECHA:
MARZO 2025

HOJA N°:
ARQ-03

FIRMA Y SELLO DE PROFESIONALES RESPONSABLES

DISEÑO ARQUITECTÓNICO:
FIRMA:

DISEÑO ARQUITECTÓNICO:
SELLO:

REGISTRO NACIONAL DE ARQUITECTOS E INGENIEROS
CARLA PATRICIA RODRIGUEZ DE CHOCOBAR
A-2359
ARQUITECTA

DIRECTOR DE LA OBRA:
FIRMA:

DIRECTOR DE LA OBRA:
SELLO:

REGISTRO NACIONAL DE ARQUITECTOS E INGENIEROS
CARLOS FRANCISCO CALICHA MORA
A-3297
ARQUITECTO

RESPONSABLE DEL TRAMITE:
FIRMA:

RESPONSABLE DEL TRAMITE:
SELLO:

REGISTRO NACIONAL DE ARQUITECTOS E INGENIEROS
Morena Guadalupe Vázquez López
A - 4576
ARQUITECTA

NOTAS GENERALES

- EL CONSTRUCTOR ES RESPONSABLE POR LA VERIFICACIÓN Y CERTIFICACIÓN DE TODAS LAS DIMENSIONES Y MEDICIONES CONTENIDAS EN ESTOS PLANOS.
- CUANDO SE ENCUENTREN DISCREPANCIAS ENTRE LA INFORMACIÓN CONTENIDA EN ESTOS PLANOS Y LA DEL RESTO DE PLANOS QUE CONFORMAN EL PROYECTO DEBERÁ SER COMUNICADA AL DISEÑADOR (O AL SUPERVISOR) CON EL FIN DE ESTABLECER LAS MEDIDAS CORRECTIVAS.
- EL CONSTRUCTOR ES RESPONSABLE DE LA CORRECTA CONSTRUCCIÓN DE LOS ELEMENTOS ESTRUCTURALES PRESENTADOS EN ESTOS PLANOS.

NOTAS TÉCNICAS

A. CONCRETO

EL CONCRETO A UTILIZAR SERÁ DE PESO VOLUMÉTRICO NORMAL, CON UNA RESISTENCIA ÚLTIMA A LA COMPRESIÓN A LOS 28 DÍAS ($f'c$) DE 210 Kg/cm^2 . LOS MATERIALES A UTILIZAR EN LA ELABORACIÓN DE CONCRETO LLENARÁN LAS SIGUIENTES ESPECIFICACIONES:

- EL CEMENTO A UTILIZAR SERÁ PORTLAND TIPO I, QUE CUMPLA LA NORMA ASTM C1157 TIPO GU. LOS AGREGADOS DEBERÁN CUMPLIR LA NORMA ASTM C33, Y SU TAMAÑO MÁXIMO NO DEBERÁ DE EXCEDER DE 0.75 VECES LA SEPARACIÓN MÍNIMA ENTRE BARRAS DE REFUERZO DEL ELEMENTO A COLAR.
- EL AGUA DEBERÁ SER LIMPIA, LIBRE DE RESÍDUOS DE ACEITE, ÁCIDOS, ÁLCALIS, SALES, MATERIA ORGÁNICA U OTRA SUSTANCIA QUE PUEDAN SER DAÑINAS PARA EL MORTERO O CUALQUIER METAL EMBEBIDO EN EL CONCRETO. LA RELACIÓN AGUA-CEMENTO, PARA LA MEZCLA DE CONCRETO A UTILIZAR EN ELEMENTOS ESTRUCTURALES PRIMARIOS COMO CIMENTACIONES, VIGAS, COLUMNAS Y LOSAS NO DEBERÁ DE EXCEDER DEL 0.50.
- CUALQUIER TIPO DE ADITIVO A UTILIZAR EN LA MEZCLA DEBERÁ DE SER APROBADO PREVIAMENTE POR EL SUPERVISOR.

LA TOLERANCIA EN CUANTO A LAS DIMENSIONES GENERALES DE LA SECCIÓN DE UN ELEMENTO DE CONCRETO SERÁ DE ± 10 mm. Y LA TOLERANCIA EN CUANTO A LOS RECURRIMIENTOS SERÁ DE 6.0 mm. PODRÁ UTILIZARSE LAS TOLERANCIAS DEL CÓDIGO ACI-117 PARA LA CONSTRUCCIÓN DE TODOS LOS ELEMENTOS ESTRUCTURALES SIEMPRE Y CUANDO NO AFECTEN LA ARQUITECTURA.

B. ACERO DE REFUERZO

EL ACERO DE REFUERZO SERÁ GRADO 60 ($f_y=4200$ kg/cm^2) Y DEBERÁ CUMPLIR CON LA NORMA ASTM A-615 EXCEPTO LA VARILLA USA No.2 QUE TENDRÁ UN ESFUERZO DE FLUENCIA MÍNIMO DE 2320 kg/cm^2 . LAS LONGITUDES DE TRASLAPES Y GANCHOS ESTÁNDAR SERÁN DE ACUERDO AL ACI-318-08 PERO NO MENOR A LAS SIGUIENTES:
A) TABLA 1 : (NO TRASLAPAR MAS DEL 50% EN UNA MISMA SECCIÓN)

TABLA 1 ($f_y=4200$ KG/CM2 Y $f'c=210$ KG/CM2)								
CAIBRE	DIAMETRO (P.LO)	db (cm)	AREA (cm2)	Ld lecho sup. (cm)	Ld lecho inf. (cm)	Lt lecho sup. (cm)	Lt lecho inf. (cm)	L gh (cm)
3	0.375	0.95	0.71	55.0	42.0	70.0	54.0	15.00
4	0.500	1.27	1.27	72.0	55.0	94.0	72.0	21.00
5	0.625	1.59	1.98	90.0	69.0	117.0	90.0	26.00
6	0.750	1.91	2.85	108.0	83.0	141.0	108.0	32.00

C. RECUBRIMIENTO DEL ACERO DE REFUERZO

LOS RECUBRIMIENTOS MÍNIMOS DE CONCRETO A SER UTILIZADOS, A MENOS QUE EN DETALLES ESPECÍFICOS SE INDIQUEN OTROS VALORES, SERÁN LOS SIGUIENTES:

ZAPATAS – SOLERAS: 7.5 CM
LECHO INFERIOR, LECHO SUPERIOR Y DEMÁS CARAS 5.0 CM
TENSORES: 5 CM
PEDESTALES: 5 CM
COLUMNAS: 4 CM.
NERVIOS Y VIGAS: 3 CM

D. GANCHOS


TODOS LOS DOBLECES EN LAS VARILLAS DE REFUERZO DEBERÁN EFECTUARSE EN FRÍO. LOS DIÁMETROS INTERNOS DE DOBLEZ A SER UTILIZADOS SERÁN DE ACUERDO AL DETALLE SIGUIENTE:

- GANCHOS ESTÁNDAR A 90 Y 180 GRADOS = SEIS VECES EL DIÁMETRO DE LA VARILLA A DOBLAR.
- GANCHO A 135 Y 180 GRADOS EN ESTRIBOS = CUATRO VECES EL DIÁMETRO DE LA VARILLA A DOBLAR.


LA SEPARACIÓN MÍNIMA ENTRE VARILLAS PARALELAS DE REFUERZO, CUANDO ESTA NO SEAN ESPECIFICADAS COMO UN PAQUETE, SERÁ 25 MM. LAS VARILLAS LONGITUDINALES QUE DEBEN DE SER DOBLADAS POR REQUISITOS DE TRASLAPE O PASO A TRAVÉS DE NUDOS, DEBERÁN DOBLARSE CON UNA PENDIENTE MÁXIMA DE 1:6 RESPECTO DEL EJE DE LA VARILLA.

E. LOCALIZACIÓN DE EMPALMES


- EN ZAPATAS NO SON PERMITIDOS LOS EMPALMES.
- EN SOLERAS DE FUNDACIÓN LOS TRASLAPES SE PODRÁN REALIZAR EN CUALQUIER PUNTO DEL ELEMENTO, A EXCEPCIÓN DE LAS INTERSECCIONES ENTRE SOLERAS, O ENTRE SOLERAS Y COLUMNAS. NO TRASLAPAR MAS DEL 50% EN UNA MISMA SECCIÓN.
- EN PEDESTALES NO SE PERMITIRÁN EMPALMES.
- PARA TODOS LOS CASOS ANTERIORES DE EMPALME DEL ACERO DE REFUERZO DEBERÁ RESPETARSE EL CRITERIO DE EMPALMAR SOLAMENTE EL 50% DEL ÁREA (TOTAL O POR LECHO SEGÚN SEA APLICABLE) DE VARILLAS EN LA SECCIÓN A LA VEZ.
- LA DISTANCIA ENTRE SECCIONES DE TRASLAPE NUNCA SERÁ INFERIOR A LA LONGITUD DE DESARROLLO (L_d EN CUADRO DE VARILLAS) DE LA MAYOR DE LAS VARILLAS TRASLAPÁNDOSE.

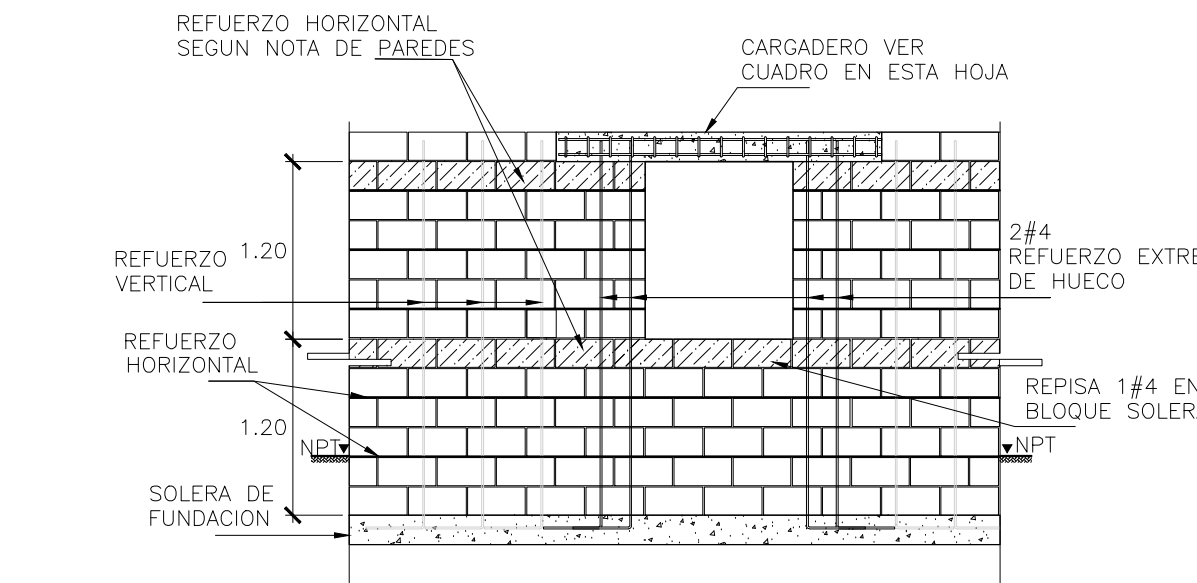

DETALLE TÍPICO DE SOLERAS INTERMEDIAS, CARGADEROS Y REPISAS SIN ESCALA

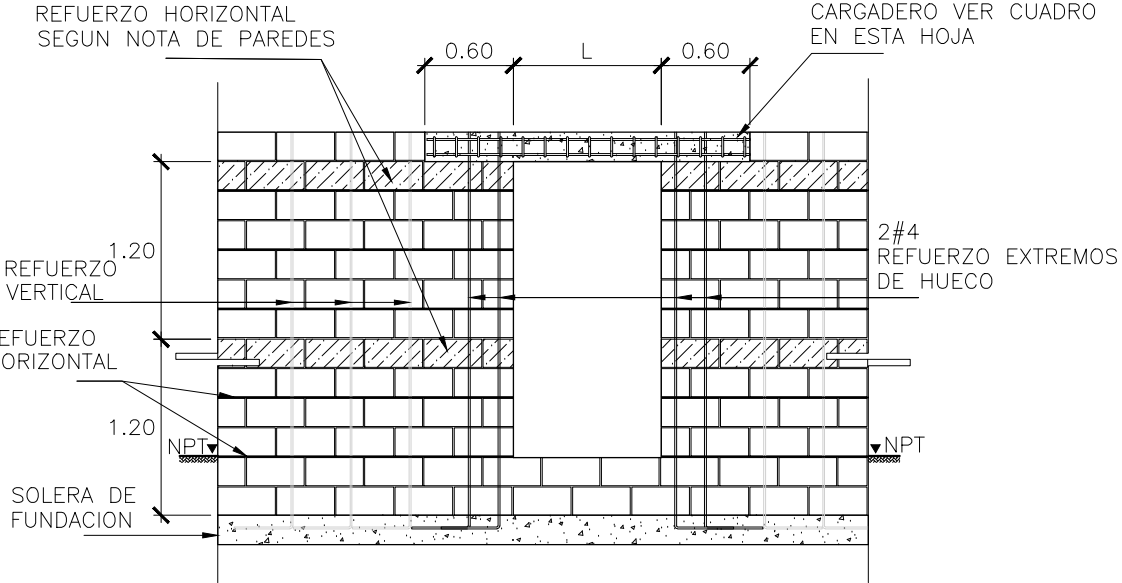

DETALLE TÍPICO DE SOLERAS INTERMEDIAS, CARGADEROS Y REPISAS SIN ESCALA

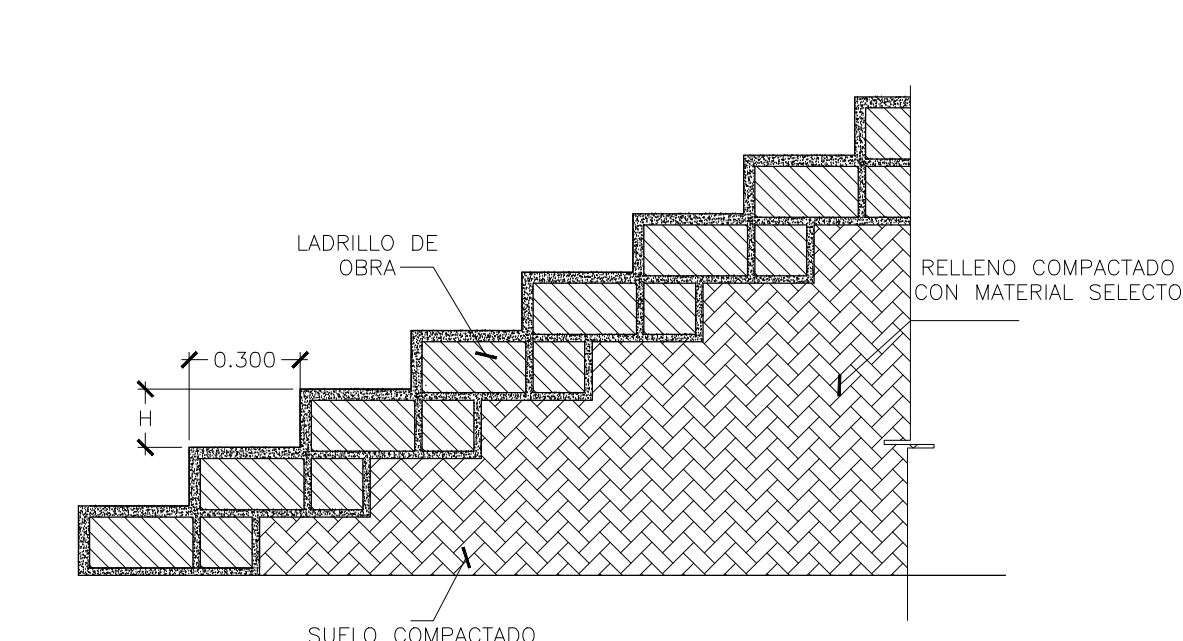

DETALLE TÍPICO DE GRADA FORJADA SIN ESCALA


F. ESTRUCTURA METALICA

- LOS POLINES SERÁN DE ACERO A36 O SIMILAR, CON $F_y=2530$ kg/cm^2 .
- LAS TUERCAS SERÁN HEXAGONALES TIPO PESADA DE ACUERDO A NORMA ASTM A325 GRADO C.
- TODOS LOS MIEMBROS METÁLICOS A BASE DE PERFILES METÁLICOS Y LOS POLINES DEBERÁN SER PROTEGIDOS CON DOS MANOS DE PINTURA ANTICORROSIVA, LAS QUE SE APLICARÁN EN DIFERENTES COLORES.
- LAS SOLDADURAS SERÁN DE ARCO METÁLICO Y LOS ELECTRODOS DEBERÁN CUMPLIR CON LA NORMA AWS A 5.1 O 5.5 Y SU DESIGNACIÓN SERÁ E-70XX, QUE PRODUCE METAL DE APORTACIÓN CON ESFUERZO MÍNIMO ESPECIFICADO DE FLUENCIA DE 3500 kg/cm^2 , Y DE RUPTURA EN TENSION DE 4200 kg/cm^2 . ESTE ELECTRODO ES COMPATIBLE CON EL ACERO A-36.
- EN LA TABLA 2 SE MUESTRAN LOS SÍMBOLOS BÁSICOS UTILIZADOS EN LA SOLDADURA.


TABLA 2									
SÍMBOLOS BÁSICOS DE SOLDADURA									
POSTERIOR	FILLETE	TAPON O RANURA	CUADRADOS	Y	BISEL	U	J	ENSANCHAMIENTO DE BESEL	ENSANCHAMIENTO DE BESEL
SÍMBOLOS COMPLEMENTARIOS									
RESPALDO	ESPACIO	SOLDADURA TODO ALREDEDOR	SOLDADURA DE CAMPO	CONTORNO		NIVELADO		CONVEXO	VEASE LA TABLA A.2.4-79 PARA LOS SÍMBOLOS COMPLEMENTARIOS DE LA SOLDADURA
LOCALIZACIÓN ESTÁNDAR DE LOS ELEMENTOS DE UN SÍMBOLO DE SOLDADURA									

G. FUNDACIONES


PARA EL DISEÑO DE LAS CIMENTACIONES SE HA CONSIDERADO UN SUELO CON CAPACIDAD DE CARGA DE 15 ton/m^2 . LO CUAL DEBERÁ DE GARANTIZARSE EN LA OBRA.

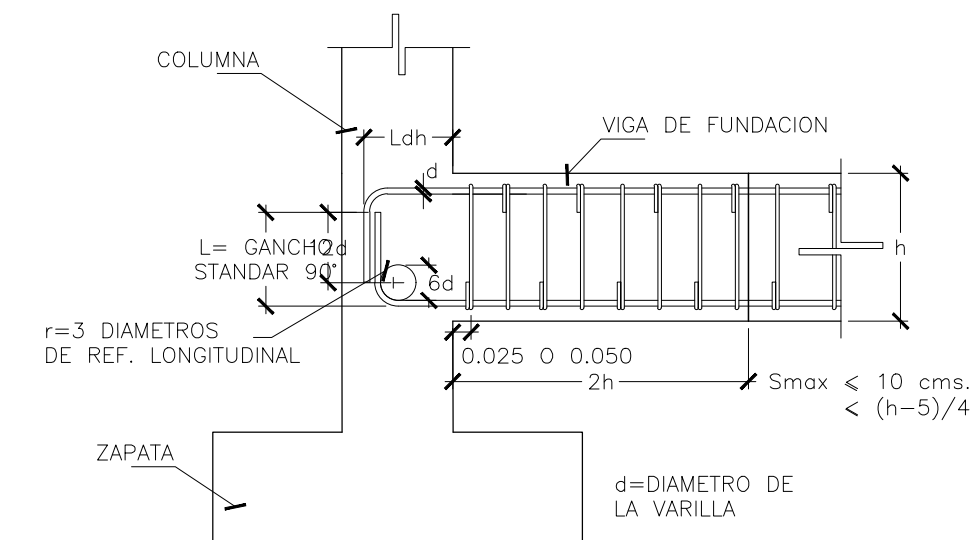


ANCLAJE FUNDACION EN COLUMNAS ESC. 1:20

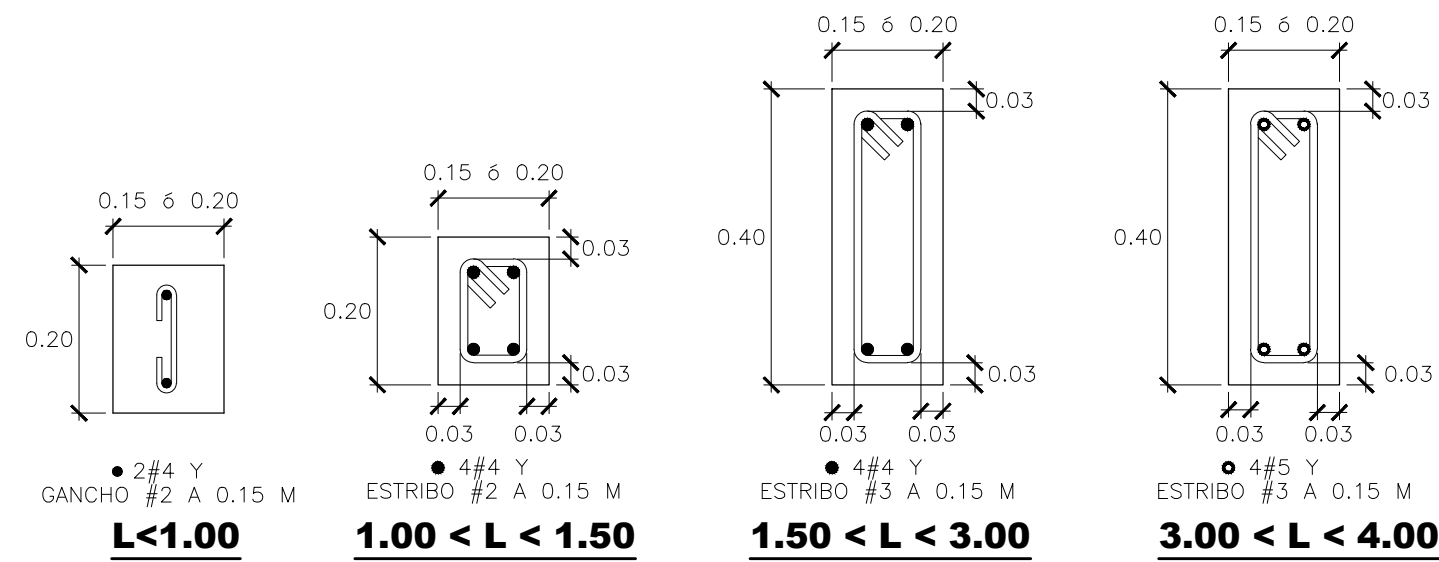


DETALLES DE CARGADEROS ESC. 1:10

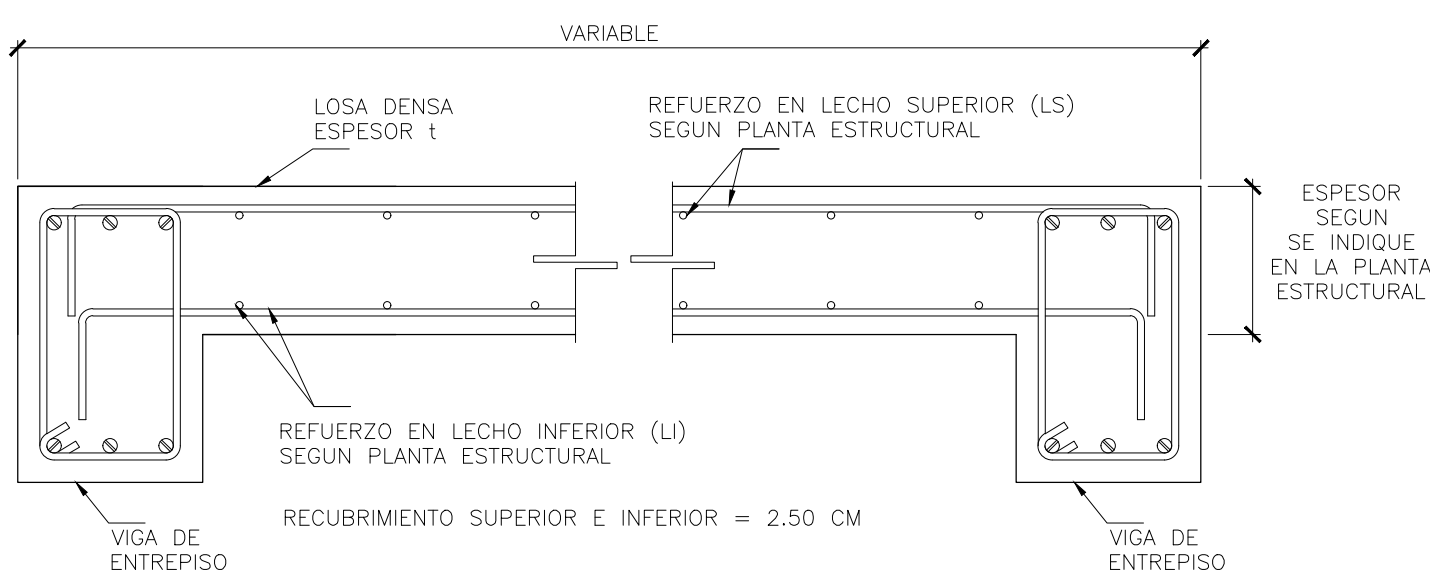


SECCION TÍPICA DE LOSA Densa ESC. 1:10

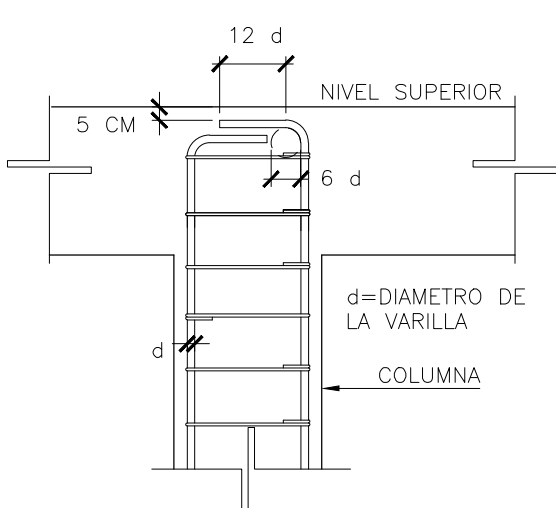

DETALLE DE REMATE EN COLUMNA ESC. 1:10

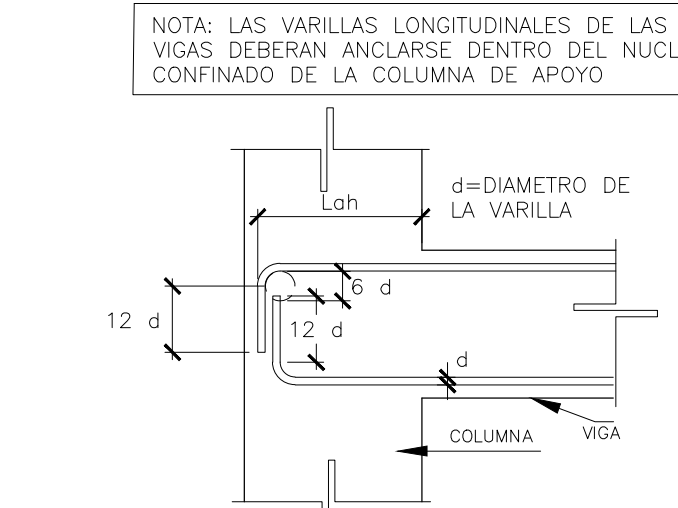


ANCLAJE DE VIGA A COLUMNAS ESC. 1:10

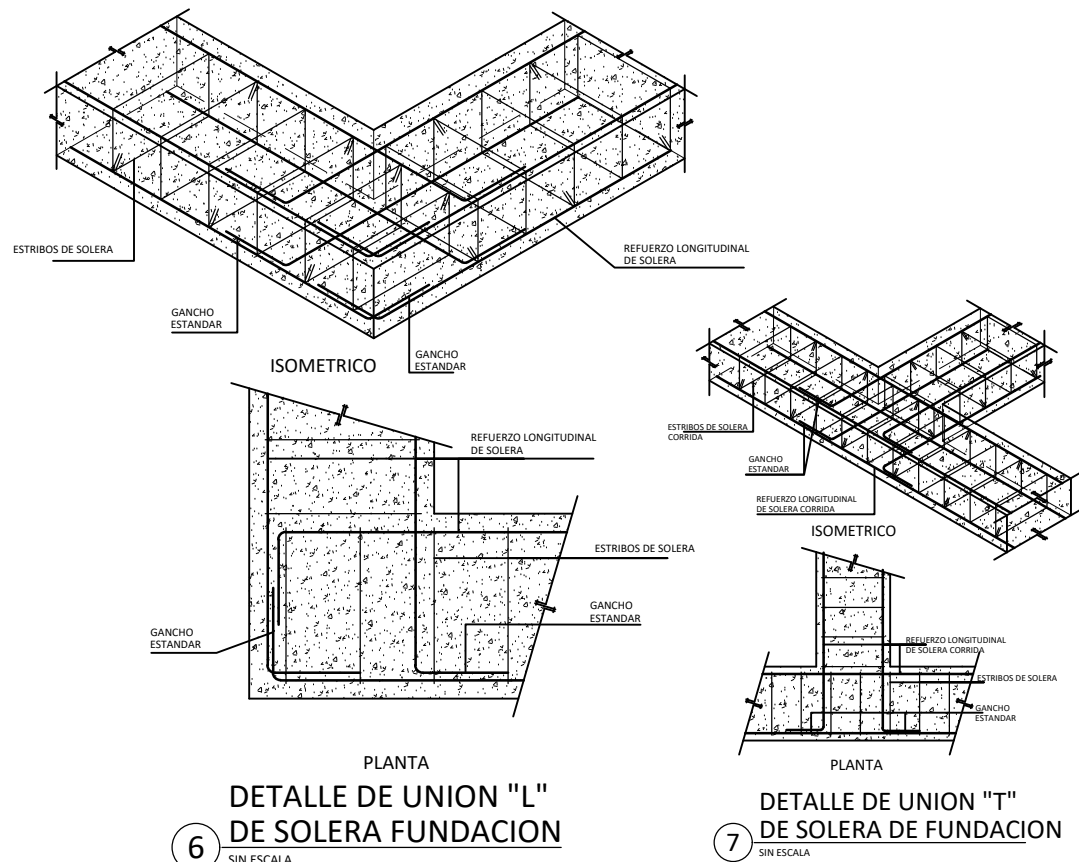

DETALLE DE UNION "L" DE SOLERA FUNDACION SIN ESCALA

DETALLE DE UNION "T" DE SOLERA DE FUNDACION SIN ESCALA

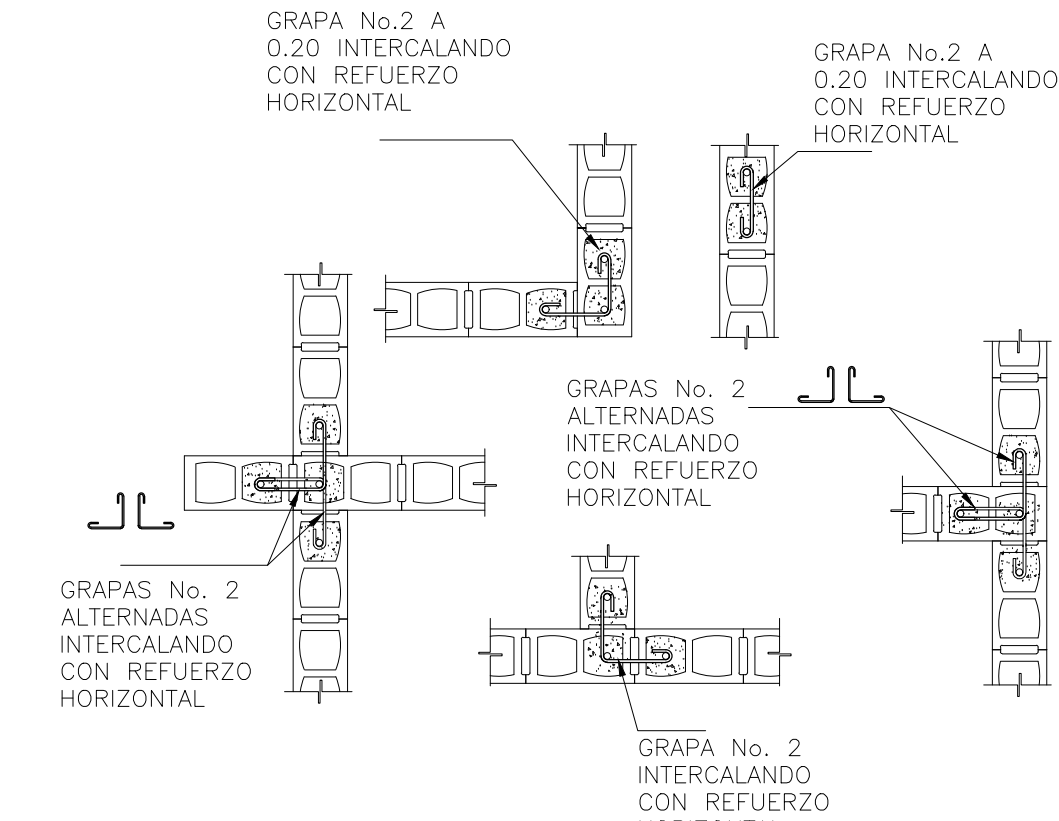

DETALLE DE UNIONES ENTRE PAREDES DE BLOQUE SIN ESCALA



SELLOS DE APROBACION:

ESTE PLANO FORMA PARTE INTEGRAL DE LA RESOLUCION EMITIDA EN FECHA 24 DE JULIO DE 2025 EN FORMATO DIGITAL Y CORRESPONDE AL EXPEDIENTE DE PERMISO DE CONSTRUCCION REFERENCIA 0333-2025. PRESENTADO BAJO LA RESPONSABILIDAD DE LA ARQ. MORENA GUADALUPE VASQUEZ LOPEZ CON REGISTRO PROFESIONAL VMVDU A-4576.

PRESENTA:



Tel. 7526-1553
asismica@gmail.com

PROYECTO
CONSTRUCCION DE VIVIENDA DE DOS NIVELES
Y TERRAZA EMPRESA AZZUL
PROPIETARIOS
EMPRESA AZZUL S.A DE C.V

UBICACION:
CANTON SAN RAFAEL, CONDOMINIO RECREATIVOS LOMAS DE SAN BLASS, CALLE MAJAHUAL, POLIGONO 6, NIVEL 1, NUMERO 18, DEPARTAMENTO DE LA LIBERTAD.

CONTENIDO:

NOTAS TECNICAS Y DETALLES ESTRUCTURALES


ESCALA:
INDICADA

FECHA:
MARZO DE 2025


HOJA N°:
E-01

FIRMA Y SELLO DE PROFESIONALES RESPONSABLES


DISEÑO ARQUITECTÓNICO: FIRMA:	DIRECTOR DE LA OBRA: FIRMA:	RESPONSABLE DEL TRAMITE: FIRMA:
DISEÑO ARQUITECTÓNICO: SELLO:	DIRECTOR DE LA OBRA: SELLO:	RESPONSABLE DEL TRAMITE: SELLO:

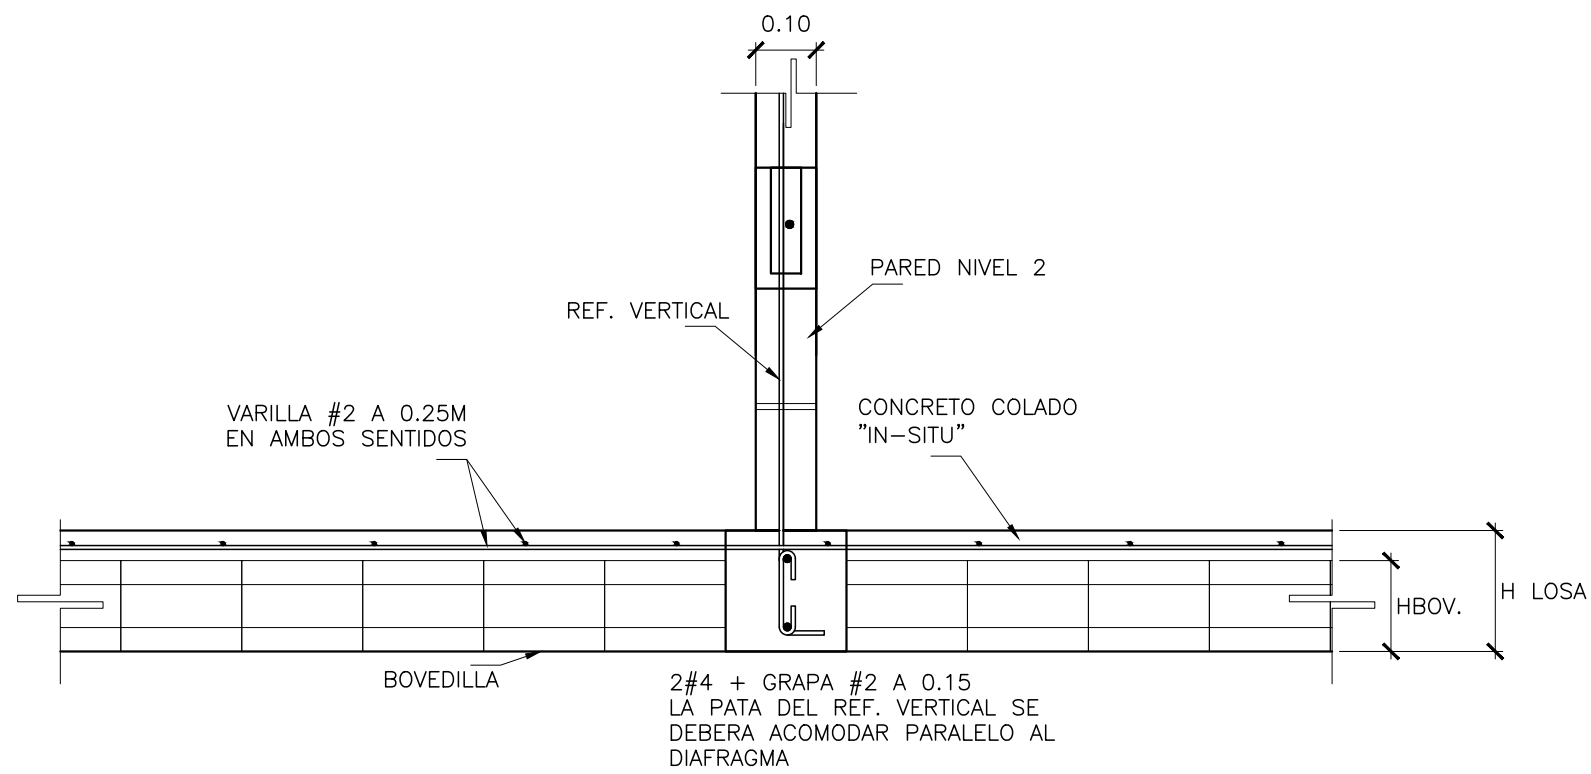


APOYO DE PARED SOBRE LOSA - PARED PERPENDICULAR A VIGUETA
ESC. 1:12.5

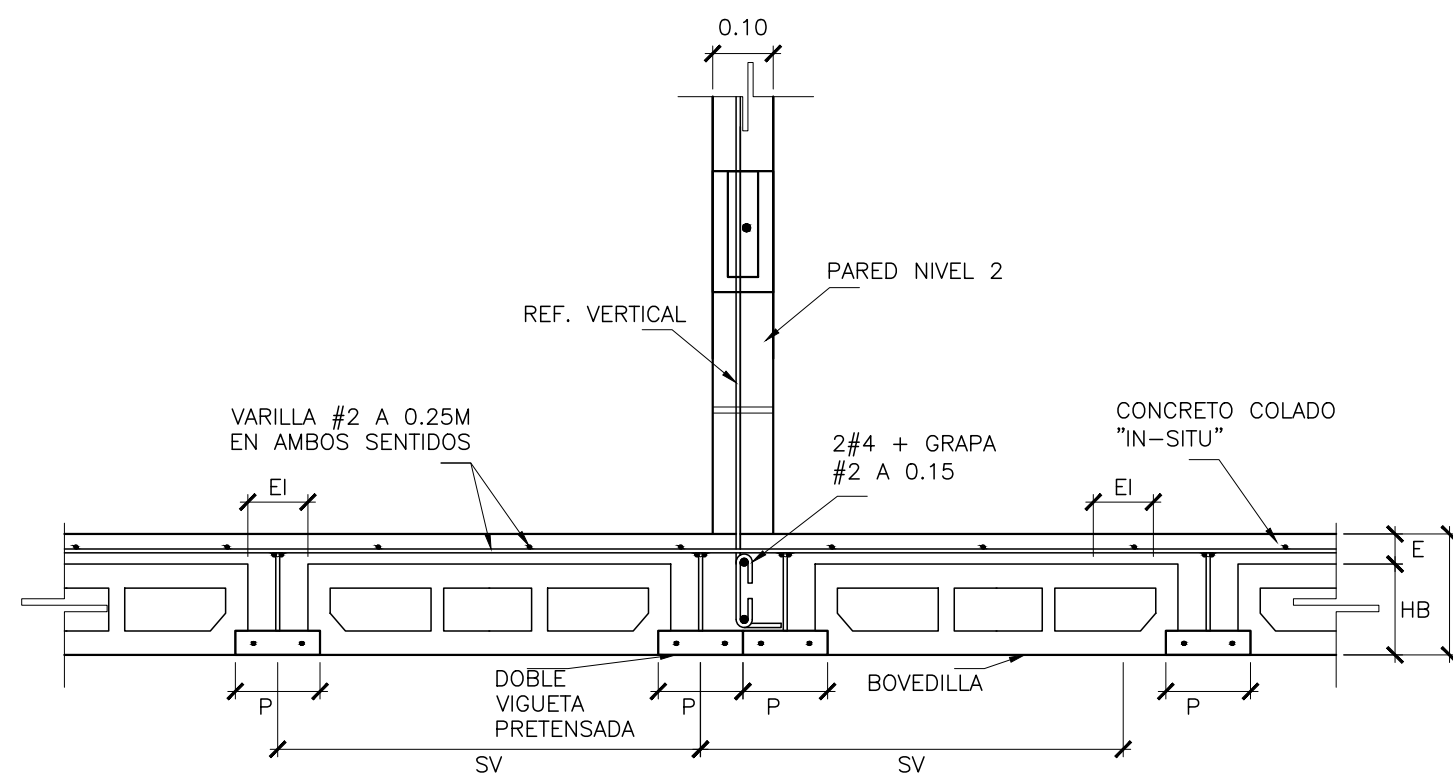

APOYO DE PARED SOBRE LOSA - PARED PARALELA A VIGUETA
ESC. 1:12.5

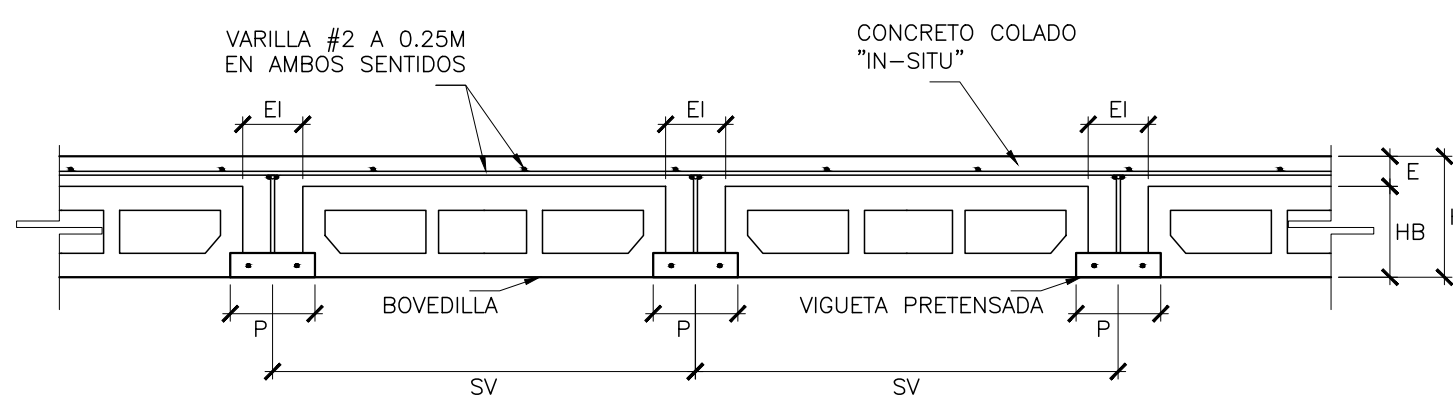


CORTE SECCION TRANSVERSAL DE LOSA
ESC. 1:12.5

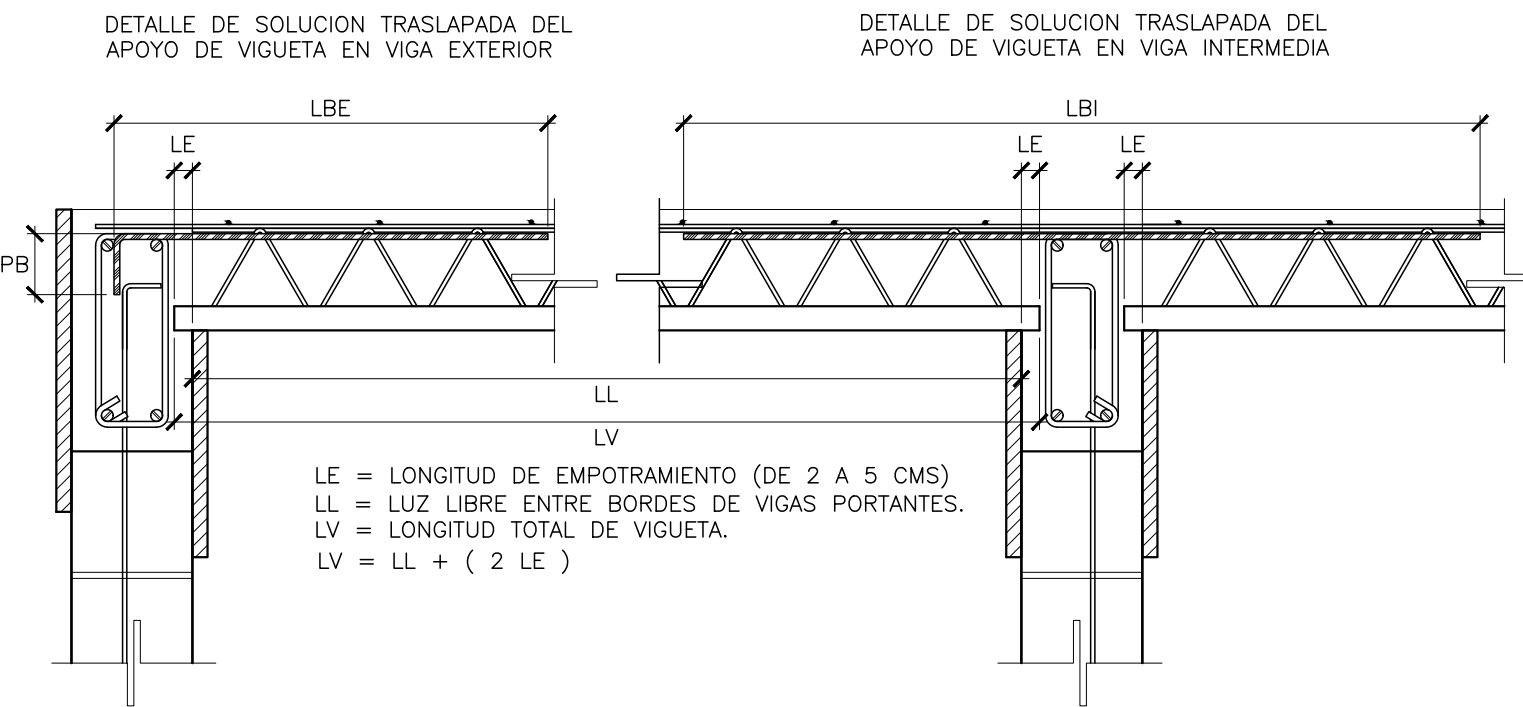


BASTONEADO EN EXTREMO DE VIGUETAS
ESC. 1:12.5

CUADRO DE BASTONES DE LOSAS	
VIGUETA	VT1-20
LBE	85
LBI	150
PB	15
No. VAR.	2#4/VIG


CUADRO DE LOSAS						
VIGUETA	HE	HB	E	SV	EI	P
VT1-20	20	15	5	70	5	14

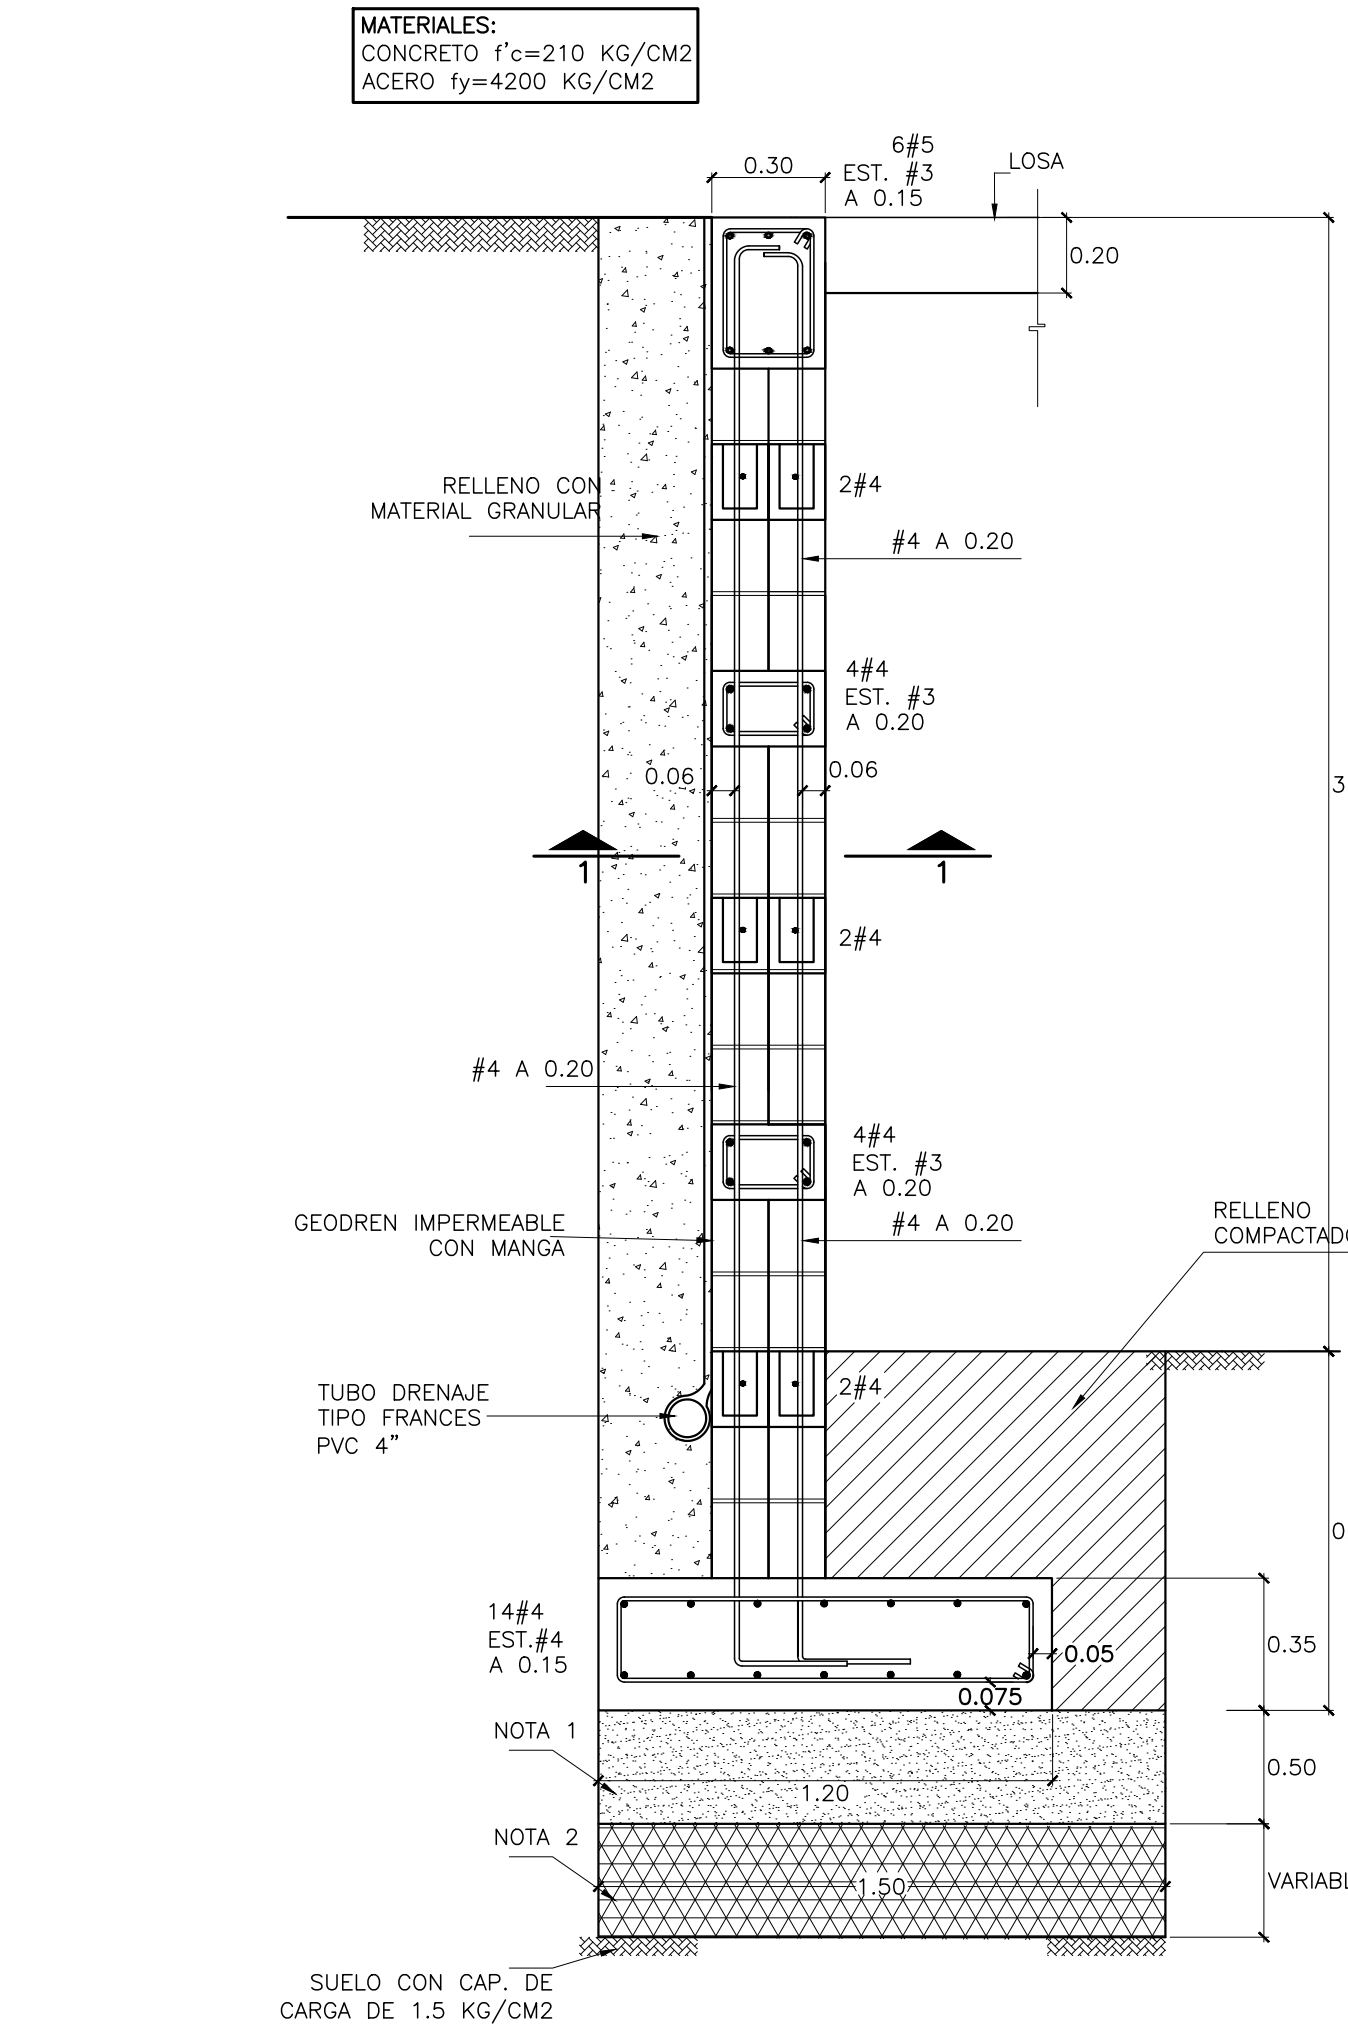

MURO MB-1
ESC. 1:12.5

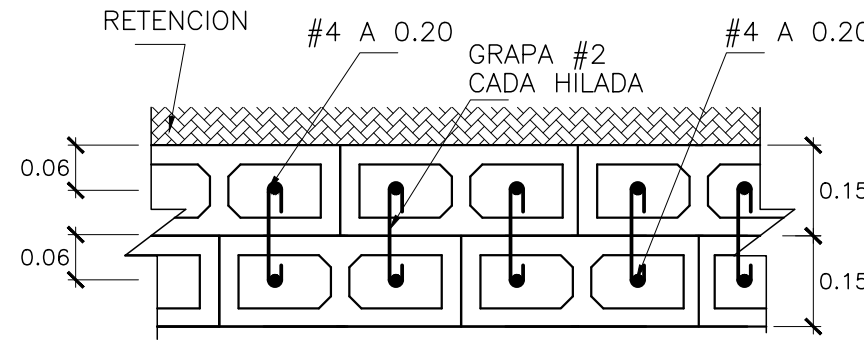


SECCION 1-1
ESC. 1:12.5

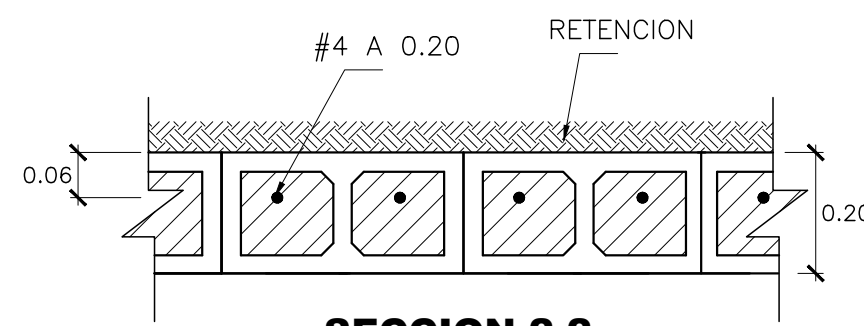


SECCION 2-2
ESC. 1:12.5

NOTA 1
COMPACTACION CON SUELO-CEMENTO. SE RECOMIENDA EL EMPLEO DE ARENAS LIMOSAS (TIERRA BLANCA) MEZCLADO CON CEMENTO EN UNA PROPORCION 20:1. LA MEZCLA DEBERA COMPACTARSE POR MEDIOS MECANICOS AL 90% DE SU DENSIDAD SECA MAXIMA DE CONFORMIDAD CON LA NORMA ASTM D-558


NOTA 2
SE DEBERA RESTITUIR EL SUELO SOBREEXCAVANDO HASTA LA PROFUNDIDAD DE SUELOS INADECUADOS INDICADOS EN EL ESTUDIO DE SUELOS, DE ACUERDO A CADA SONDEO. LA RESTITUCION SE HARA CON LIMOS ARENOSOS O ARENO LIMOSOS, DEL TIPO TIERRA BLANCA O BIEN POR SUELOS PROPIOS DEL LUGAR, PREVIA APROBACION POR PARTE DEL LABORATORIO DE SUELOS. LA COMPACTACION SE HARA AL 90% DEL PESO VOLUMETRIC SECOS MAXIMO, OBTENIDO A TRAVES DEL ENSAYO PROCTOR (PROCTOR MODIFICADO, NORMA ASTM D 1557-92)

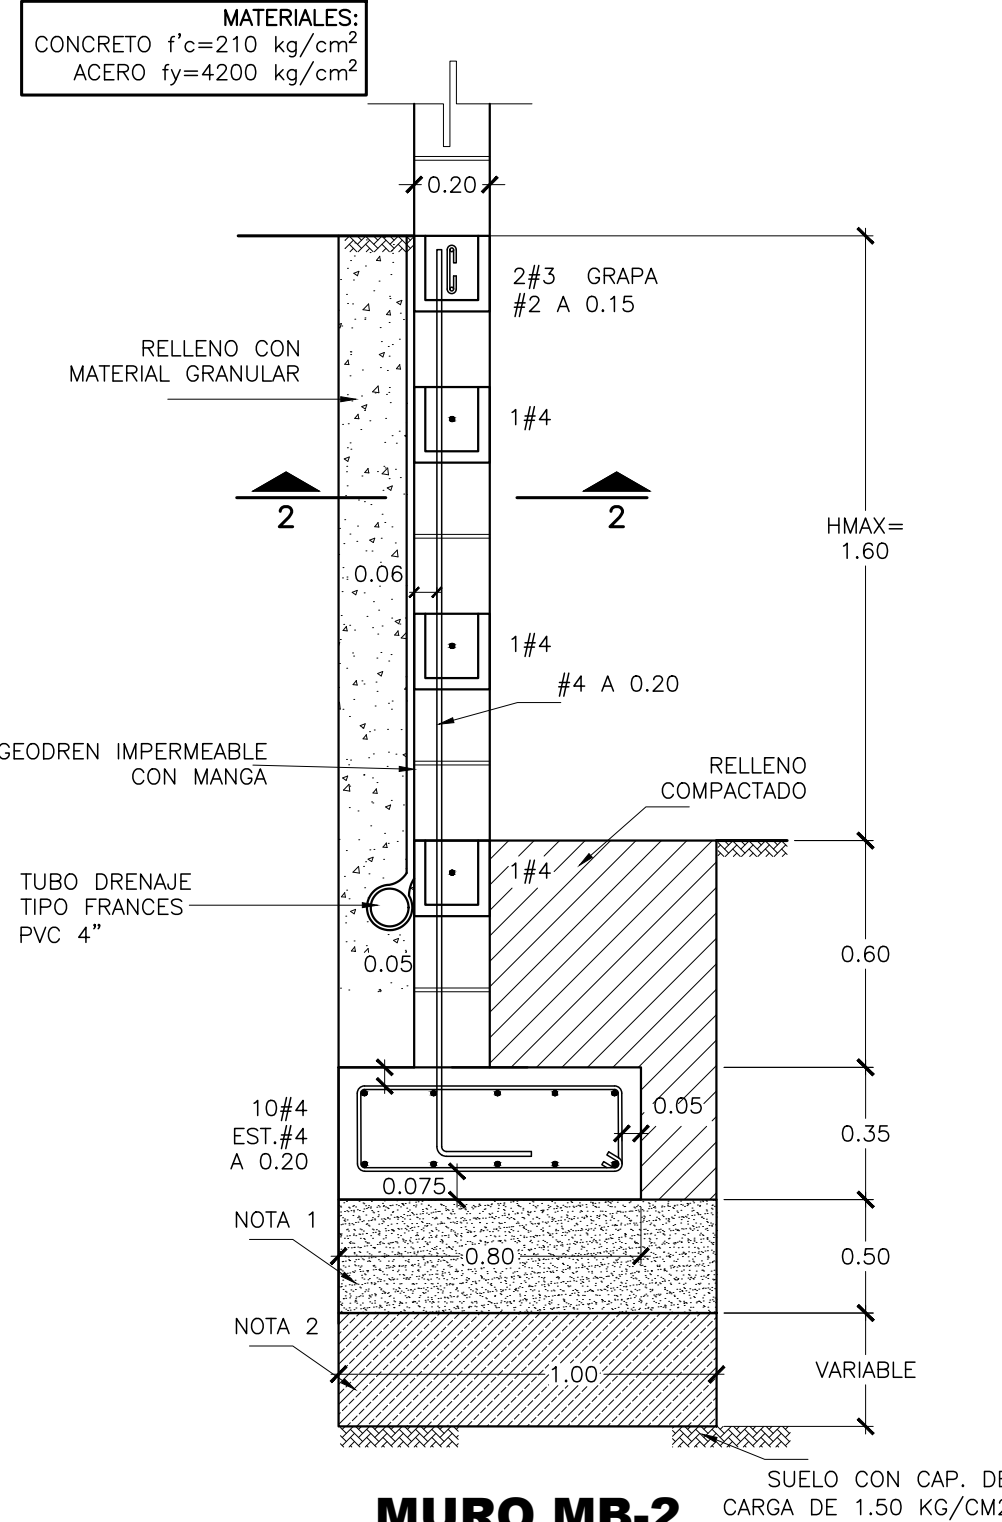


MURO MB-2
ESC. 1:20

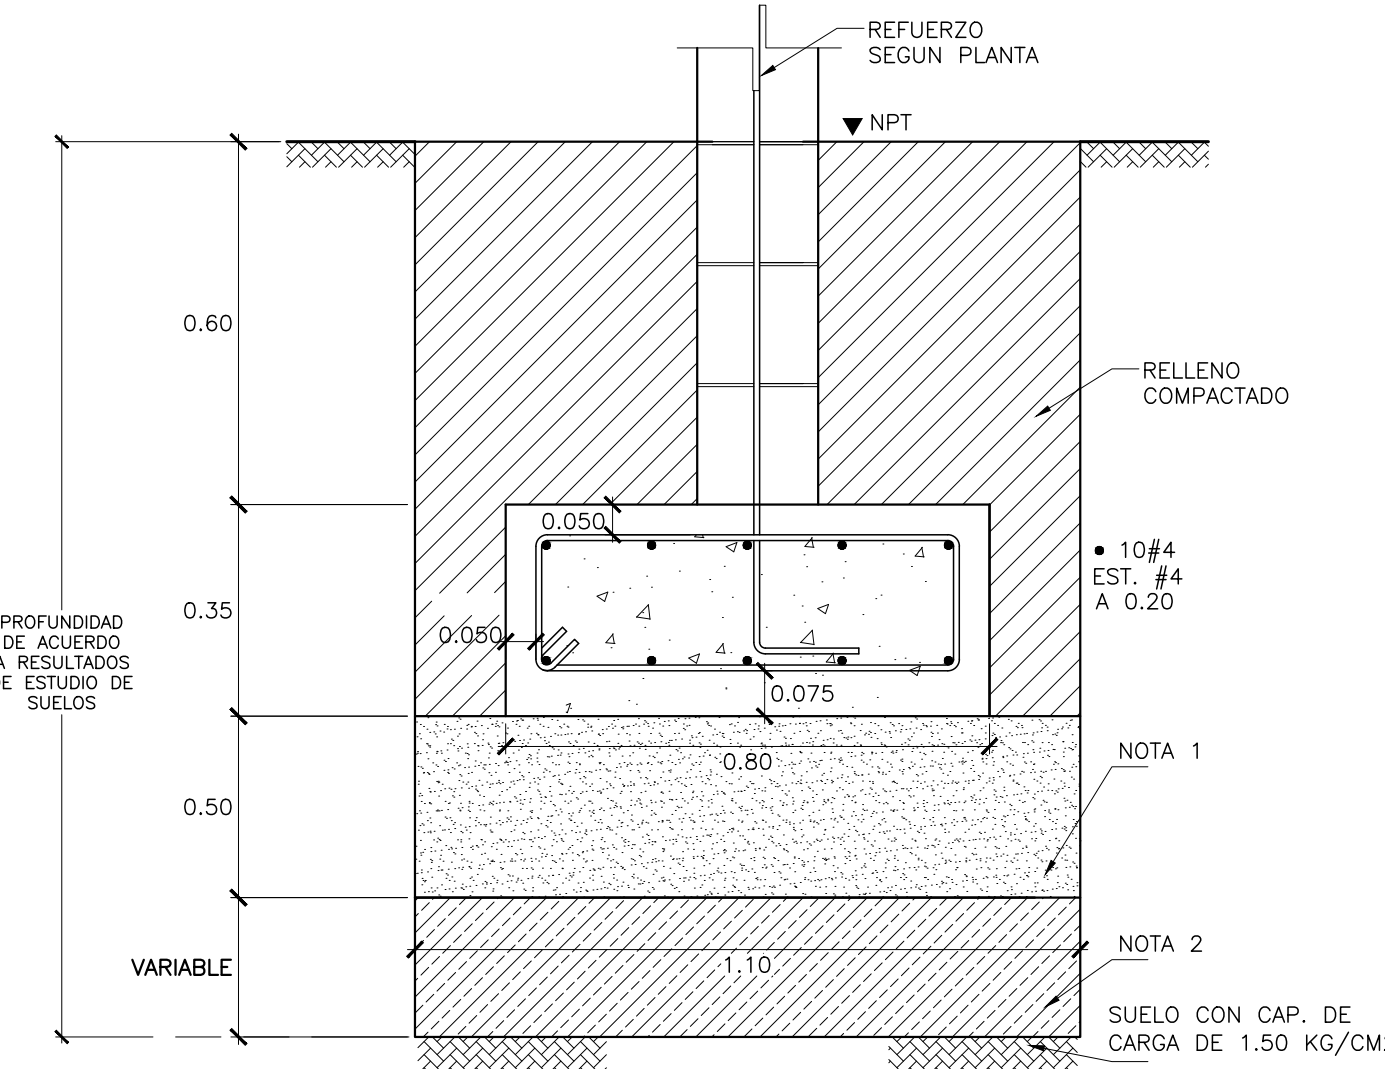


DETALLE SF-1
ESC. 1:12.5

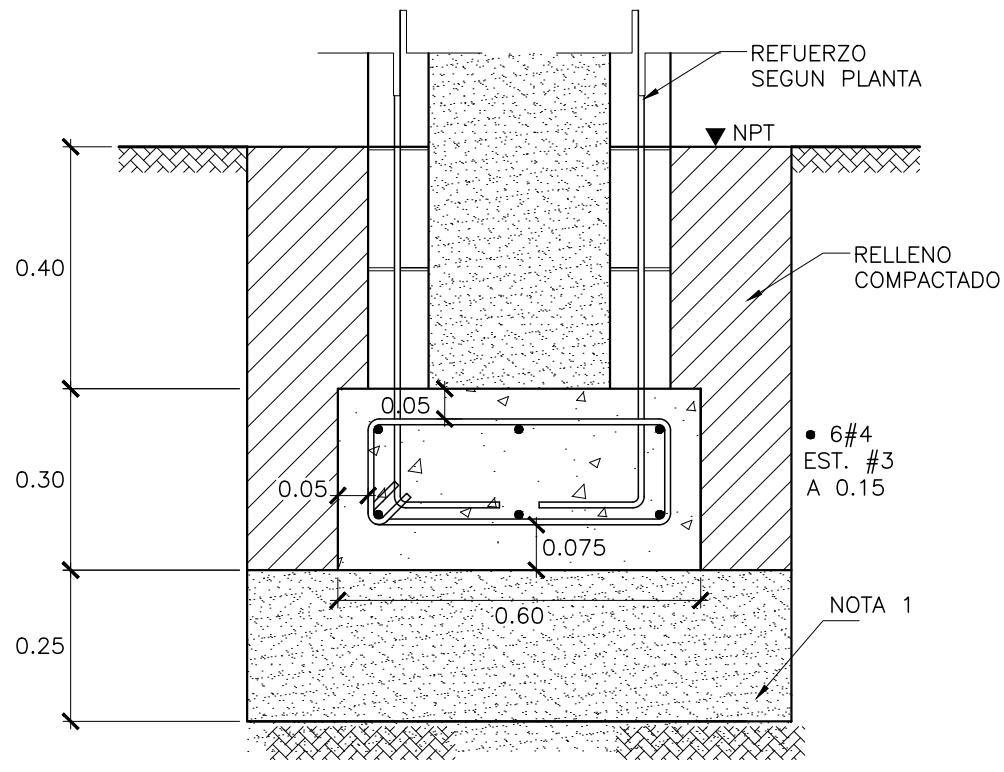

DETALLE SF-2
JARDINERA ESC. 1:12.5

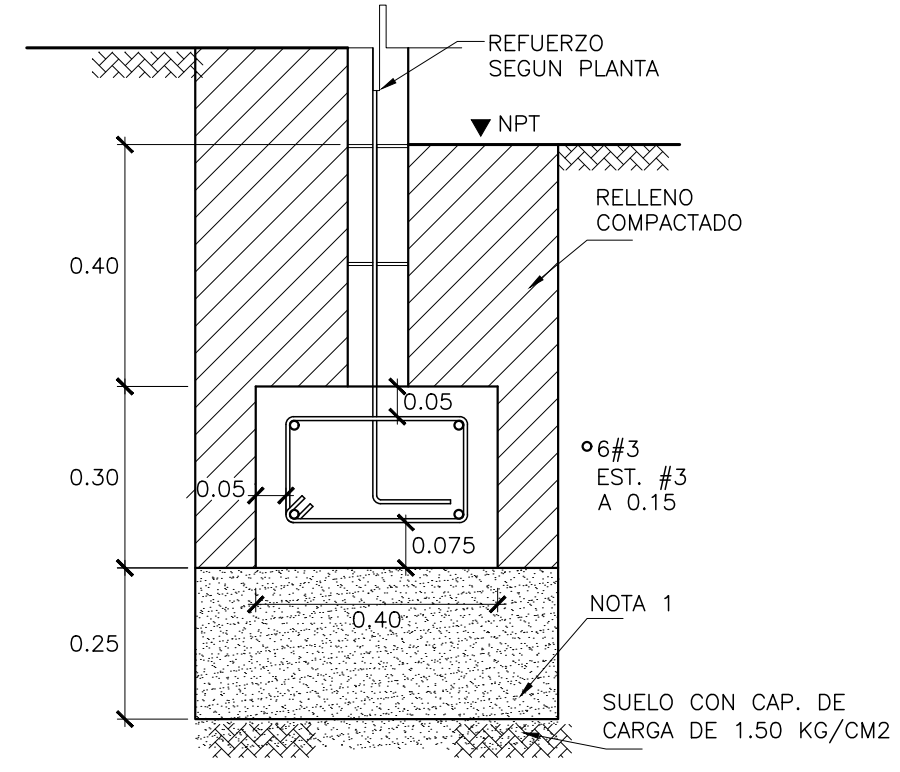

DETALLE SF-3
JARDINERA ESC. 1:12.5

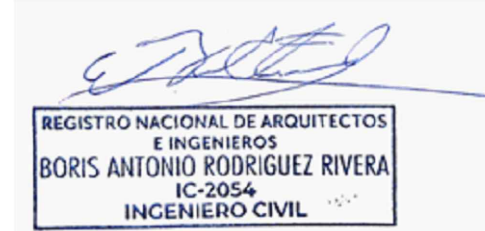

SELLOS DE APROBACION:

ESTE PLANO FORMA PARTE INTEGRAL DE LA RESOLUCION EMITIDA EN FECHA 24 DE JULIO DE 2025 EN FORMATO DIGITAL Y CORRESPONDE AL EXPEDIENTE DE PERMISO DE CONSTRUCCION REFERENCIA 0333-2025. PRESENTADO BAJO LA RESPONSABILIDAD DE LA ARQ. MORENA GUADALUPE VASQUEZ LOPEZ CON REGISTRO PROFESIONAL VMVDU A-4576.

PRESENTA:



Tel. 7526-1553
asismica@gmail.com

PROYECTO
SAN BLASS AZZUL, LOTE 18

PROPIETARIOS
AZZUL INVERSIONES SA DE CV


UBICACION:
CANTON SAN RAFAEL, CONDOMINIOS RECREATIVOS LOMAS DE SAN BLASS, CALLE MAJAHUAL, POLIGONO 6, NIVEL 1, NUMERO 18, DEPARTAMENTO DE LA LIBERTAD.

CONTENIDO:


NOTAS TECNICAS Y DETALLES ESTRUCTURALES

ESCALA: INDICADA	AREA TOTAL DEL TERRENO: 384.76 M2 AREA TOTAL DE CONSTRUCCION: 458.61 M2	FECHA: MARZO 2025	HOJA N°: E-02
---------------------	--	----------------------	------------------

FIRMA Y SELLO DE PROFESIONALES RESPONSABLES		
DISEÑO ARQUITECTÓNICO: FIRMA: 	DIRECTOR DE LA OBRA: FIRMA: 	RESPONSABLE DEL TRAMITE: FIRMA:
DISEÑO ARQUITECTÓNICO: SELLO: REGISTRO NACIONAL DE ARQUITECTOS E INGENIEROS CARLA PATRICIA RODRIGUEZ DE CHOCOBAR A-2339 ARQUITECTA	DIRECTOR DE LA OBRA: SELLO: REGISTRO NACIONAL DE ARQUITECTOS E INGENIEROS CARLOS FRANCISCO CALICA MAZA A-3297 ARQUITECTO	RESPONSABLE DEL TRAMITE: SELLO: REGISTRO NACIONAL DE ARQUITECTOS E INGENIEROS Morena Guadalupe Vasquez Lopez A-4576 ARQUITECTA

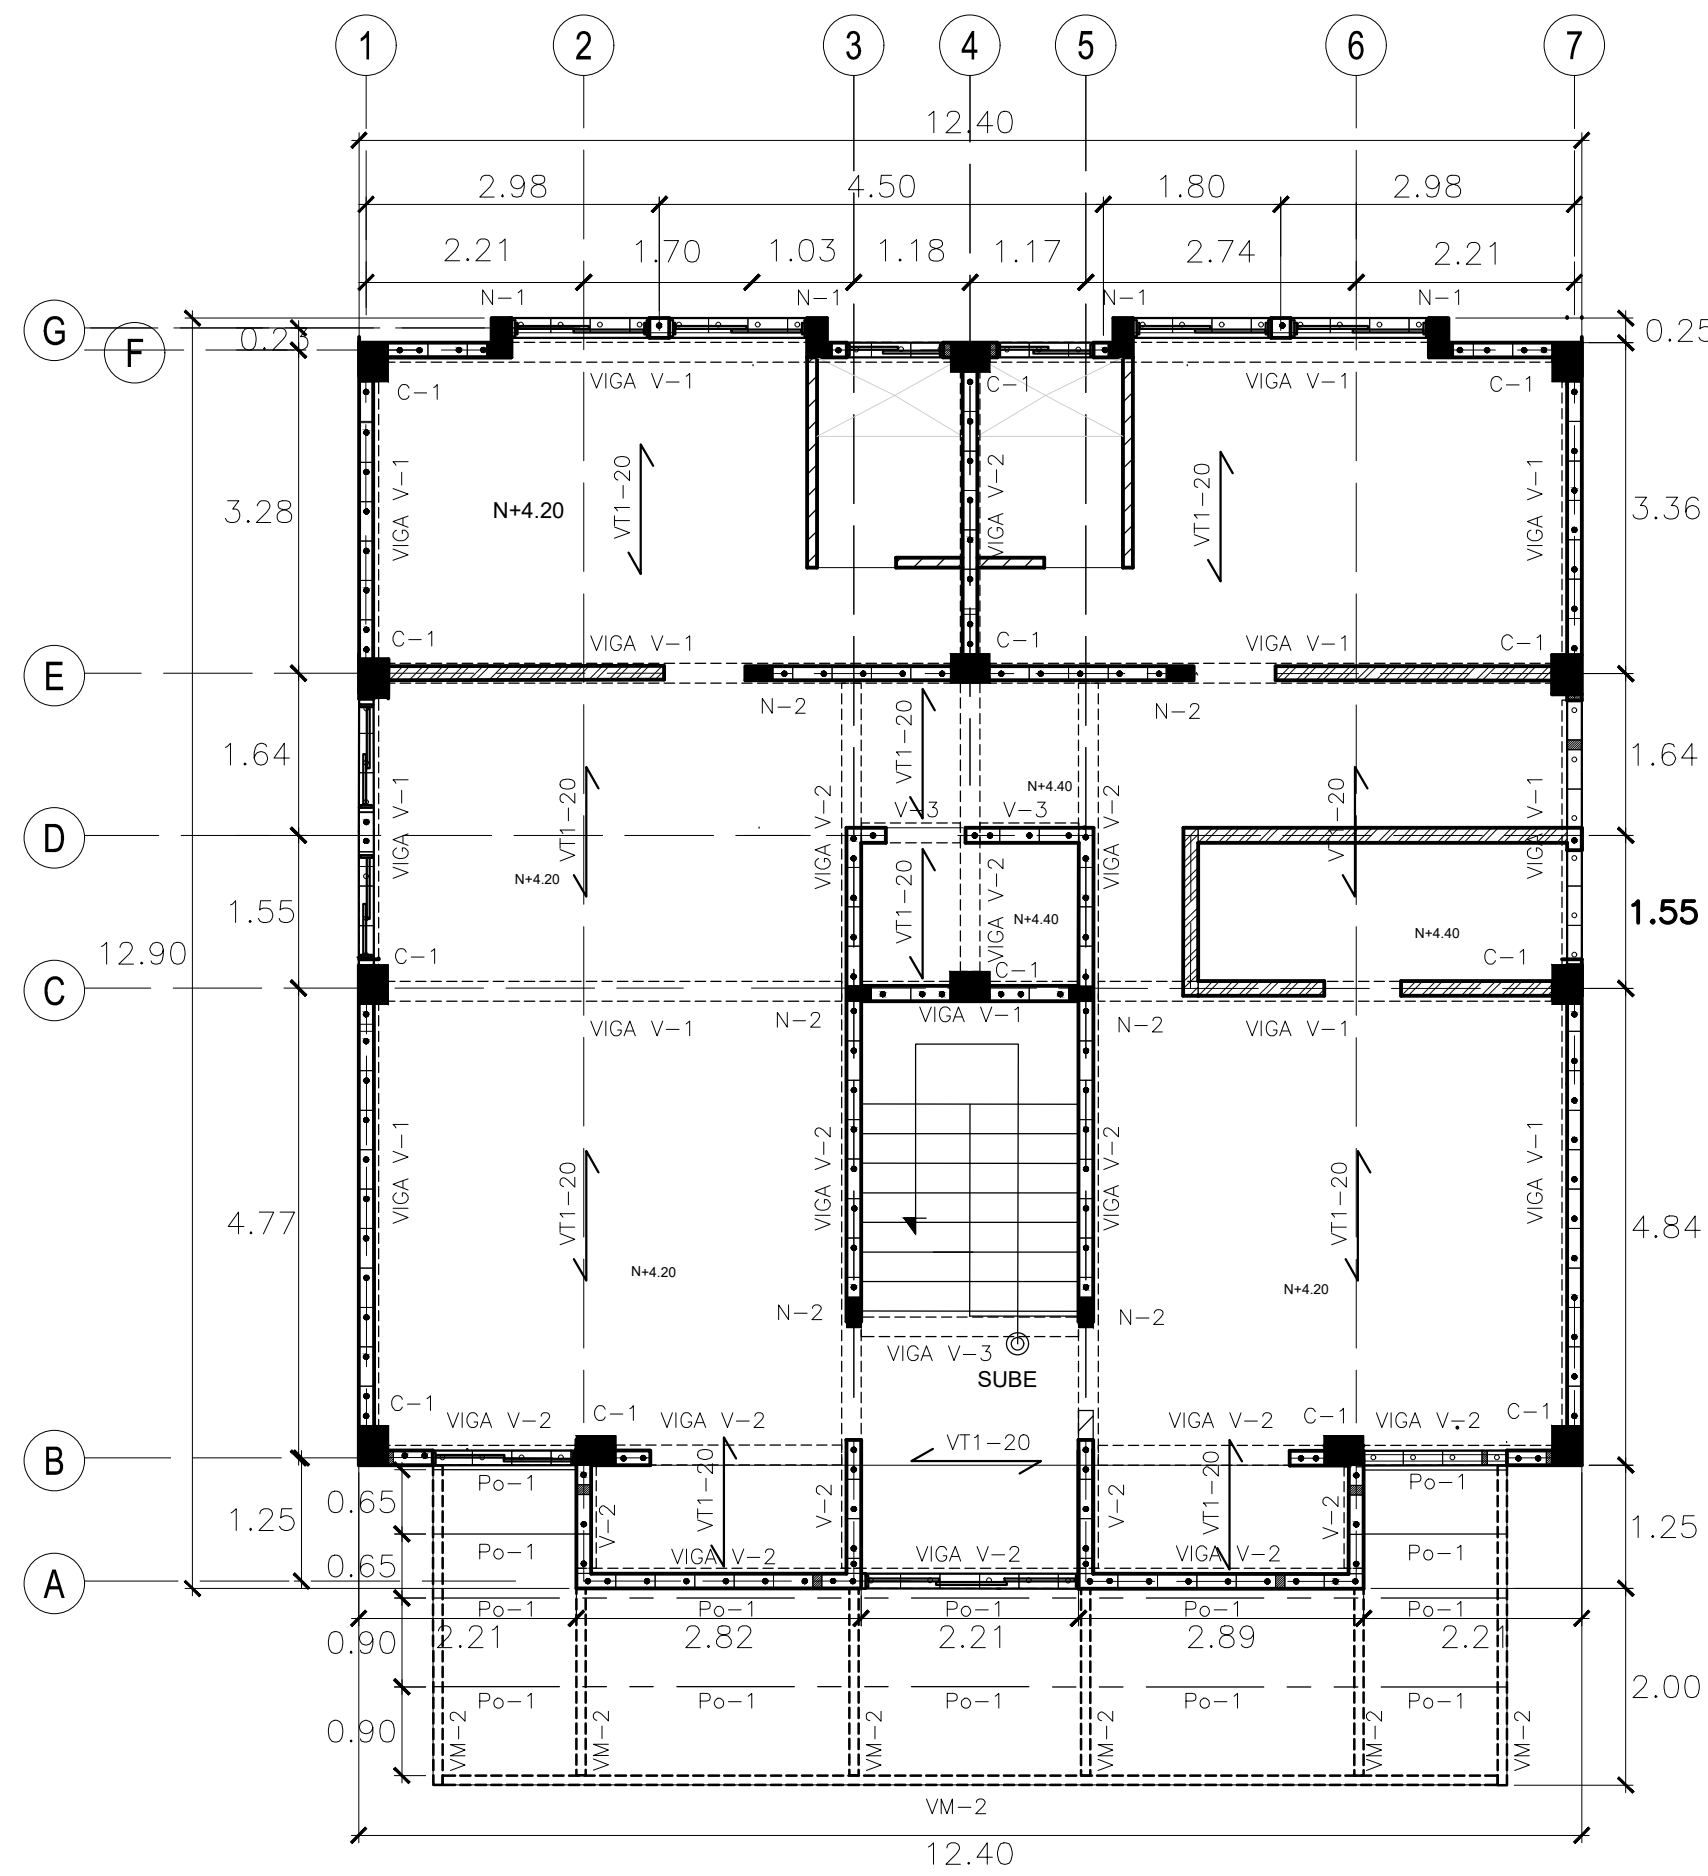

PLANTA DE ENTREPISOS SEGUNDO NIVEL
ESC. 1:75

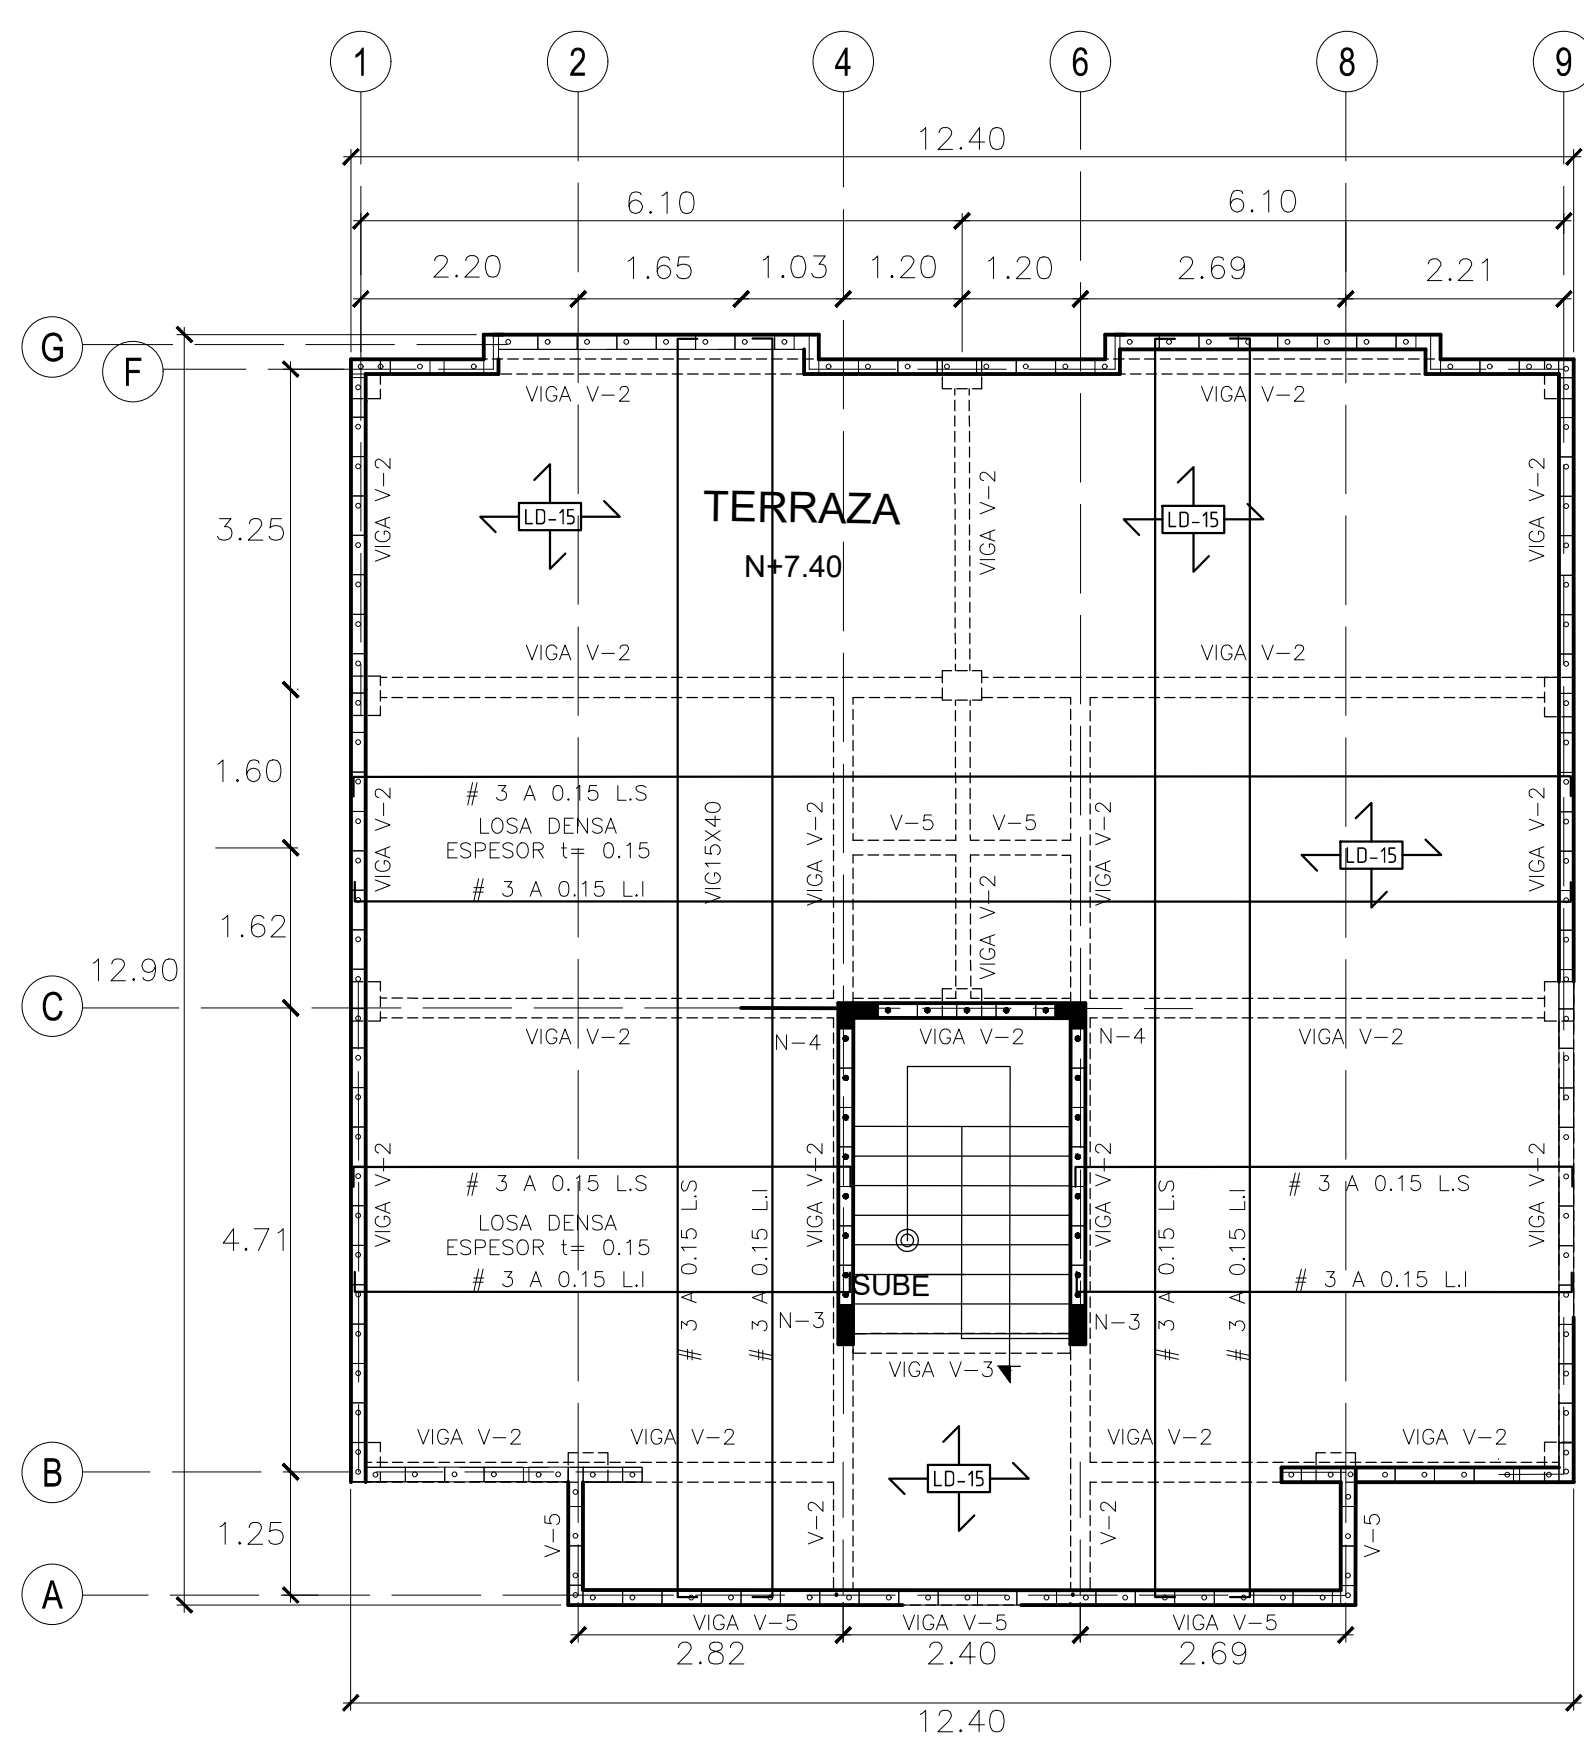


PLANTA DE ENTREPISOS TERRAZA NIVEL
ESC. 1:75




SELLOS DE APROBACION:

ESTE PLANO FORMA PARTE INTEGRAL DE LA RESOLUCION EMITIDA EN FECHA 24 DE JULIO DE 2025 EN FORMATO DIGITAL Y CORRESPONDE AL EXPEDIENTE DE PERMISO DE CONSTRUCCION REFERENCIA 0333-2025. PRESENTADO BAJO LA RESPONSABILIDAD DE LA ARQ. MORENA GUADALUPE VASQUEZ LOPEZ CON REGISTRO PROFESIONAL VMVDU A-4576.

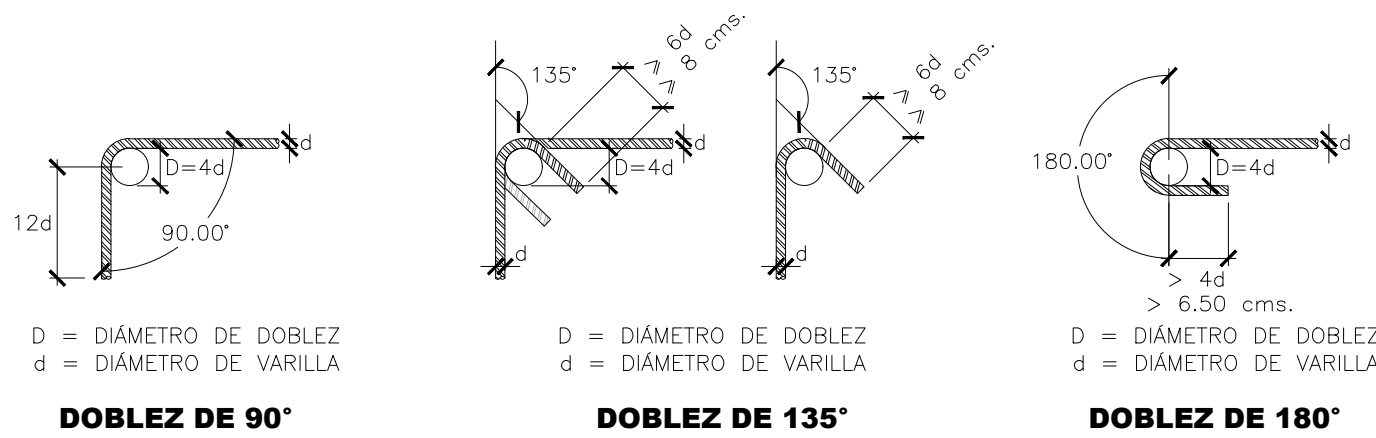


DETALLES DE DOBLECES DE REFUERZO
EN ESTRIBOS (VARILLAS MENORES AL #5)
SIN ESCALA

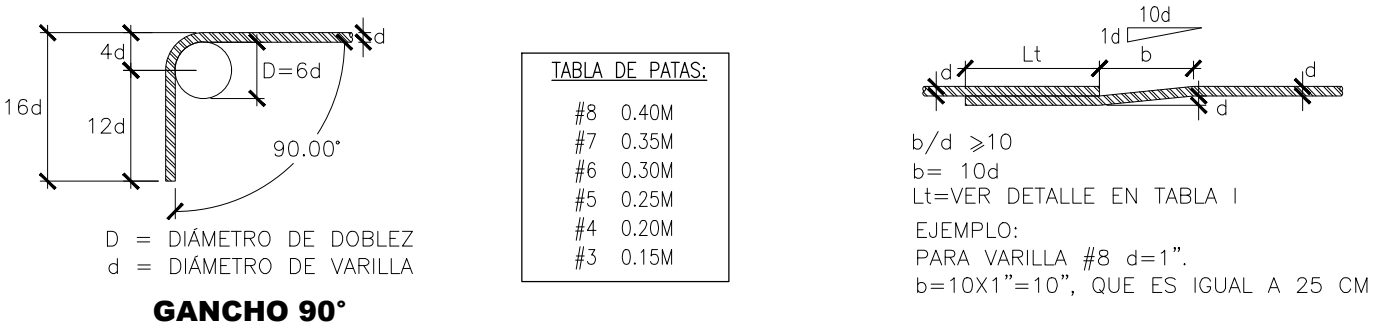


DETALLES DE DOBLEZ
DE REFUERZO PRINCIPAL
SIN ESCALA


DETALLE DE TRASLAPE
EN VIGAS Y COLUMNAS
SIN ESCALA

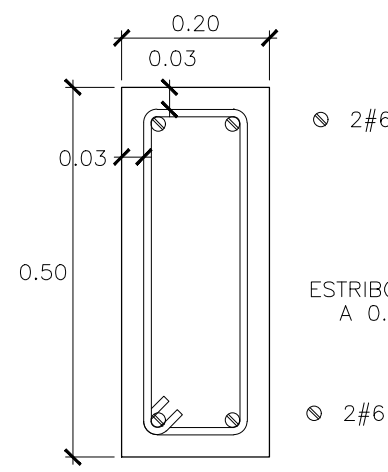


VIGA V-1
ESC. 1:10

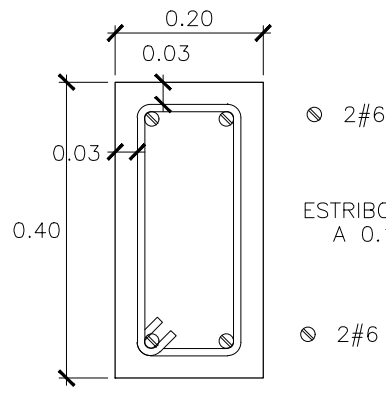


VIGA V-2
ESC. 1:10

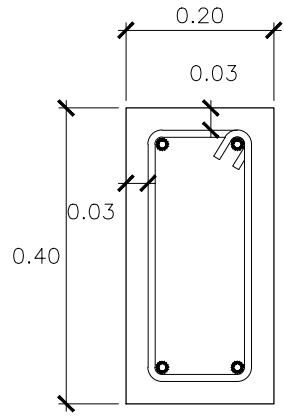


VIGA V-3
ESC. 1:10

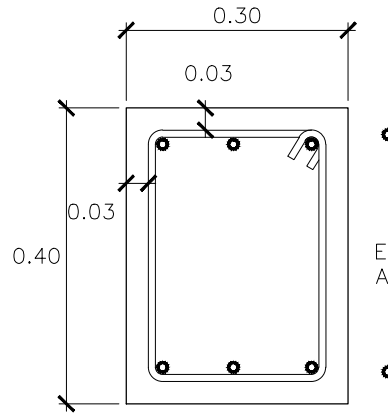


VIGA V-4
ESC. 1:10

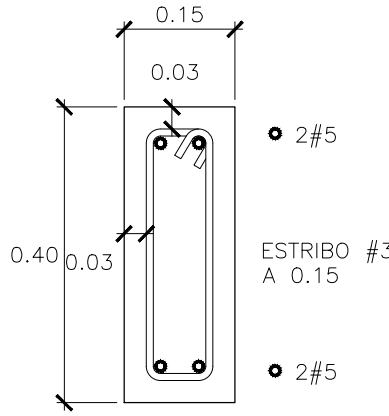


VIGA V-5
ESC. 1:10

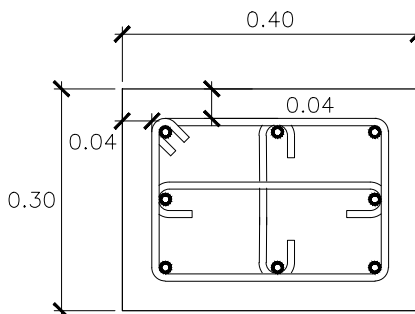


COLUMNA C-1
ESC. 1:10

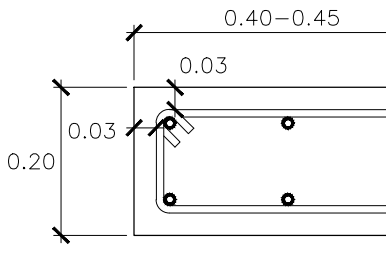


NERVIO N-1
ESC. 1:10

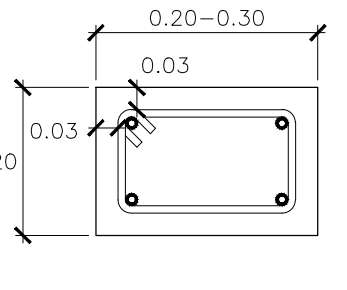

NERVIO N-2
ESC. 1:10

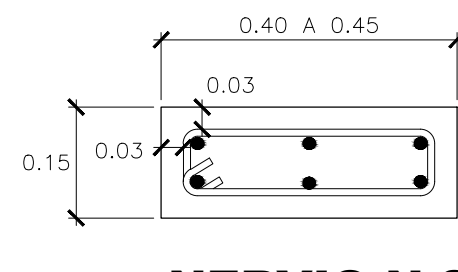

NERVIO N-3
ESC. 1:10

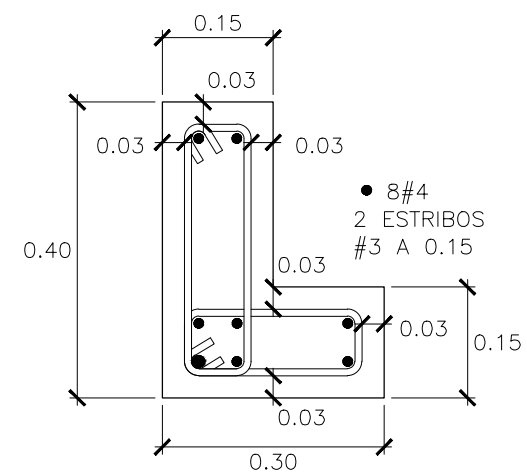

NERVIO N-4
ESC. 1:10

PRESENTA:



Tel. 7526-1553
asismica@gmail.com

PROYECTO
CONSTRUCCION DE VIVIENDA DE DOS NIVELES
Y TERRAZA EMPRESA AZZUL
PROPIETARIOS
EMPRESA AZZUL S.A DE C.V

UBICACION:
CANTON SAN RAFAEL, CONDOMINIOS RECREATIVOS LOMAS DE SAN BLASS, CALLE
MAJAHUAL, POLIGONO 6, NIVEL 1, NUMERO 18, DEPARTAMENTO DE LA LIBERTAD.

CONTENIDO:

PLANTAS DE ENTREPISOS Y DETALLES ESTRUCTURALES

ESCALA:
INDICADA

FECHA:
MARZO DE 2025


HOJA N°:
E-04

FIRMA Y SELLO DE PROFESIONALES RESPONSABLES


DISEÑO ARQUITECTÓNICO: FIRMA:	DIRECTOR DE LA OBRA: FIRMA:	RESPONSABLE DEL TRAMITE: FIRMA:
DISEÑO ARQUITECTÓNICO: SELLO:	DIRECTOR DE LA OBRA: SELLO:	RESPONSABLE DEL TRAMITE: SELLO:

REGISTRO NACIONAL DE ARQUITECTOS
E INGENIEROS
CARLOS FRANCISCO CALVO MAIDA
A-3797
ARQUITECTO


REGISTRO NACIONAL DE ARQUITECTOS
E INGENIEROS
Morena Guadalupe Vázquez López
A-4576
ARQUITECTA

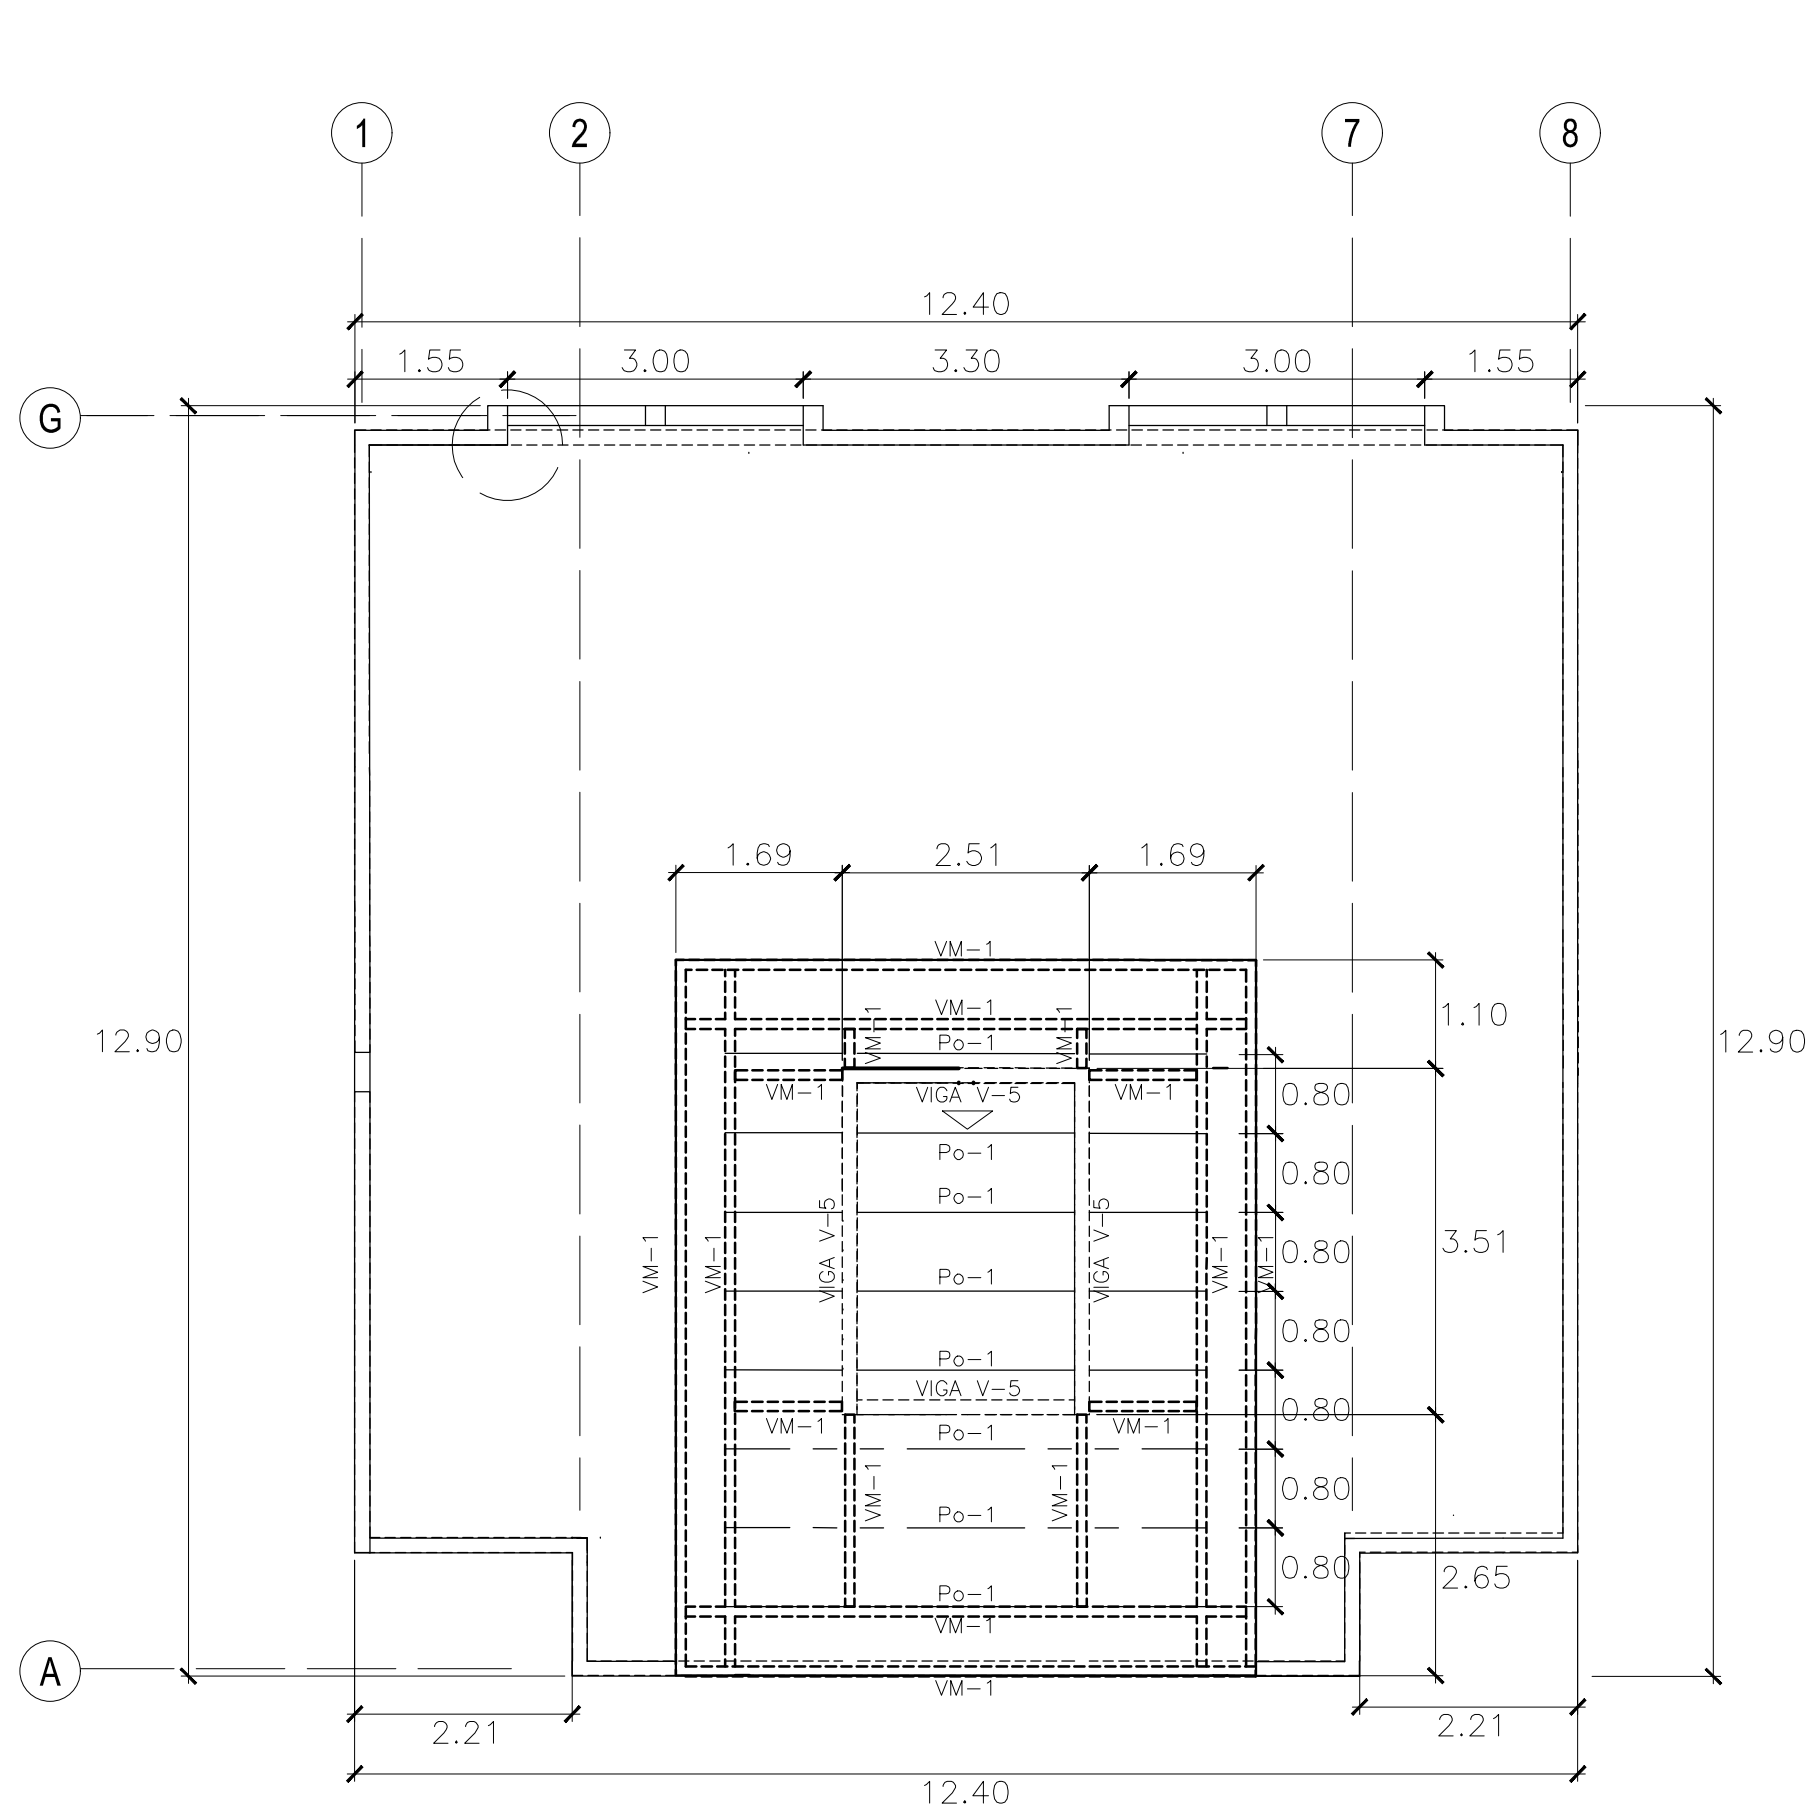


PLANTA DE TECHOS
ESC. 1:75

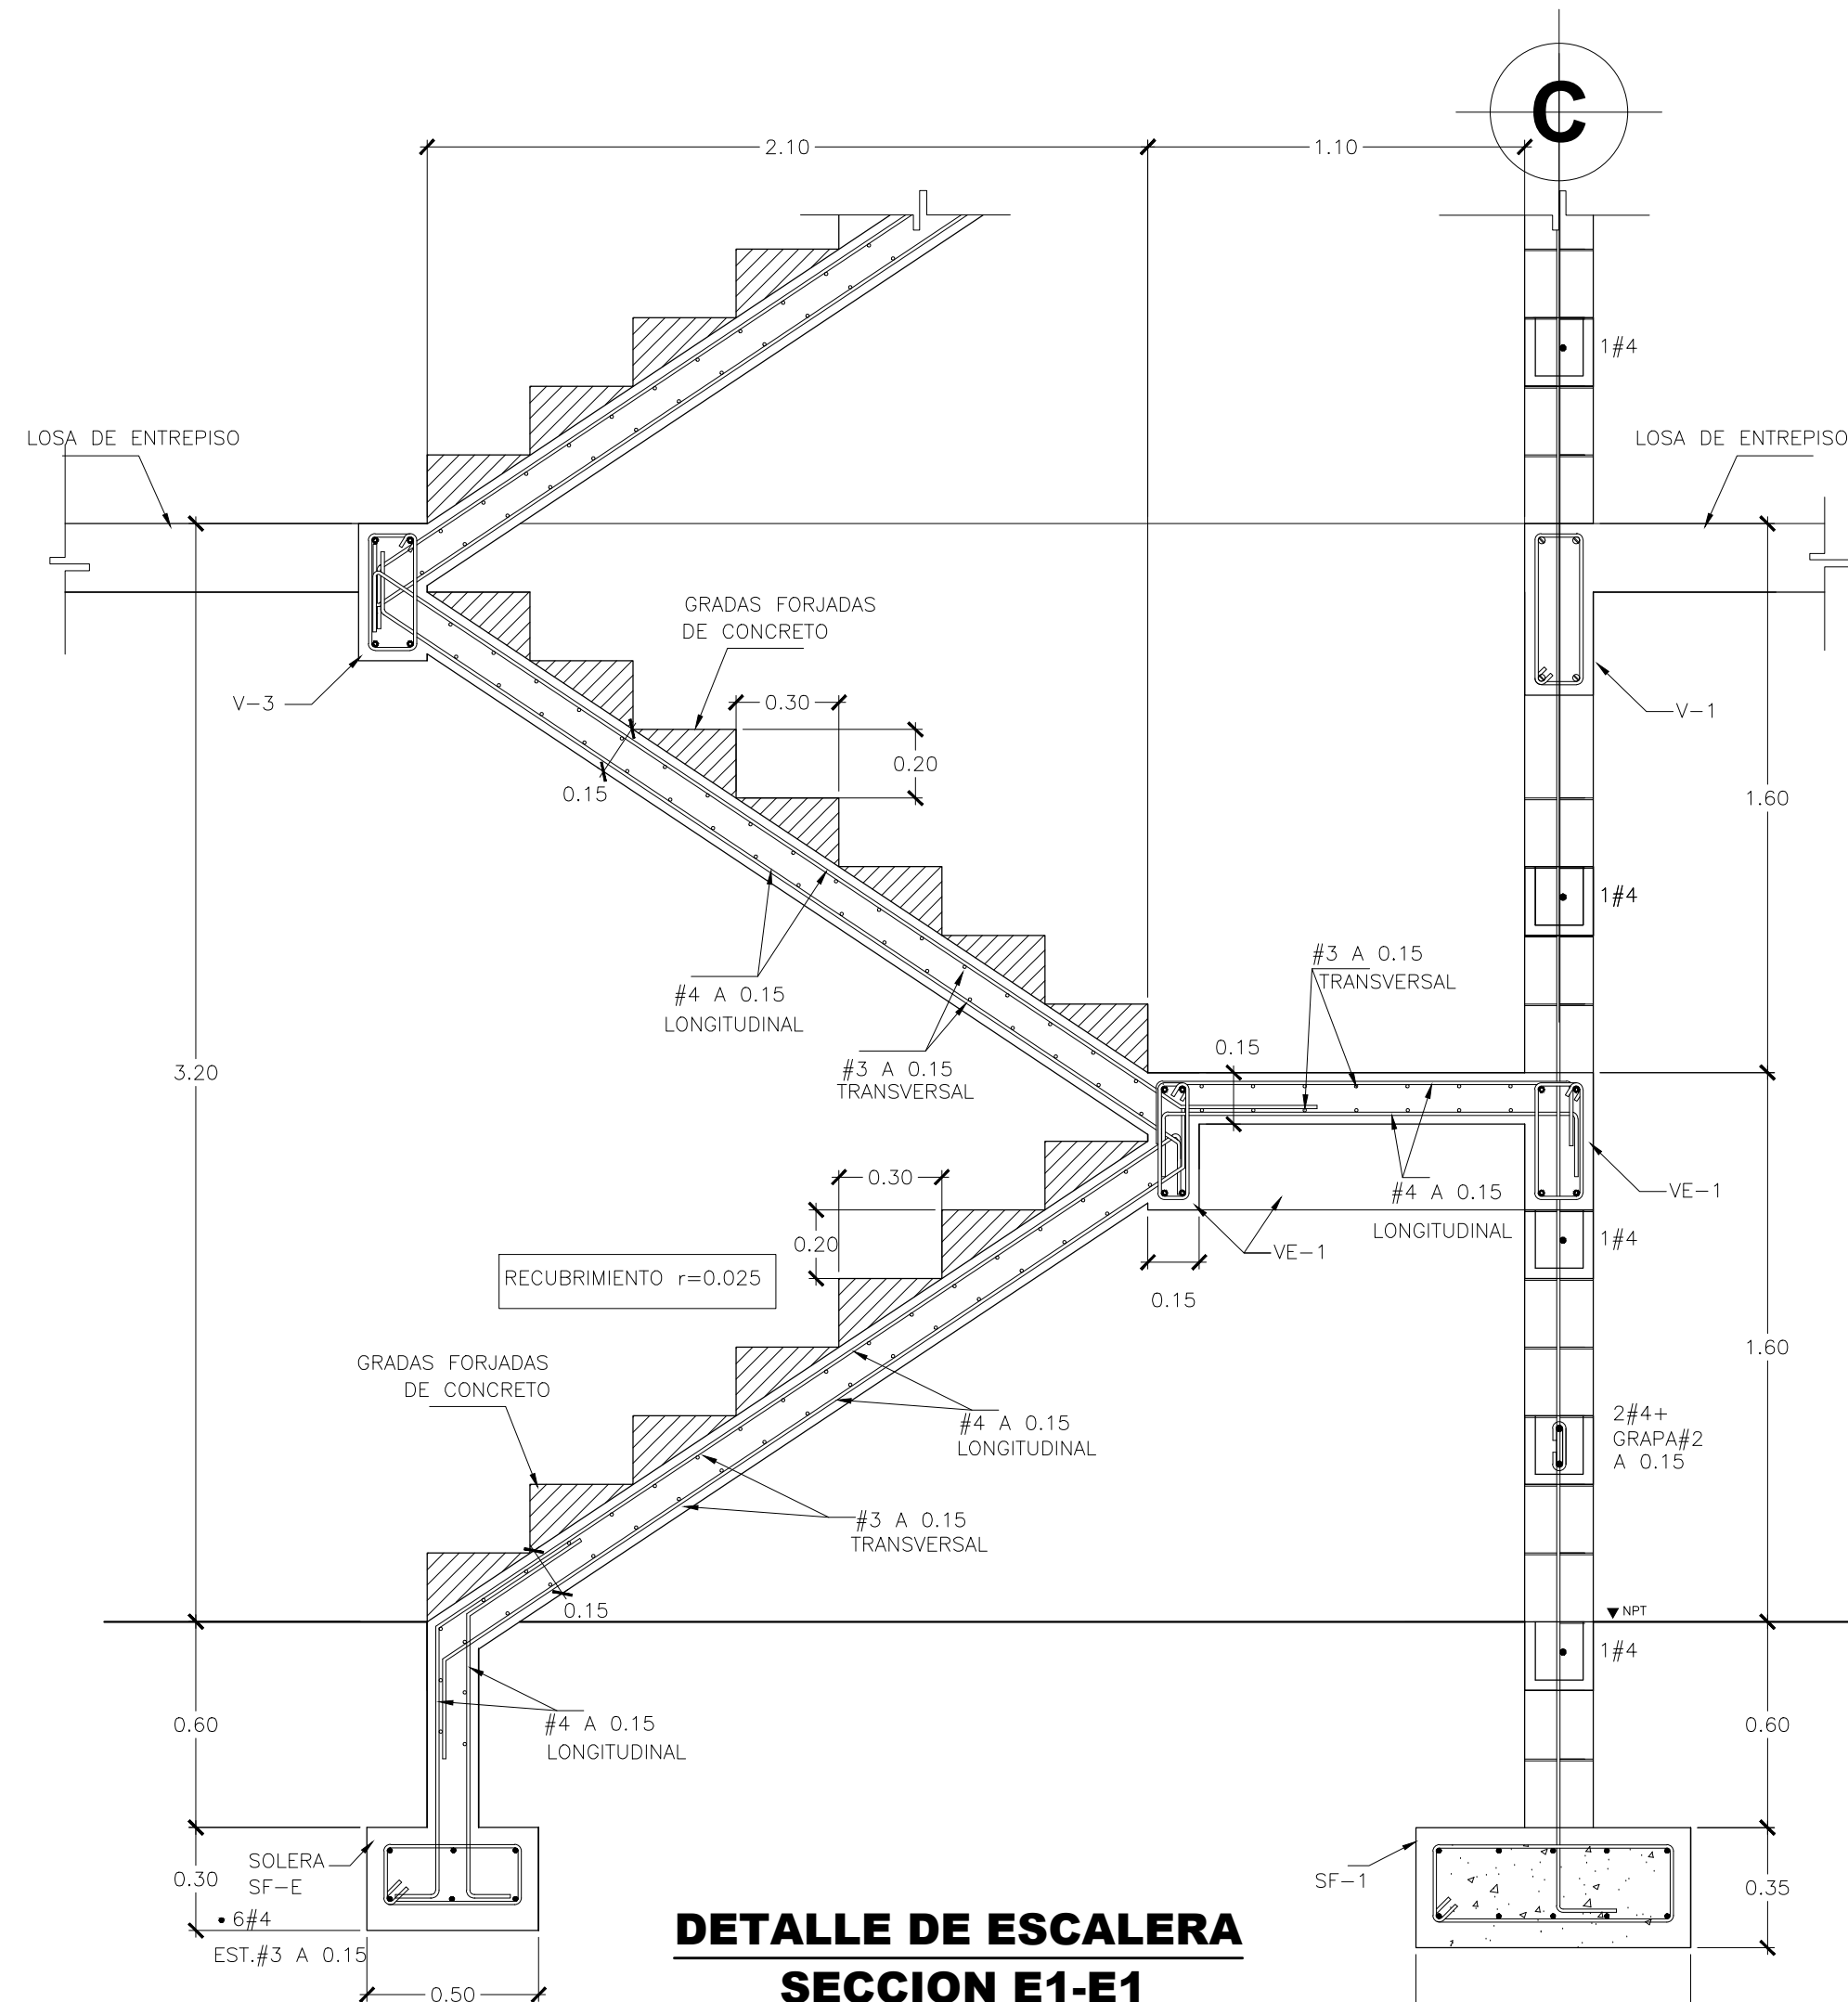


DETALLE DE ESCALERA
SECCION E1-E1
ESC. 1:20

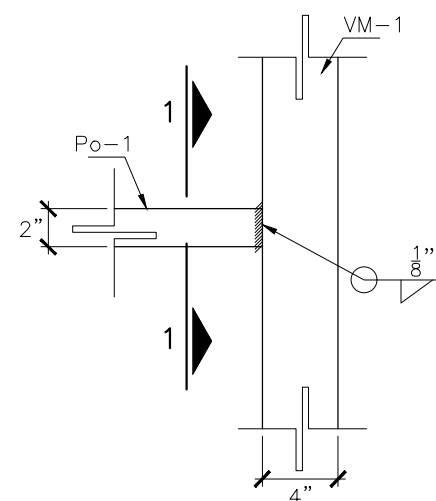


UNION VIGA A POLIN
PLANTA ESC. 1:10

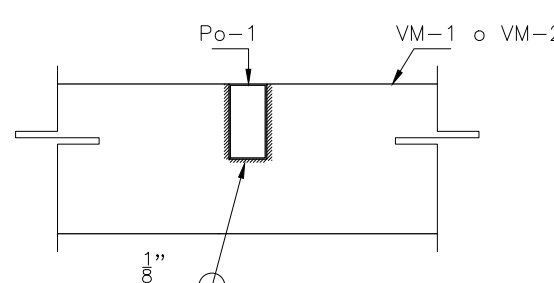


SECCION 1-1
ELEVACION ESC. 1:10

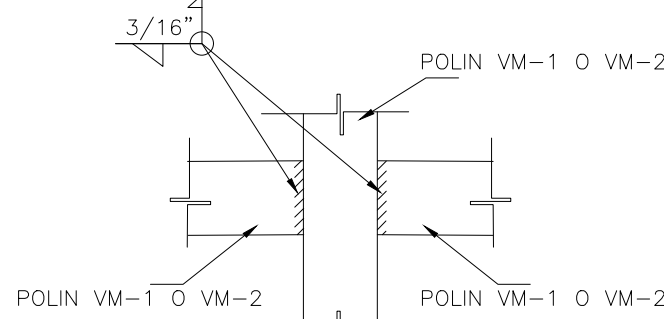


CONEXION ENTRE VIGAS
METALICAS
ESC. 1:10

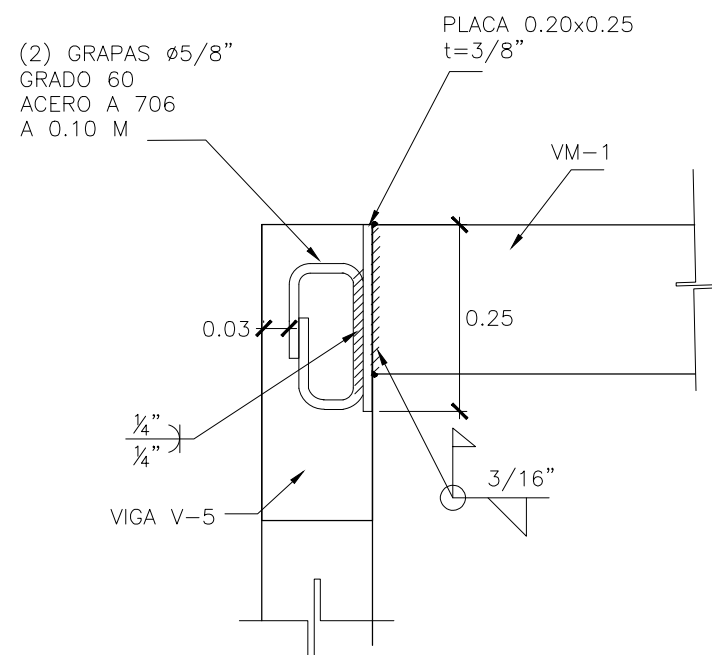


APOYO DE VM-1 A PARED
ESC. 1:10

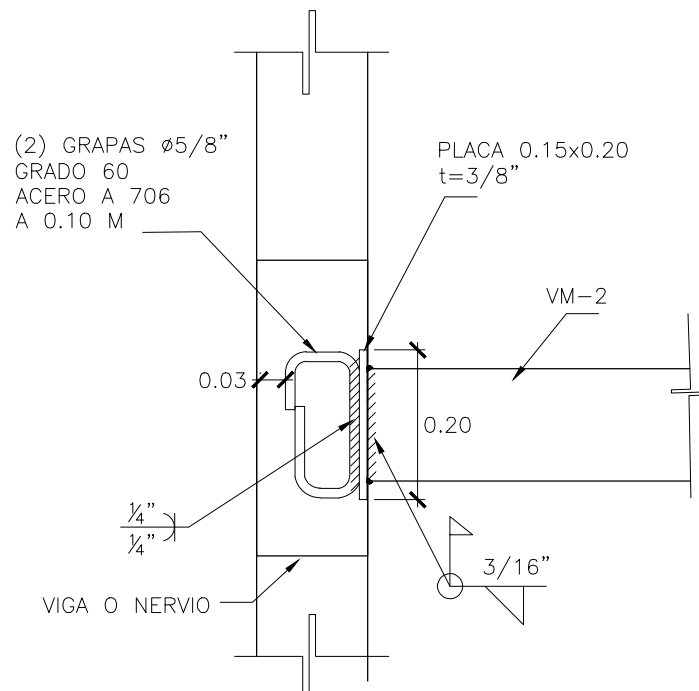

APOYO DE EM-2 A PARED
ESC. 1:10

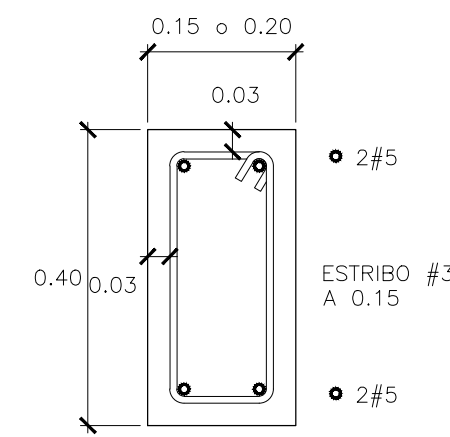

VIGA VE-1
ESC. 1:10

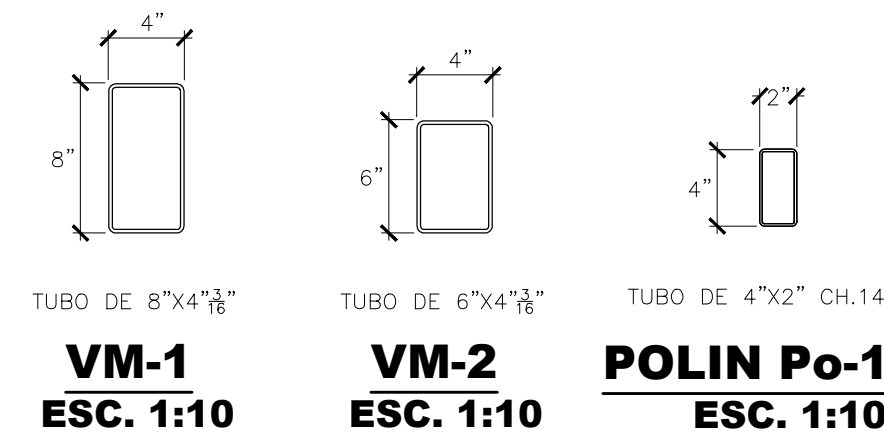

VM-1
ESC. 1:10

VM-2
ESC. 1:10

POLIN Po-1
ESC. 1:10



SELLOS DE APROBACION:

ESTE PLANO FORMA PARTE INTEGRAL DE LA RESOLUCION EMITIDA EN FECHA 24 DE JULIO DE 2025 EN FORMATO DIGITAL Y CORRESPONDE AL EXPEDIENTE DE PERMISO DE CONSTRUCCION REFERENCIA 0333-2025. PRESENTADO BAJO LA RESPONSABILIDAD DE LA ARQ. MORENA GUADALUPE VASQUEZ LOPEZ CON REGISTRO PROFESIONAL VMVDU A-4576.

PRESENTA:



Tel. 7526-1553
asismica@gmail.com

PROYECTO
CONSTRUCCION DE VIVIENDA DE DOS NIVELES
Y TERRAZA EMPRESA AZZUL
PROPIETARIOS
EMPRESA AZZUL S.A DE C.V

UBICACION:
CANTON SAN RAFAEL, CONDOMINIOS RECREATIVOS LOMAS DE SAN BLASS, CALLE
MAJAHUAL, POLIGONO 6, NIVEL 1, NUMERO 18, DEPARTAMENTO DE LA LIBERTAD.

CONTENIDO:

PLANTA DE TECHOS Y DETALLES ESTRUCTURALES



ESCALA:
INDICADA

FECHA:
MARZO DE 2025

HOJA N°:
E-05

FIRMA Y SELLO DE PROFESIONALES RESPONSABLES

DISEÑO ARQUITECTÓNICO: FIRMA:	DIRECTOR DE LA OBRA: FIRMA:	RESPONSABLE DEL TRAMITE: FIRMA:
DISEÑO ARQUITECTÓNICO: SELLO:	DIRECTOR DE LA OBRA: SELLO:	RESPONSABLE DEL TRAMITE: SELLO:
	REGISTRO NACIONAL DE ARQUITECTOS E INGENIEROS CARLOS FRANCISCO CALVO MORA A-3297 ARQUITECTO	REGISTRO NACIONAL DE ARQUITECTOS E INGENIEROS Morena Guadalupe Vázquez López A-4576 ARQUITECTA

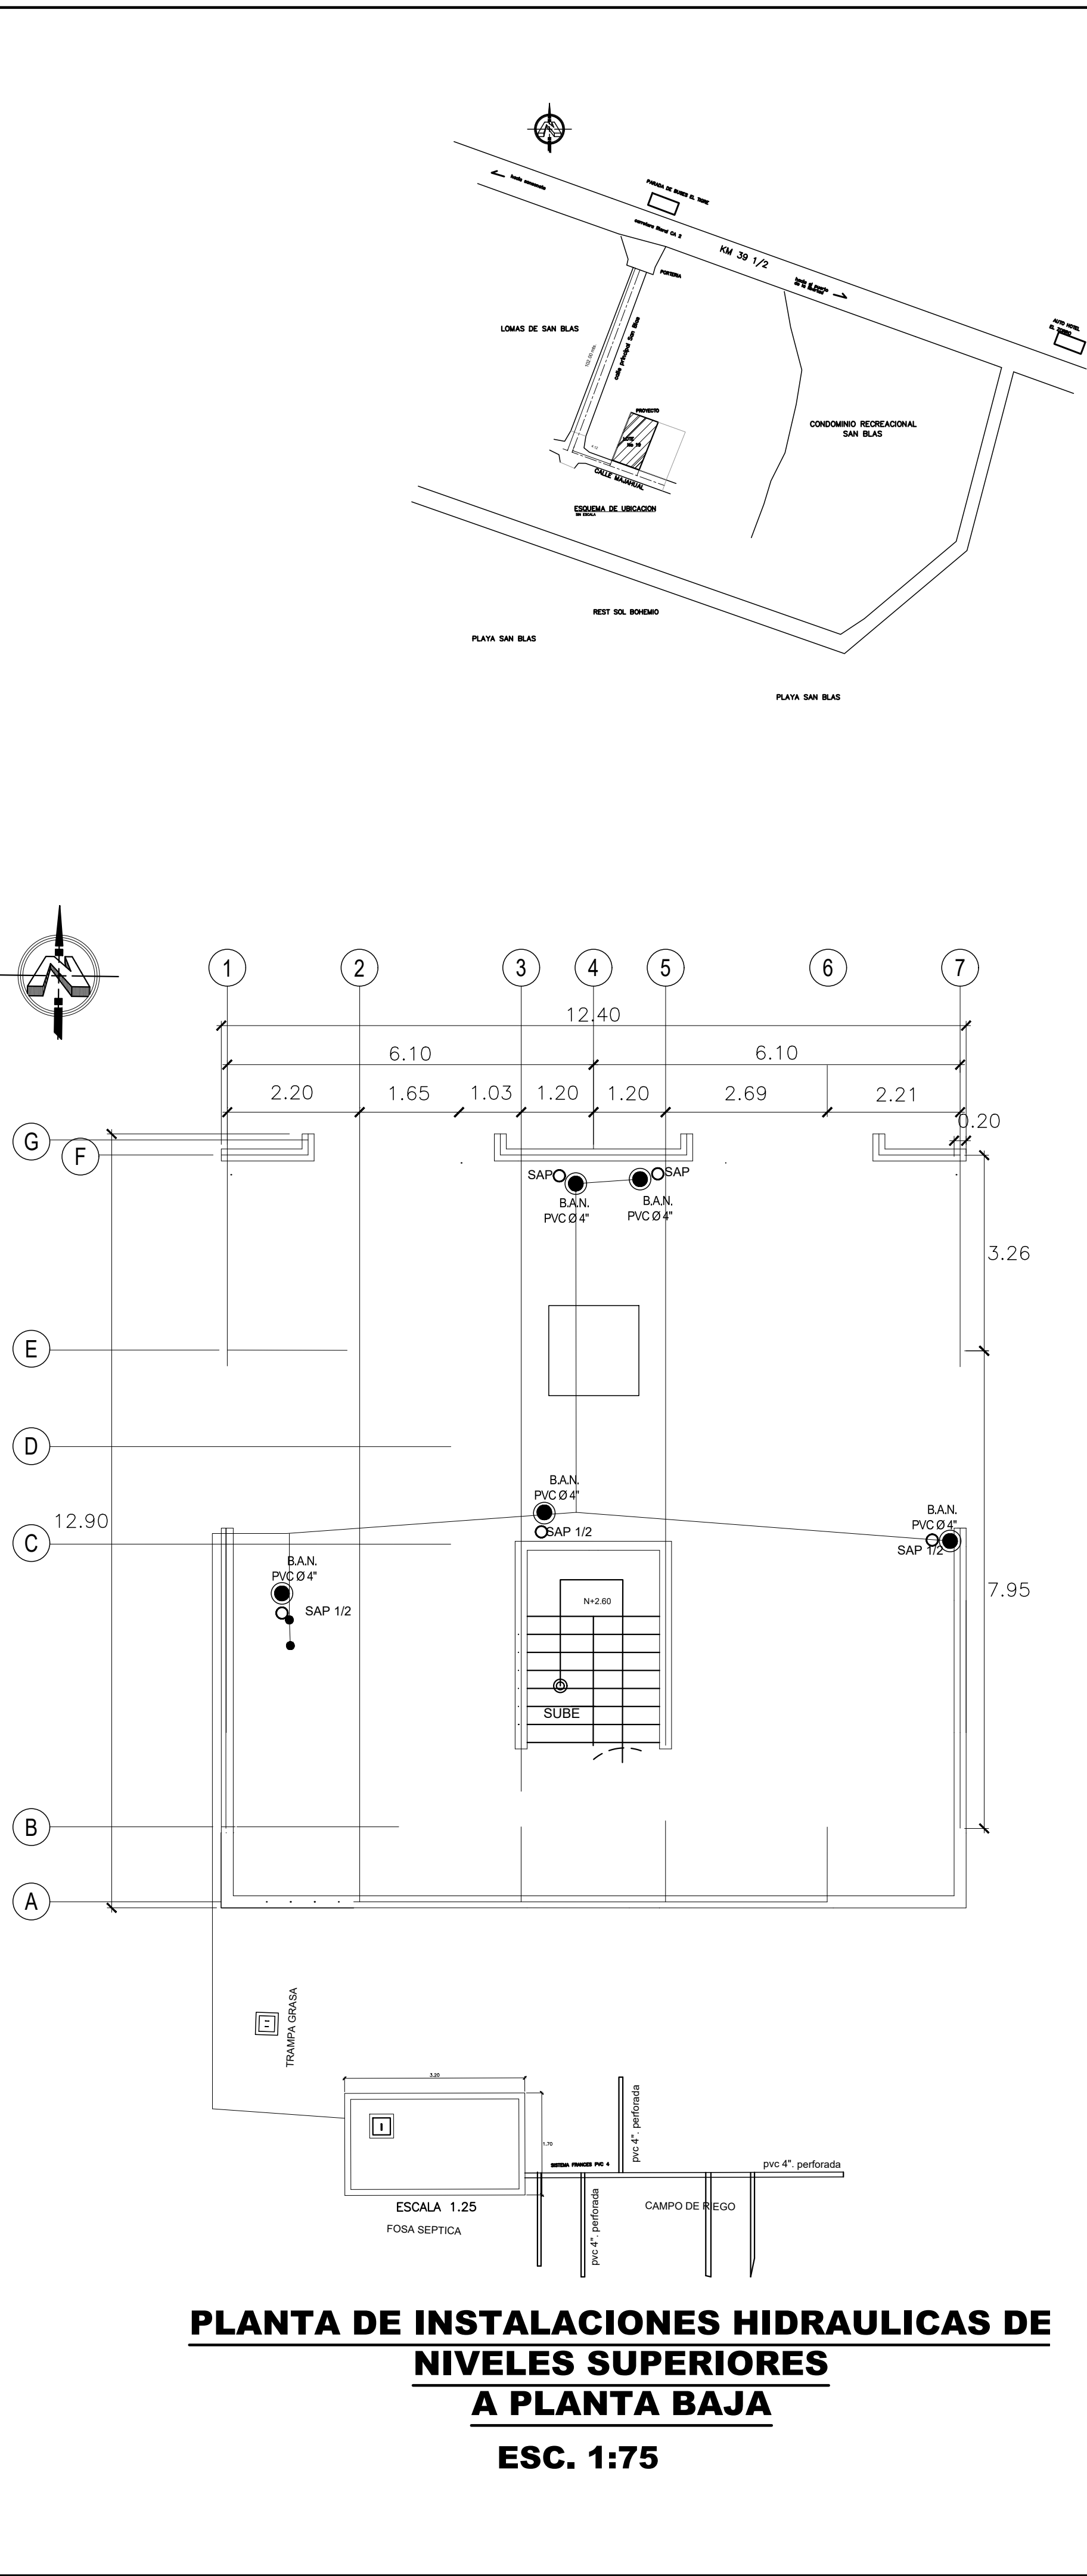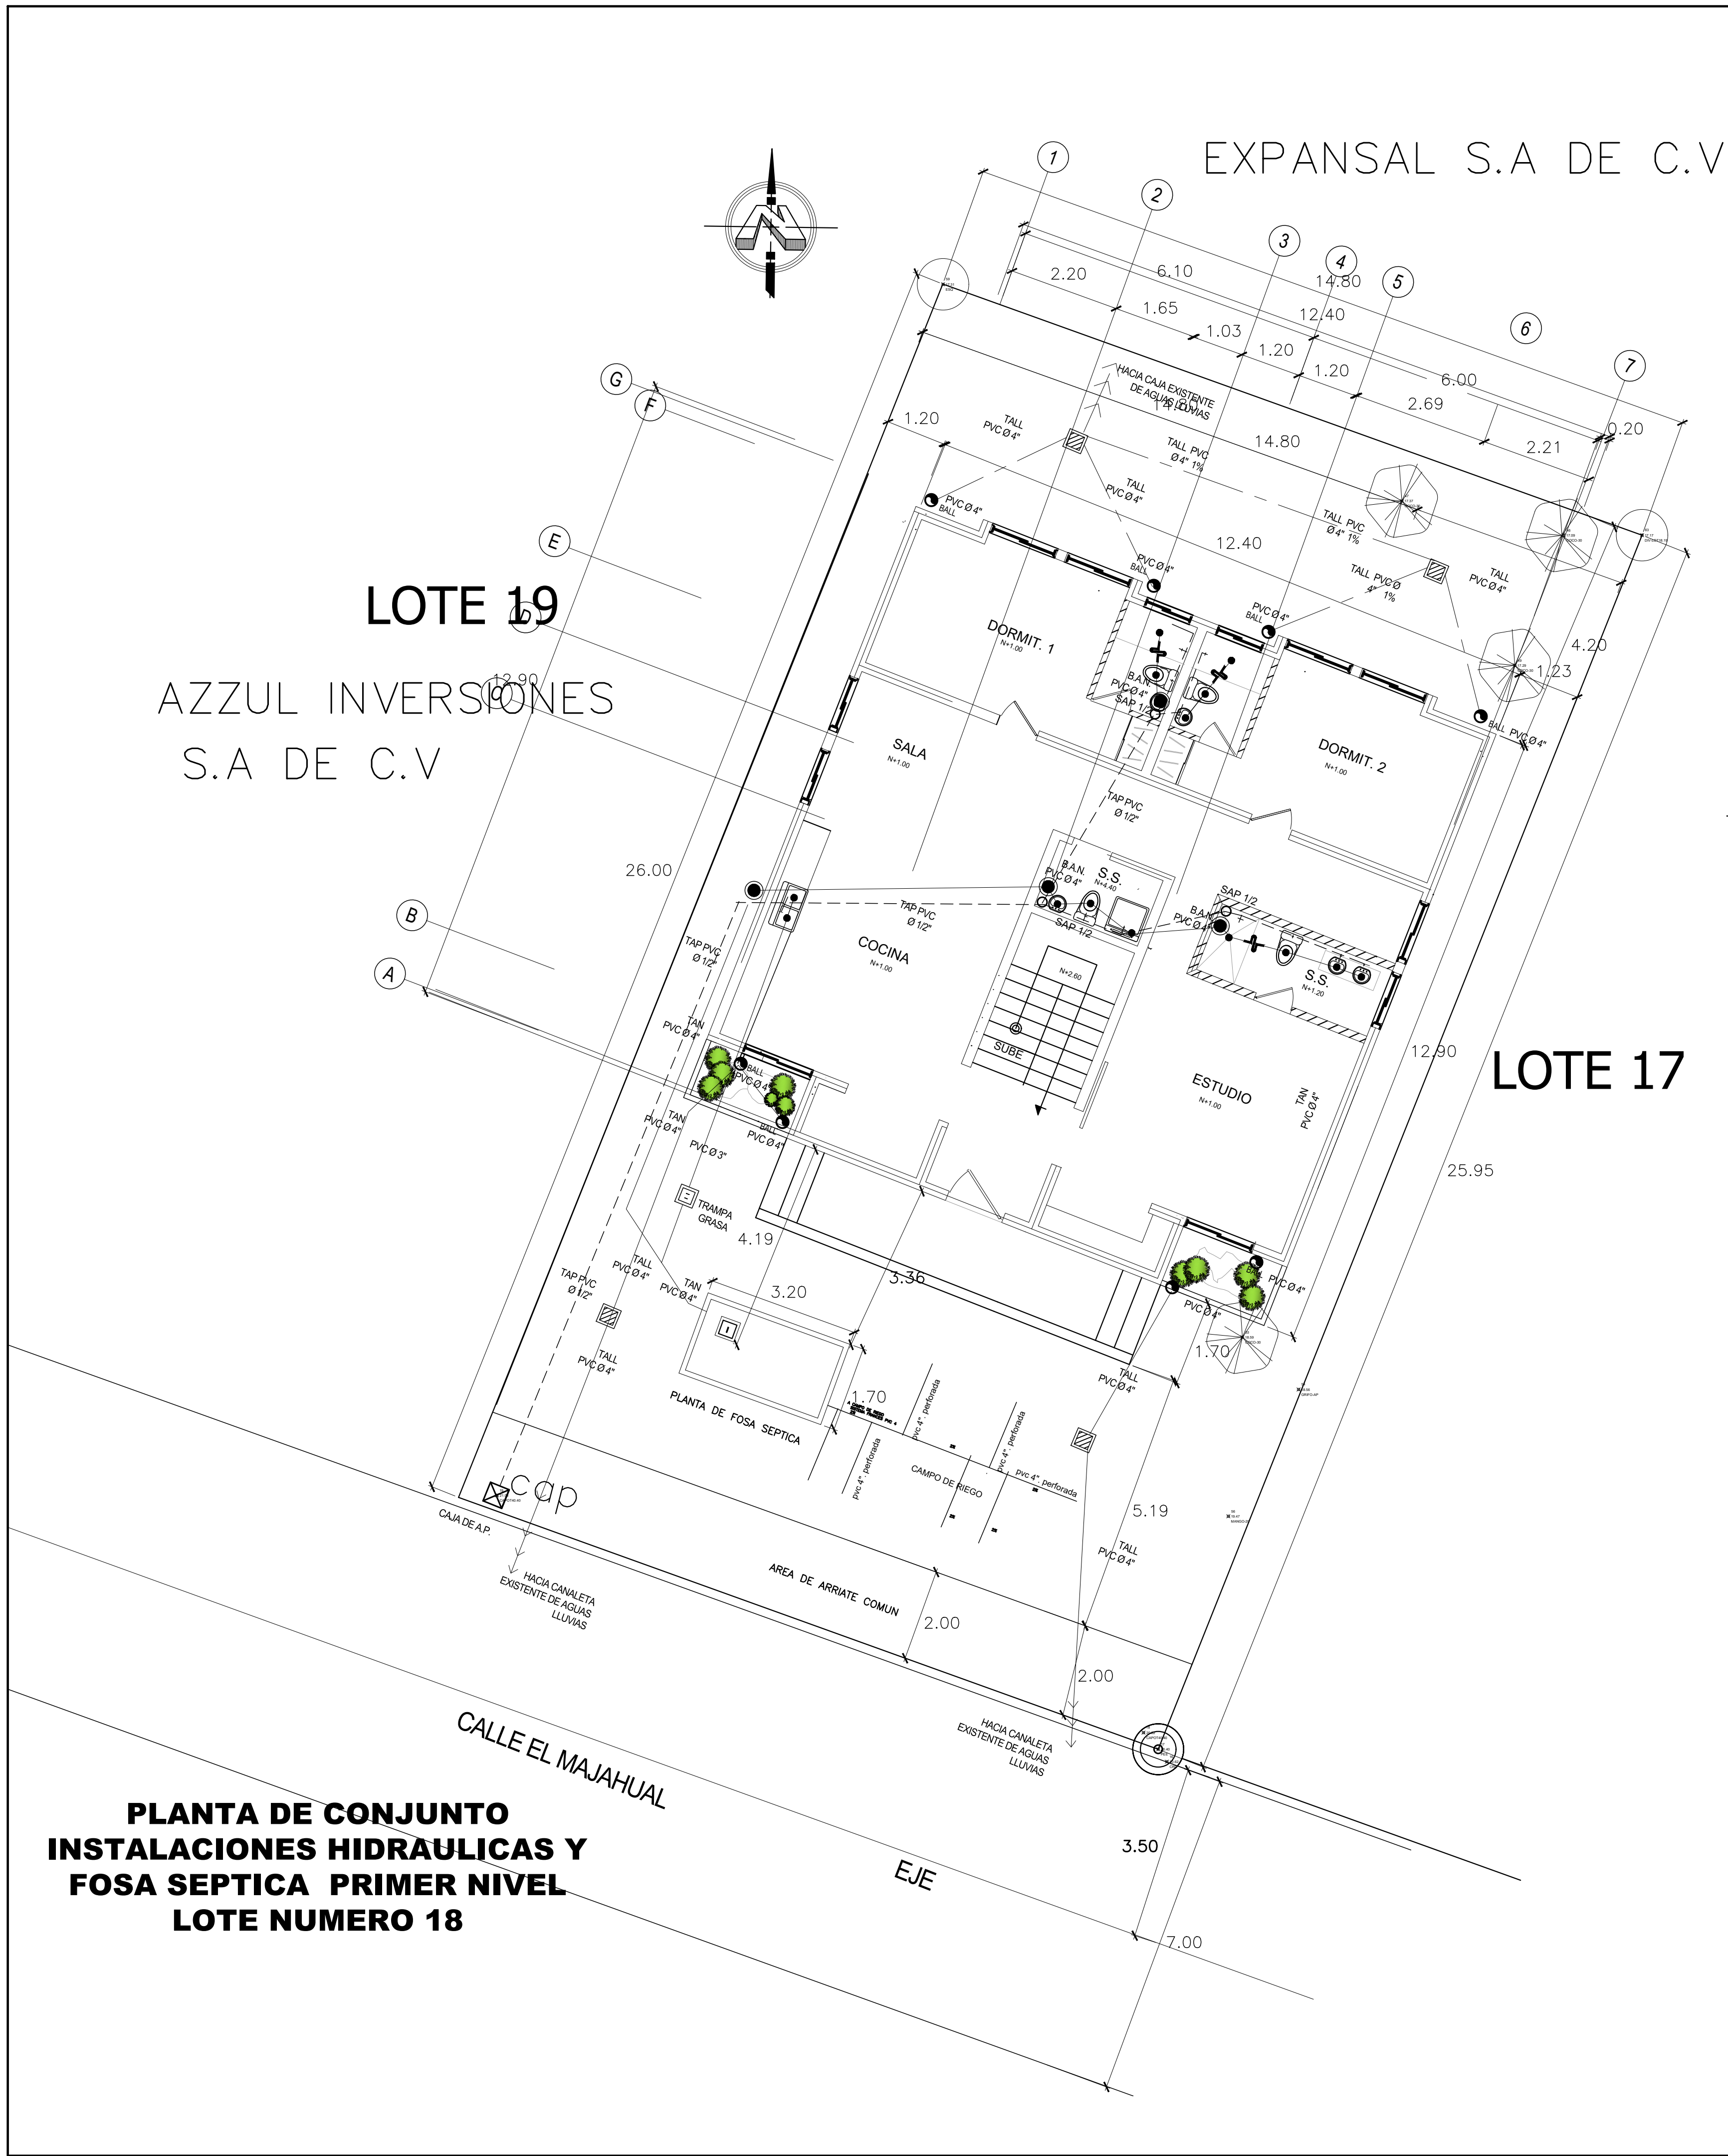

REGISTRO NACIONAL DE ARQUITECTOS E INGENIEROS
BORIS ANTONIO RODRIGUEZ RIVERA
IC-2054
INGENIERO CIVIL

SELLOS DE APROBACION:

ESTE PLANO FORMA PARTE INTEGRAL DE LA RESOLUCION EMITIDA EN FECHA 24 DE JULIO DE 2025 EN FORMATO DIGITAL Y CORRESPONDE AL EXPEDIENTE DE PERMISO DE CONSTRUCCION REFERENCIA 0333-2025. PRESENTADO BAJO LA RESPONSABILIDAD DE LA ARQ. MORENA GUADALUPE VASQUEZ LOPEZ CON REGISTRO PROFESIONAL VMVDU A-4576.

PRESENTA:

ING. BORIS RODRIGUEZ

PROYECTO:
CONSTRUCCION DE VIVIENDA DE DOS NIVELES
Y TERRAZA EMPRESA AZZUL

PROPIETARIOS:
EMPRESA AZZUL S.A DE C.V

UBICACION:
CANTON SAN RAFAEL, CONDOMINIO RECREATIVO, LOMAS DE SAN BLAS, CALLE MAJAHUAL, POLIGONO 6, NUMERO 19, LA LIBERTAD COSTA. DEPARTAMENTO DE LA LIBERTAD






CONTENIDO:

PLANTAS DE INSTALACION HIDRAULICA
Y FOSA SEPTICA

ESCALA: INDICADA	AREA TOTAL DEL TERRENO: 384.76 M2 AREA TOTAL DE CONSTRUCCION: 458.61 M2	FECHA: MARZO 2025	HOJA N°: HI-01
---------------------	--	----------------------	-------------------

FIRMA Y SELLO DE PROFESIONALES RESPONSABLES

DISEÑO ARQUITECTONICO: FIRMA: DISEÑO ARQUITECTONICO: SELLO:	DIRECTOR DE LA OBRA: FIRMA: DIRECTOR DE LA OBRA: SELLO:	RESPONSABLE DEL TRAMITE: FIRMA: RESPONSABLE DEL TRAMITE: SELLO:
REGISTRO NACIONAL DE ARQUITECTOS E INGENIEROS CARLA PATRICIA RODRIGUEZ DE CHOCOBAR A-2339 ARQUITECTA	REGISTRO NACIONAL DE ARQUITECTOS E INGENIEROS CARLOS FRANCISCO CALICIA MADR A-3297 ARQUITECTO	REGISTRO NACIONAL DE ARQUITECTOS E INGENIEROS Morena Guadalupe Vasquez López A-4576 ARQUITECTA

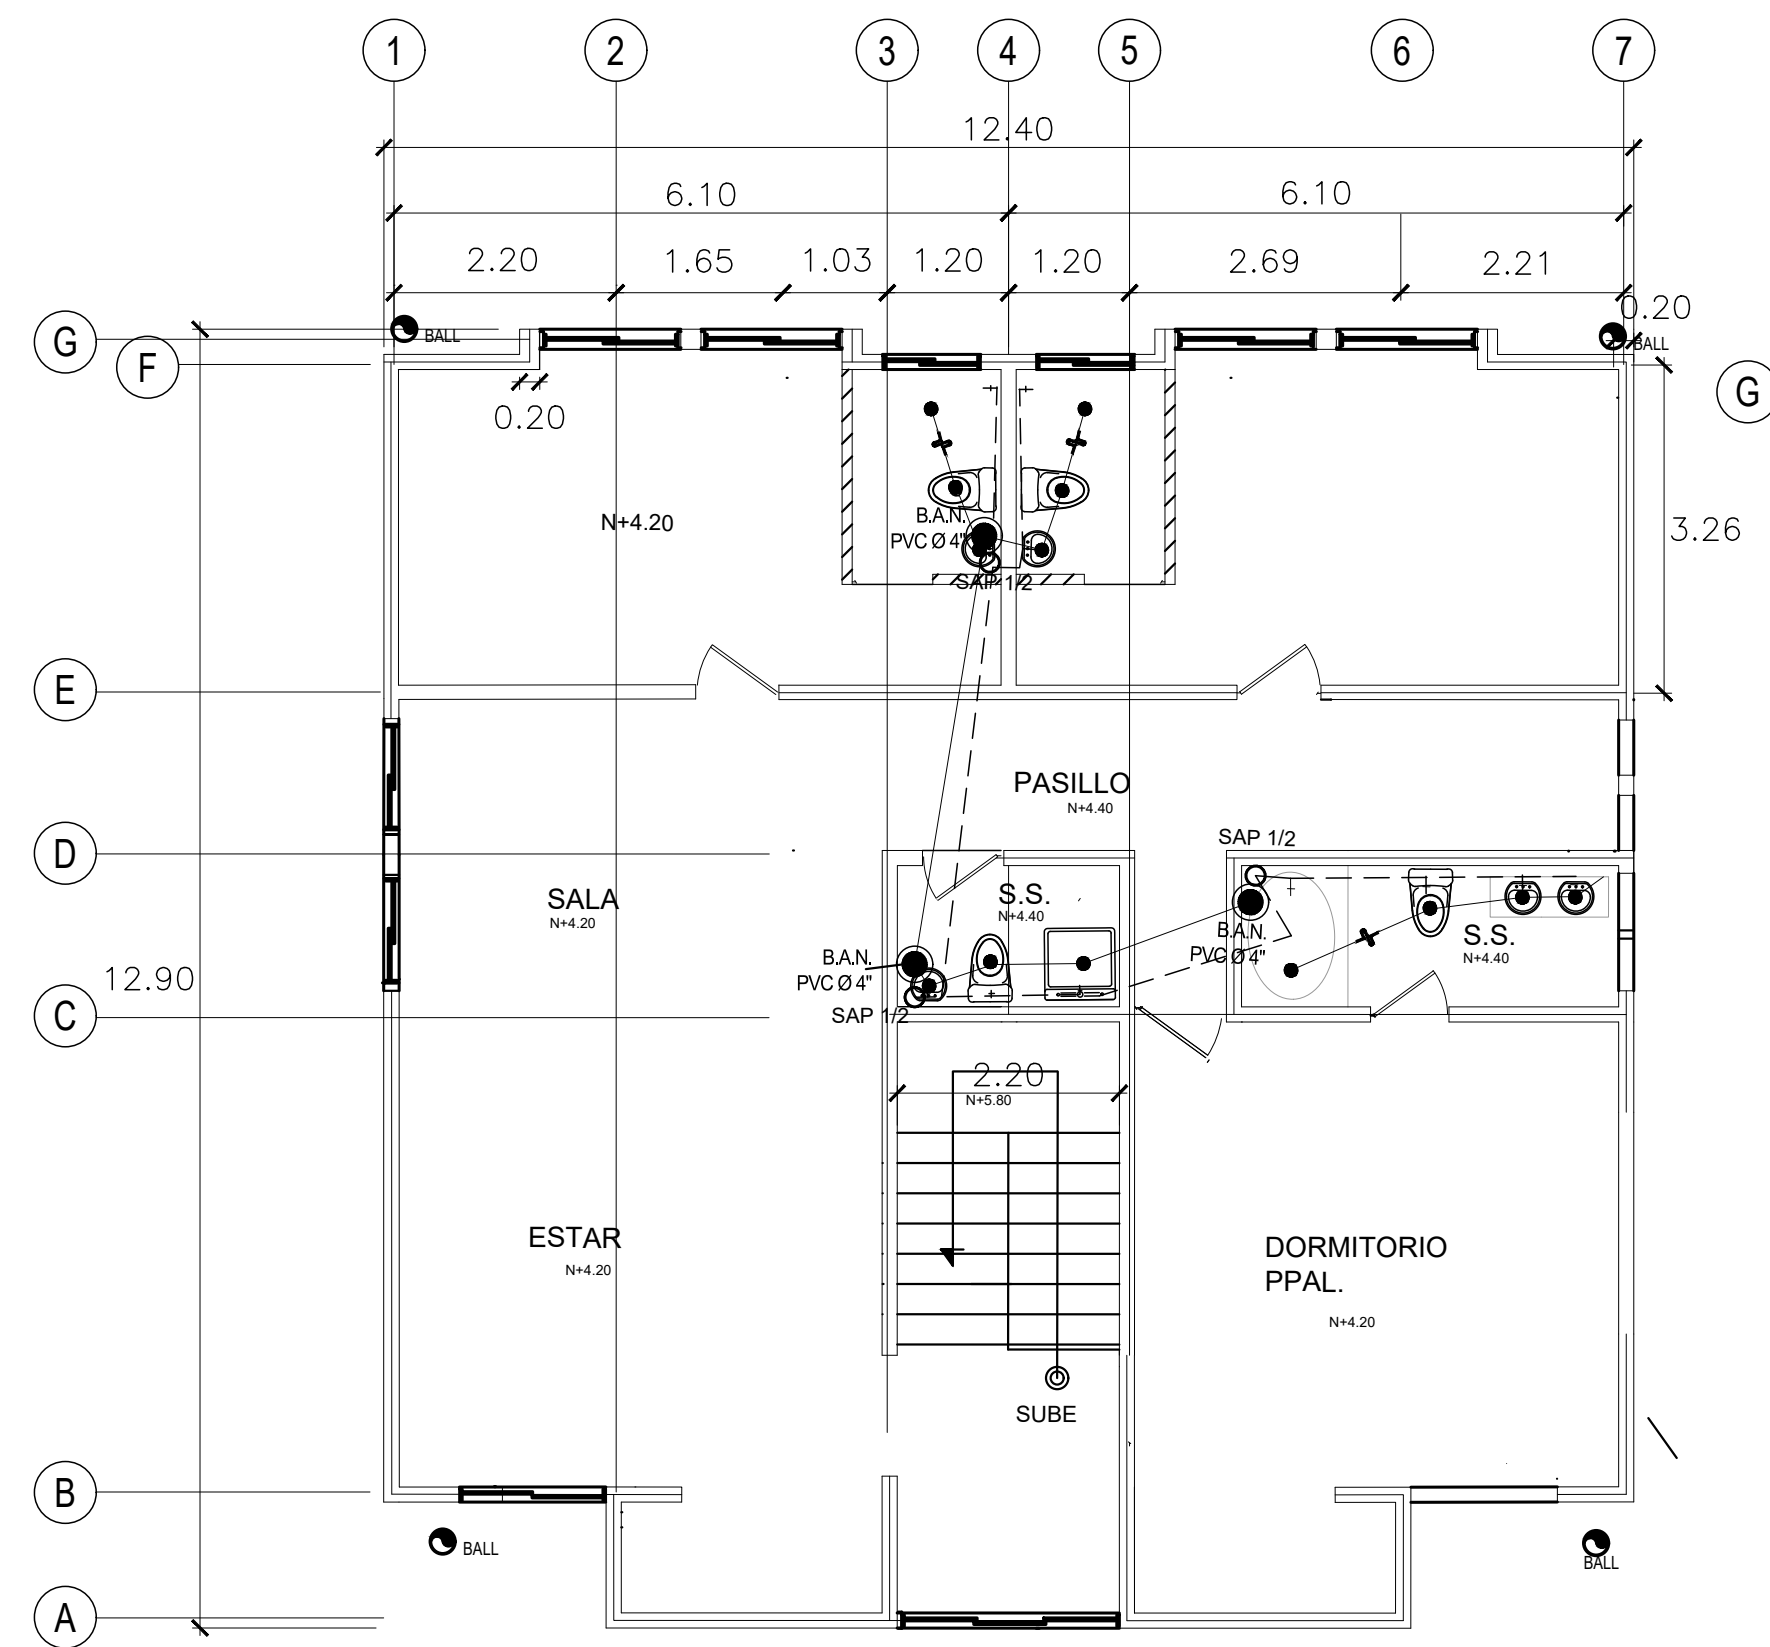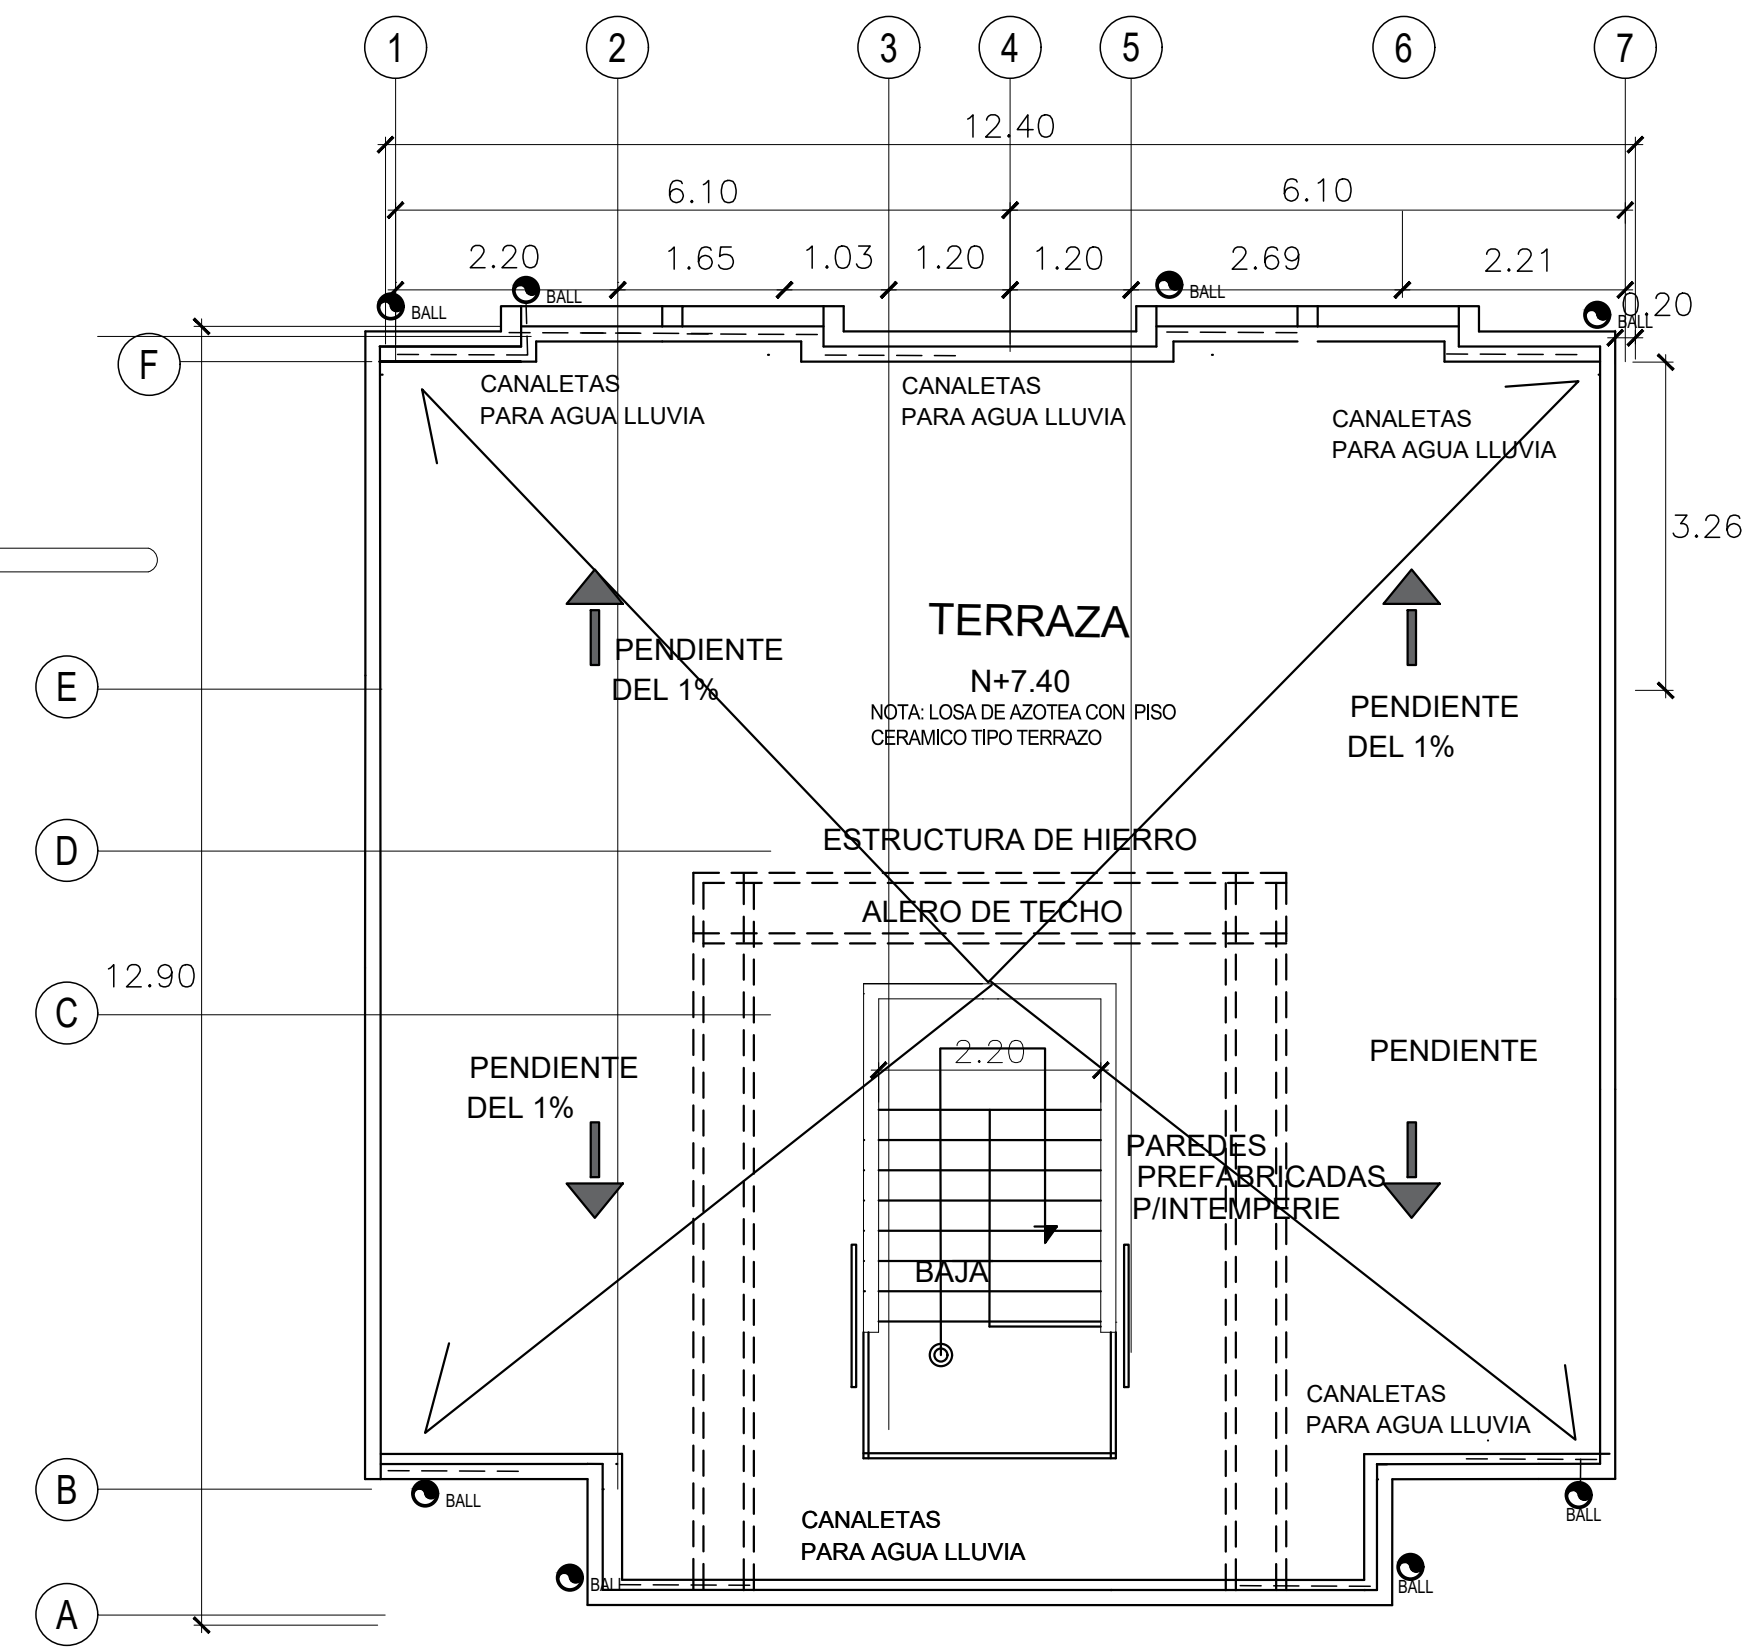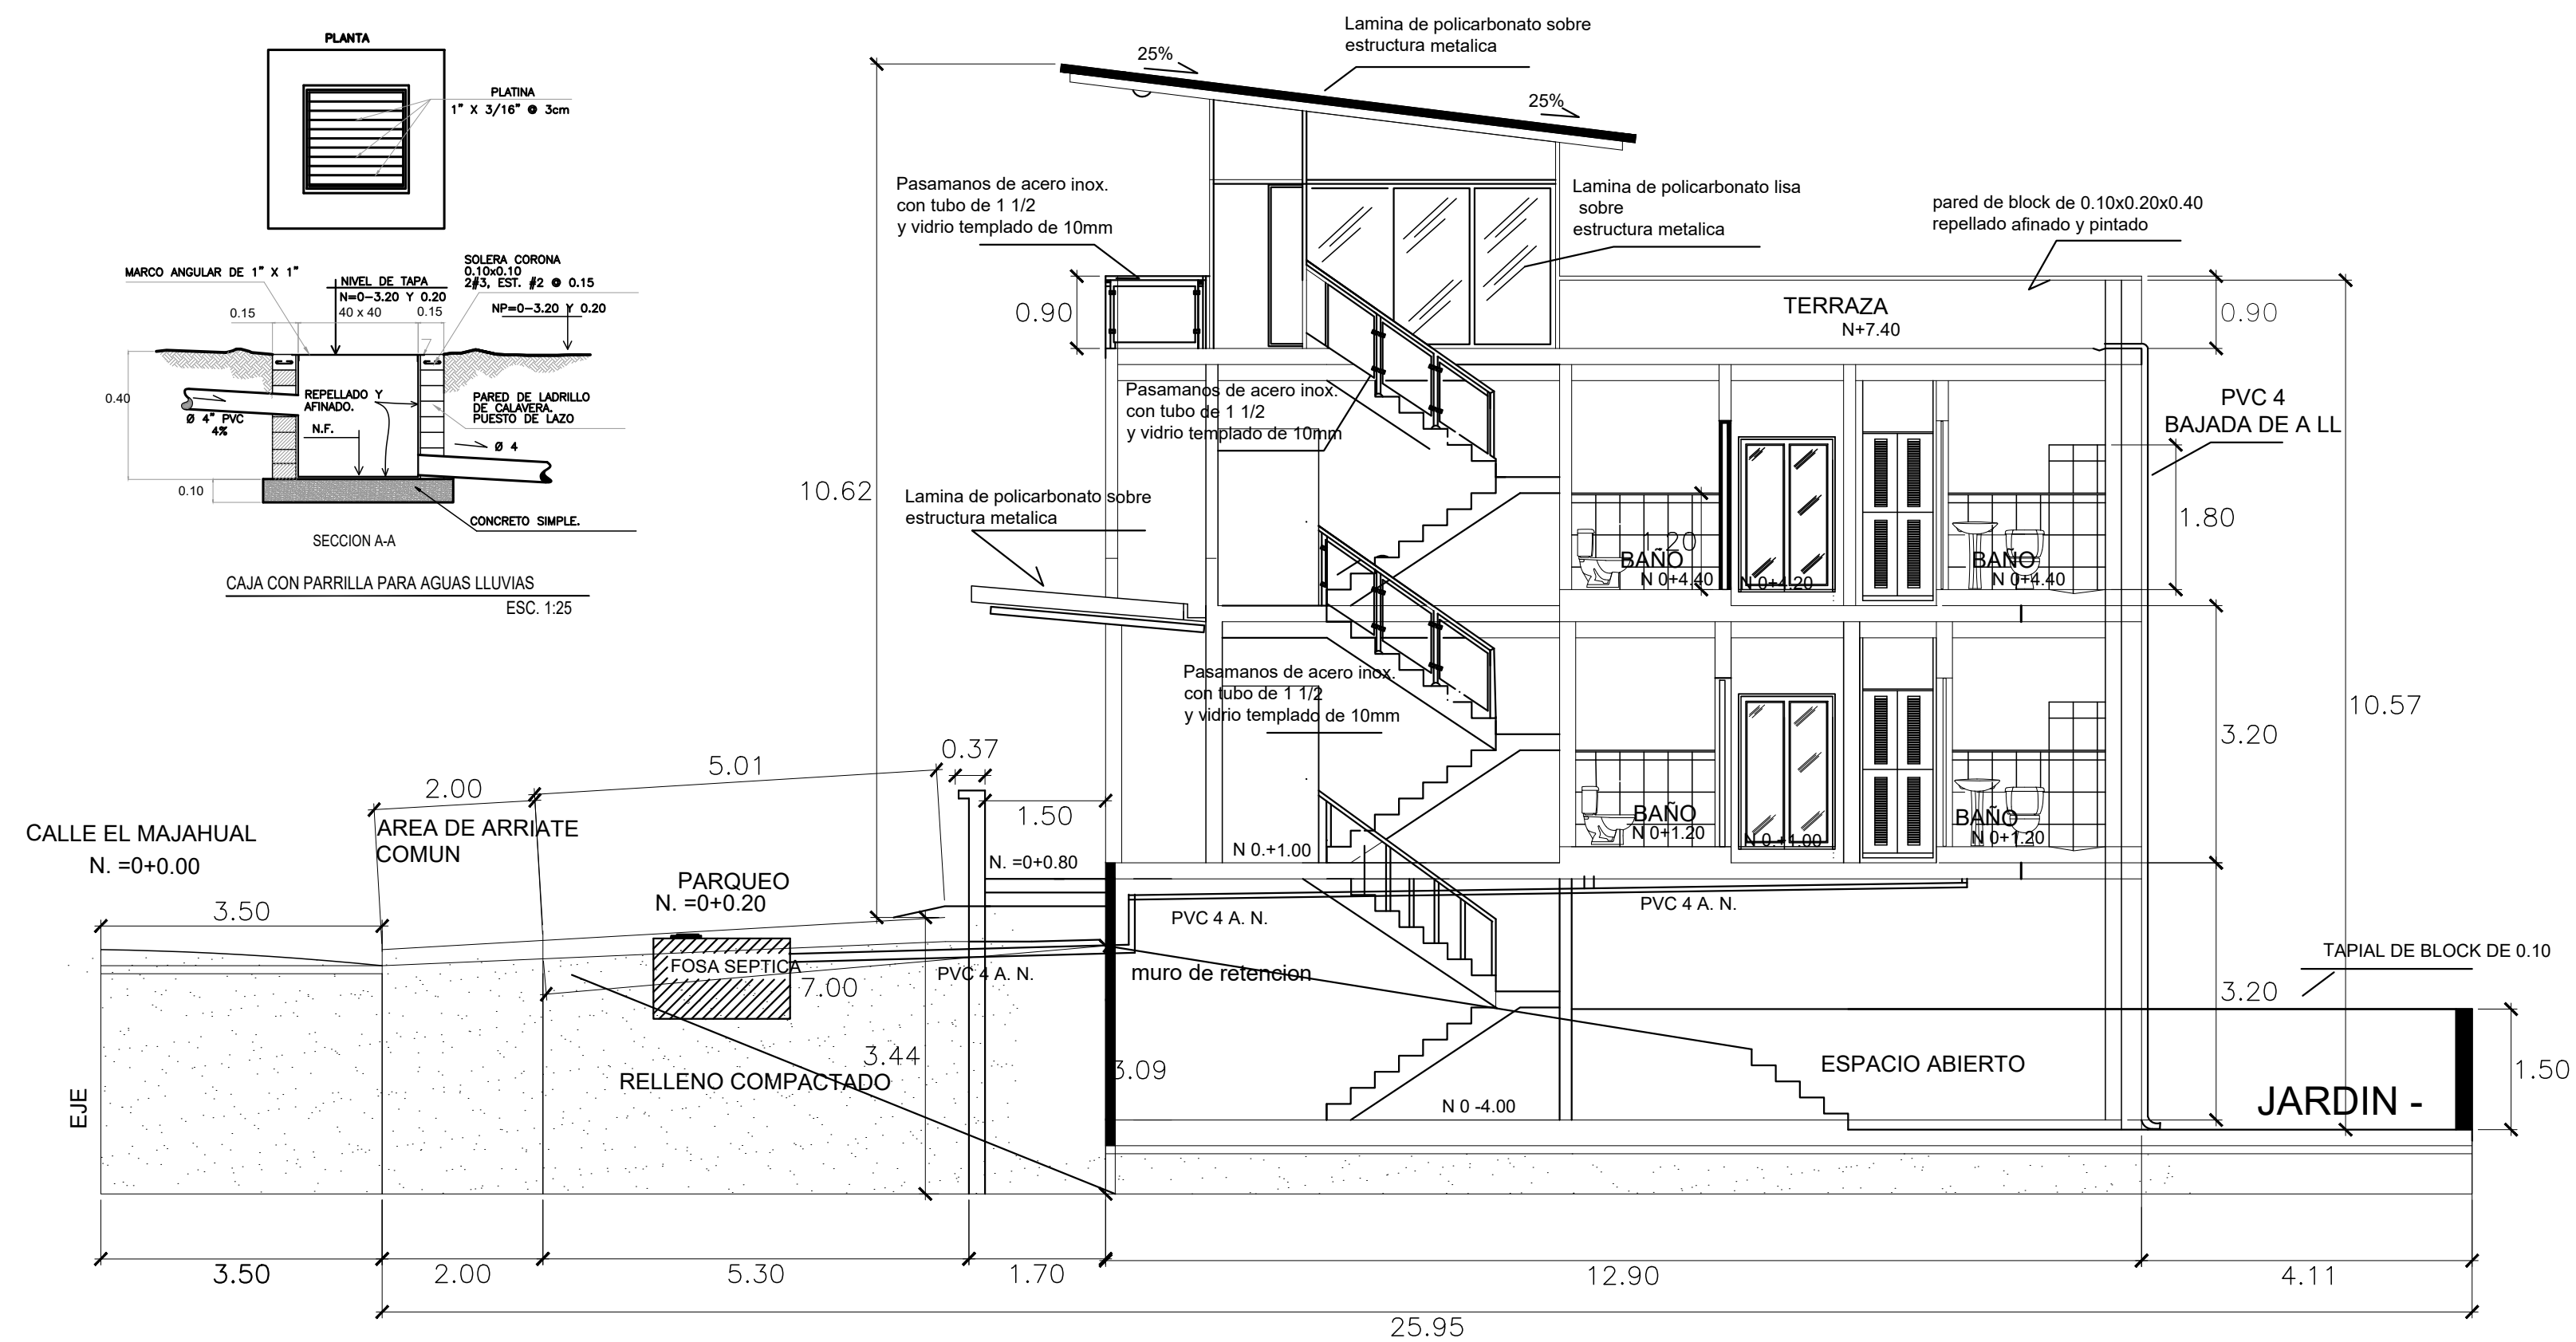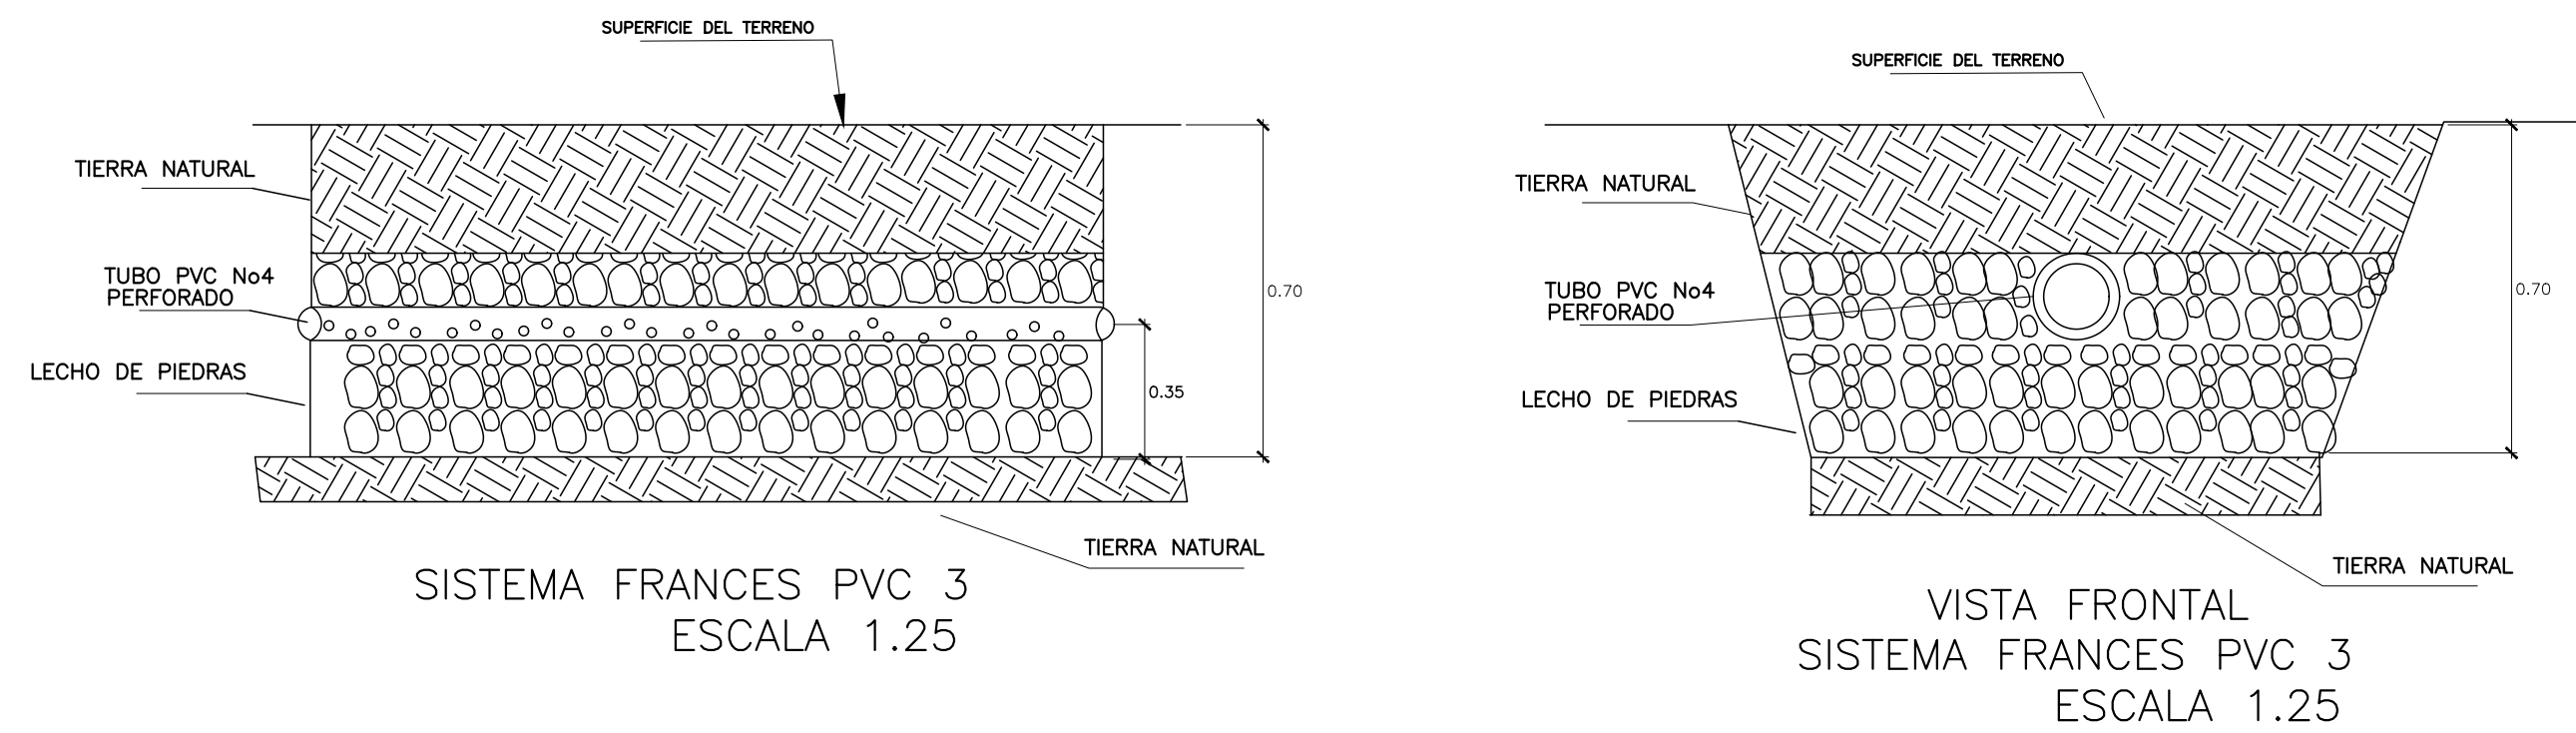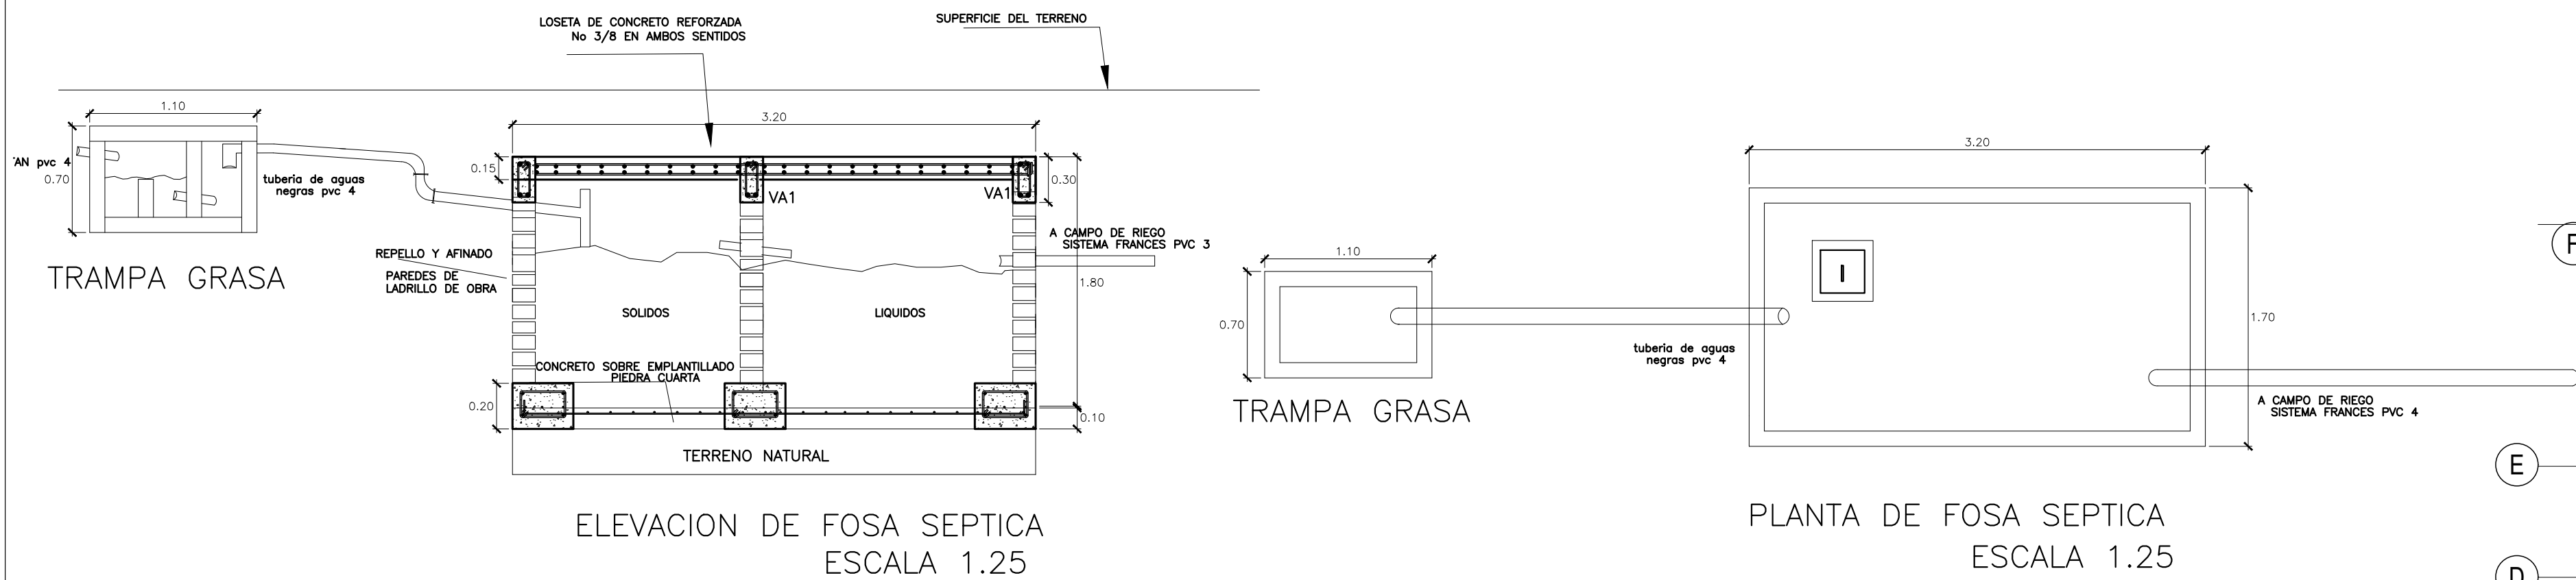

SELLOS DE APROBACION:

ESTE PLANO FORMA PARTE INTEGRAL DE LA RESOLUCION EMITIDA EN FECHA 24 DE JULIO DE 2025 EN FORMATO DIGITAL Y CORRESPONDE AL EXPEDIENTE DE PERMISO DE CONSTRUCCION REFERENCIA 0333-2025. PRESENTADO BAJO LA RESPONSABILIDAD DE LA ARQ. MORENA GUADALUPE VASQUEZ LOPEZ CON REGISTRO PROFESIONAL VMVDU A-4576.

PRESENTA:

ING. BORIS RODRIGUEZ

PROYECTO
CONSTRUCCION DE VIVIENDA DE DOS NIVELES
Y TERRAZA EMPRESA AZZUL

PROPIETARIOS
EMPRESA AZZUL S.A DE C.V


UBICACION:
CANTON SAN RAFAEL, CONDOMINIO RECREATIVO, LOMAS DE SAN BLAS, CALLE MAJAHUAL, POLIGONO 6, NUMERO 19, LA LIBERTAD COSTA. DEPARTAMENTO DE LA LIBERTAD

CONTENIDO:


DETALLE DE FOSA SEPTICA Y TRAMPA GRASA, SECCION

ESCALA: INDICADA	AREA TOTAL DEL TERRENO: 384.76 M2 AREA TOTAL DE CONSTRUCCION: 458.61 M2	FECHA: MARZO 2025	HOJA N°: HI-02
---------------------	--	----------------------	-------------------


FIRMA Y SELLO DE PROFESIONALES RESPONSABLES		
DISEÑO ARQUITECTÓNICO: FIRMA: SELLO:	DIRECTOR DE LA OBRA: FIRMA: SELLO:	RESPONSABLE DEL TRAMITE: FIRMA: SELLO:
REGISTRO NACIONAL DE ARQUITECTOS E INGENIEROS CARLA PATRICIA RODRIGUEZ DE CHOCOBAR A-2339 ARQUITECTA	REGISTRO NACIONAL DE ARQUITECTOS E INGENIEROS CARLOS FRANCISCO RODRIGUEZ MAJIA A-3297 ARQUITECTO	REGISTRO NACIONAL DE ARQUITECTOS E INGENIEROS Morena Guadalupe Vázquez López A- 4576 ARQUITECTA

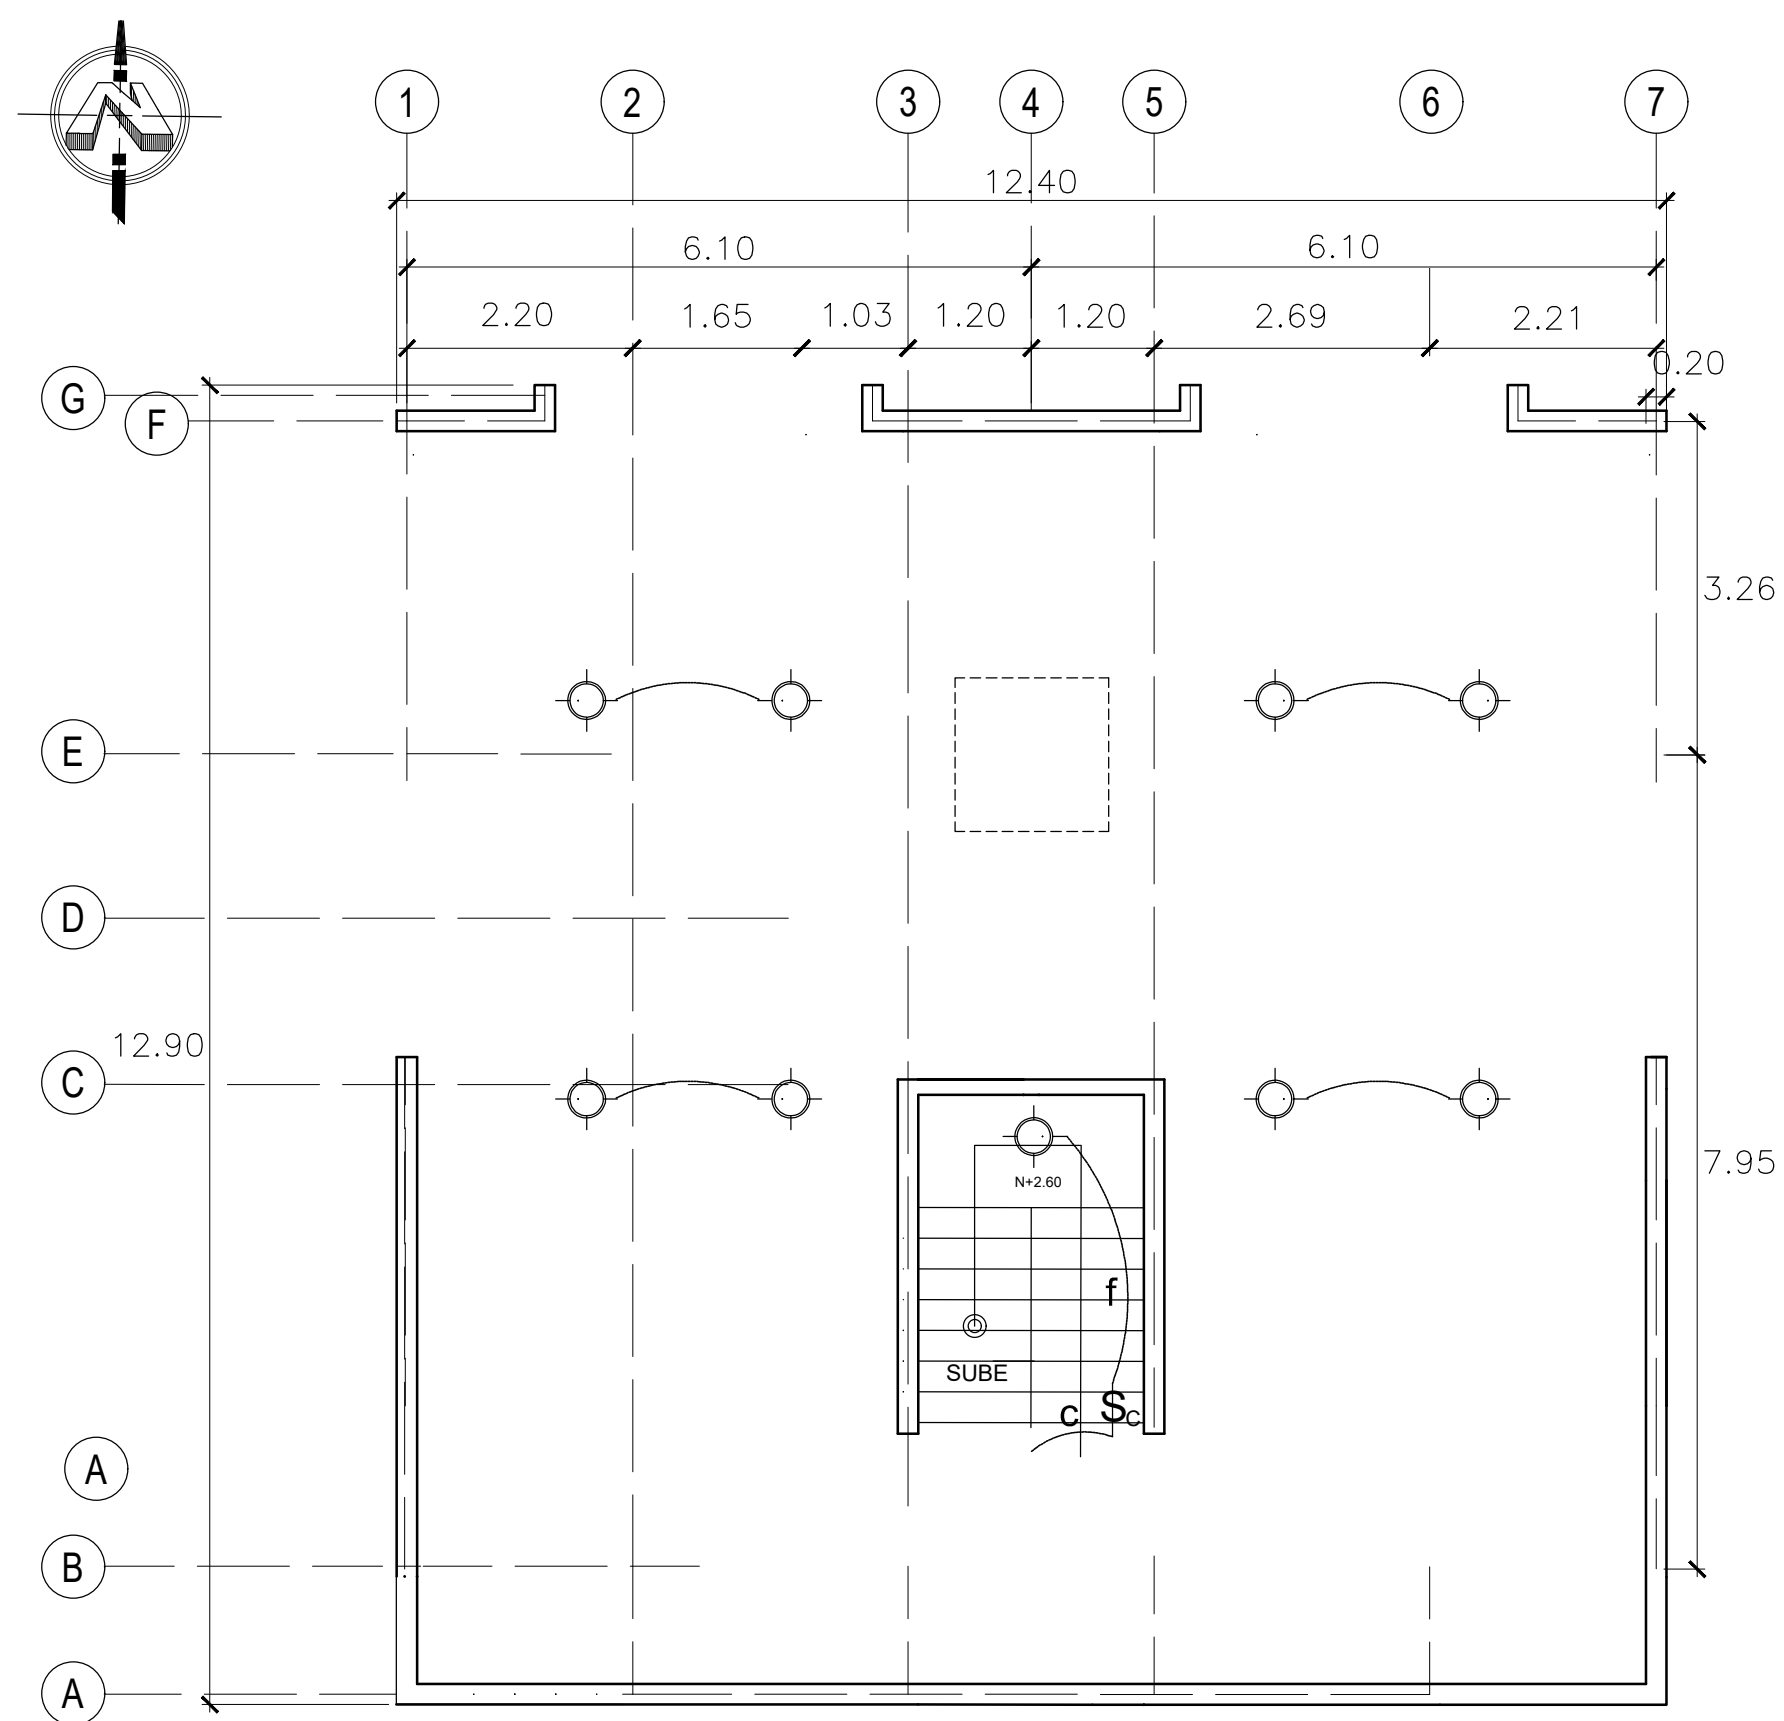


**PLANTA DE INSTALACIONES ELECTRICAS
LUCES E INTERRUPTORES
NIVEL FUNDACION
ESC. 1:75**

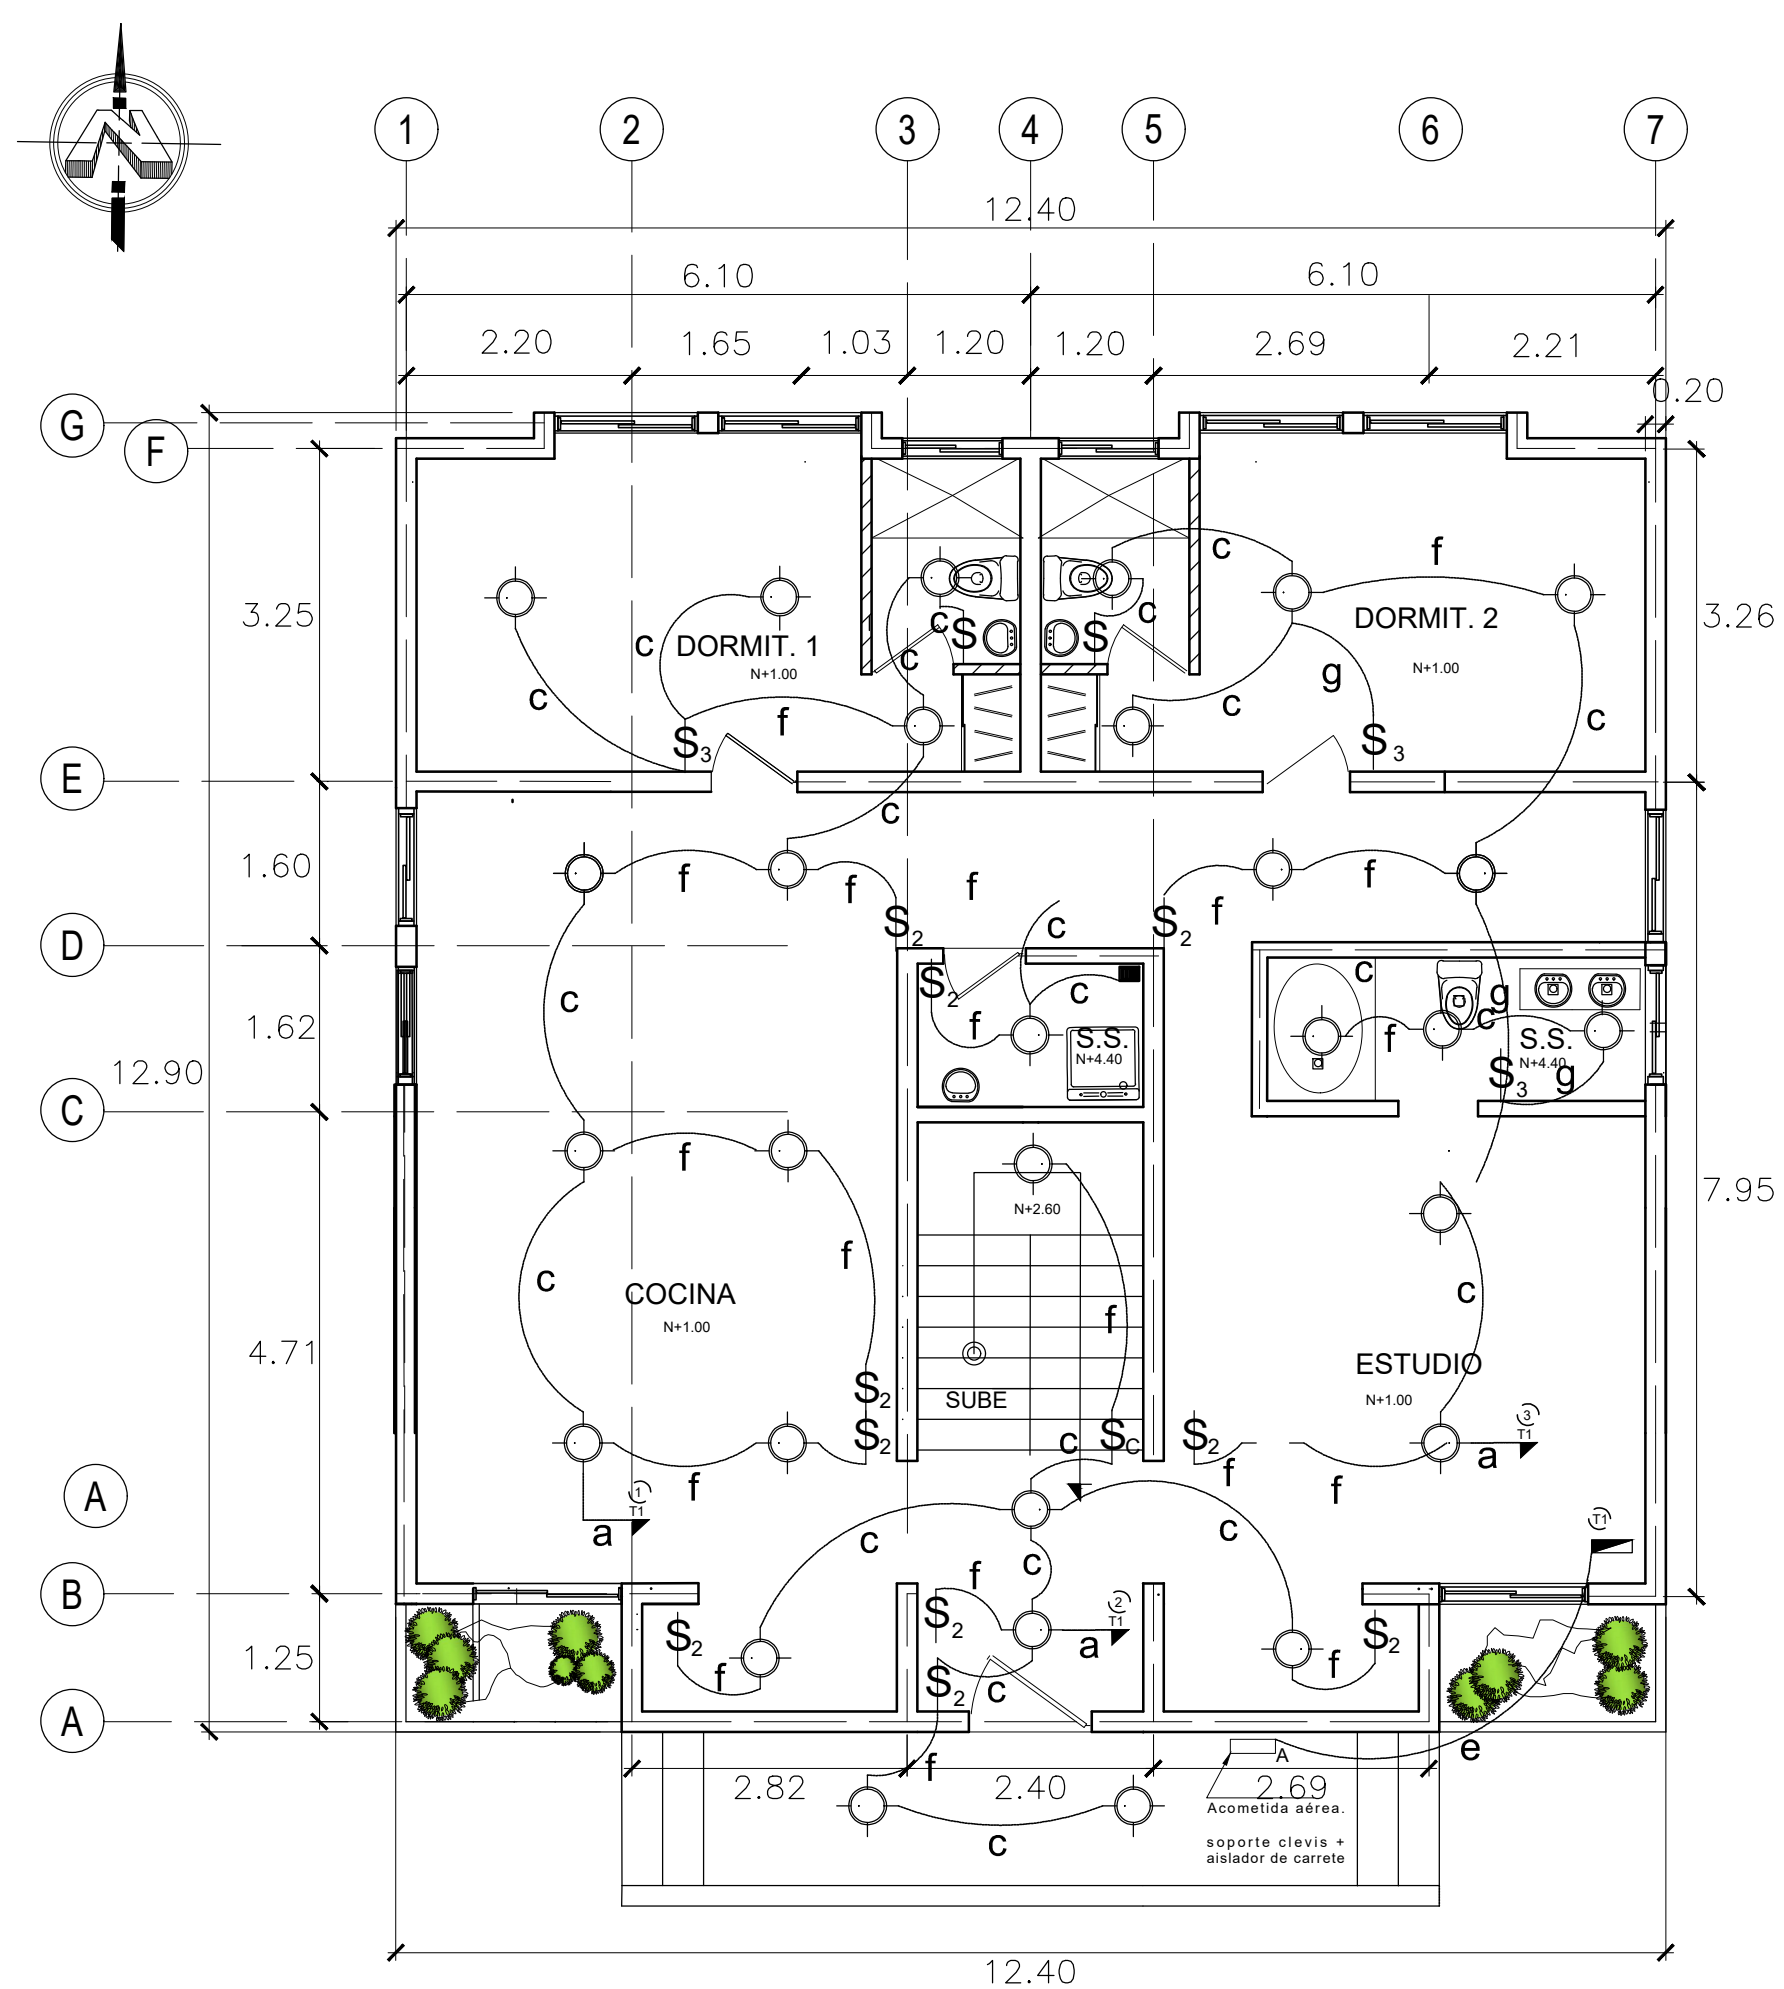

**PLANTA DE INSTALACIONES ELECTRICAS
LUCES E INTERRUPTORES PRIMER NIVEL
ESC. 1:75**

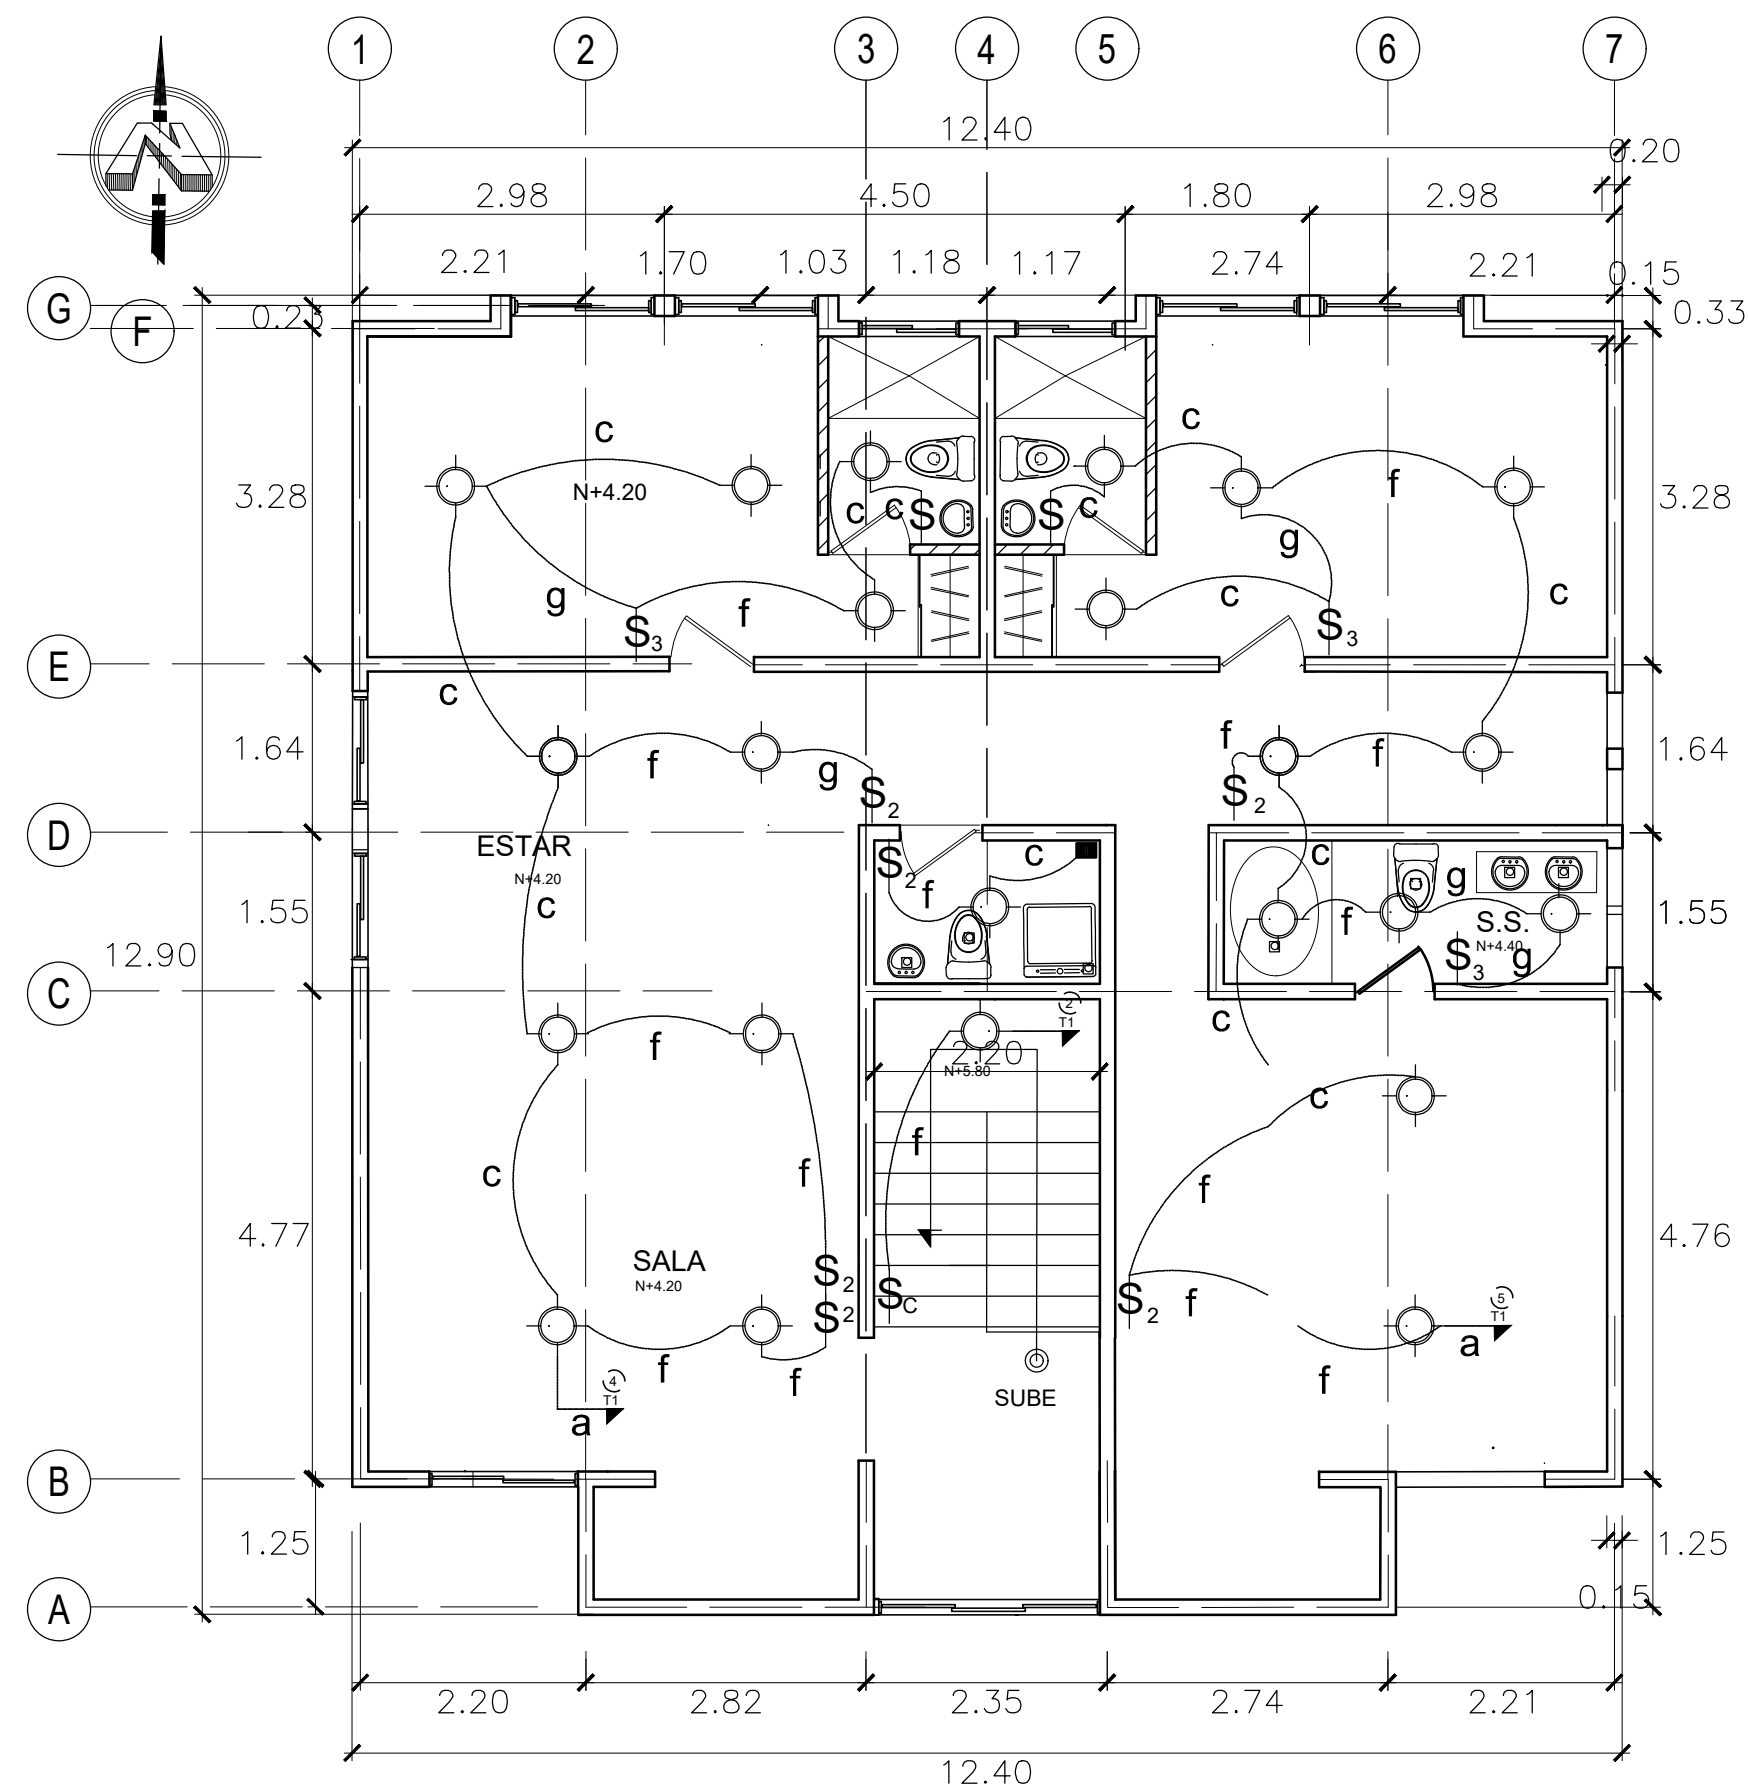

**PLANTA DE INSTALACIONES ELECTRICAS
LUCES E INTERRUPTORES
SEGUNDO NIVEL
ESC. 1:75**

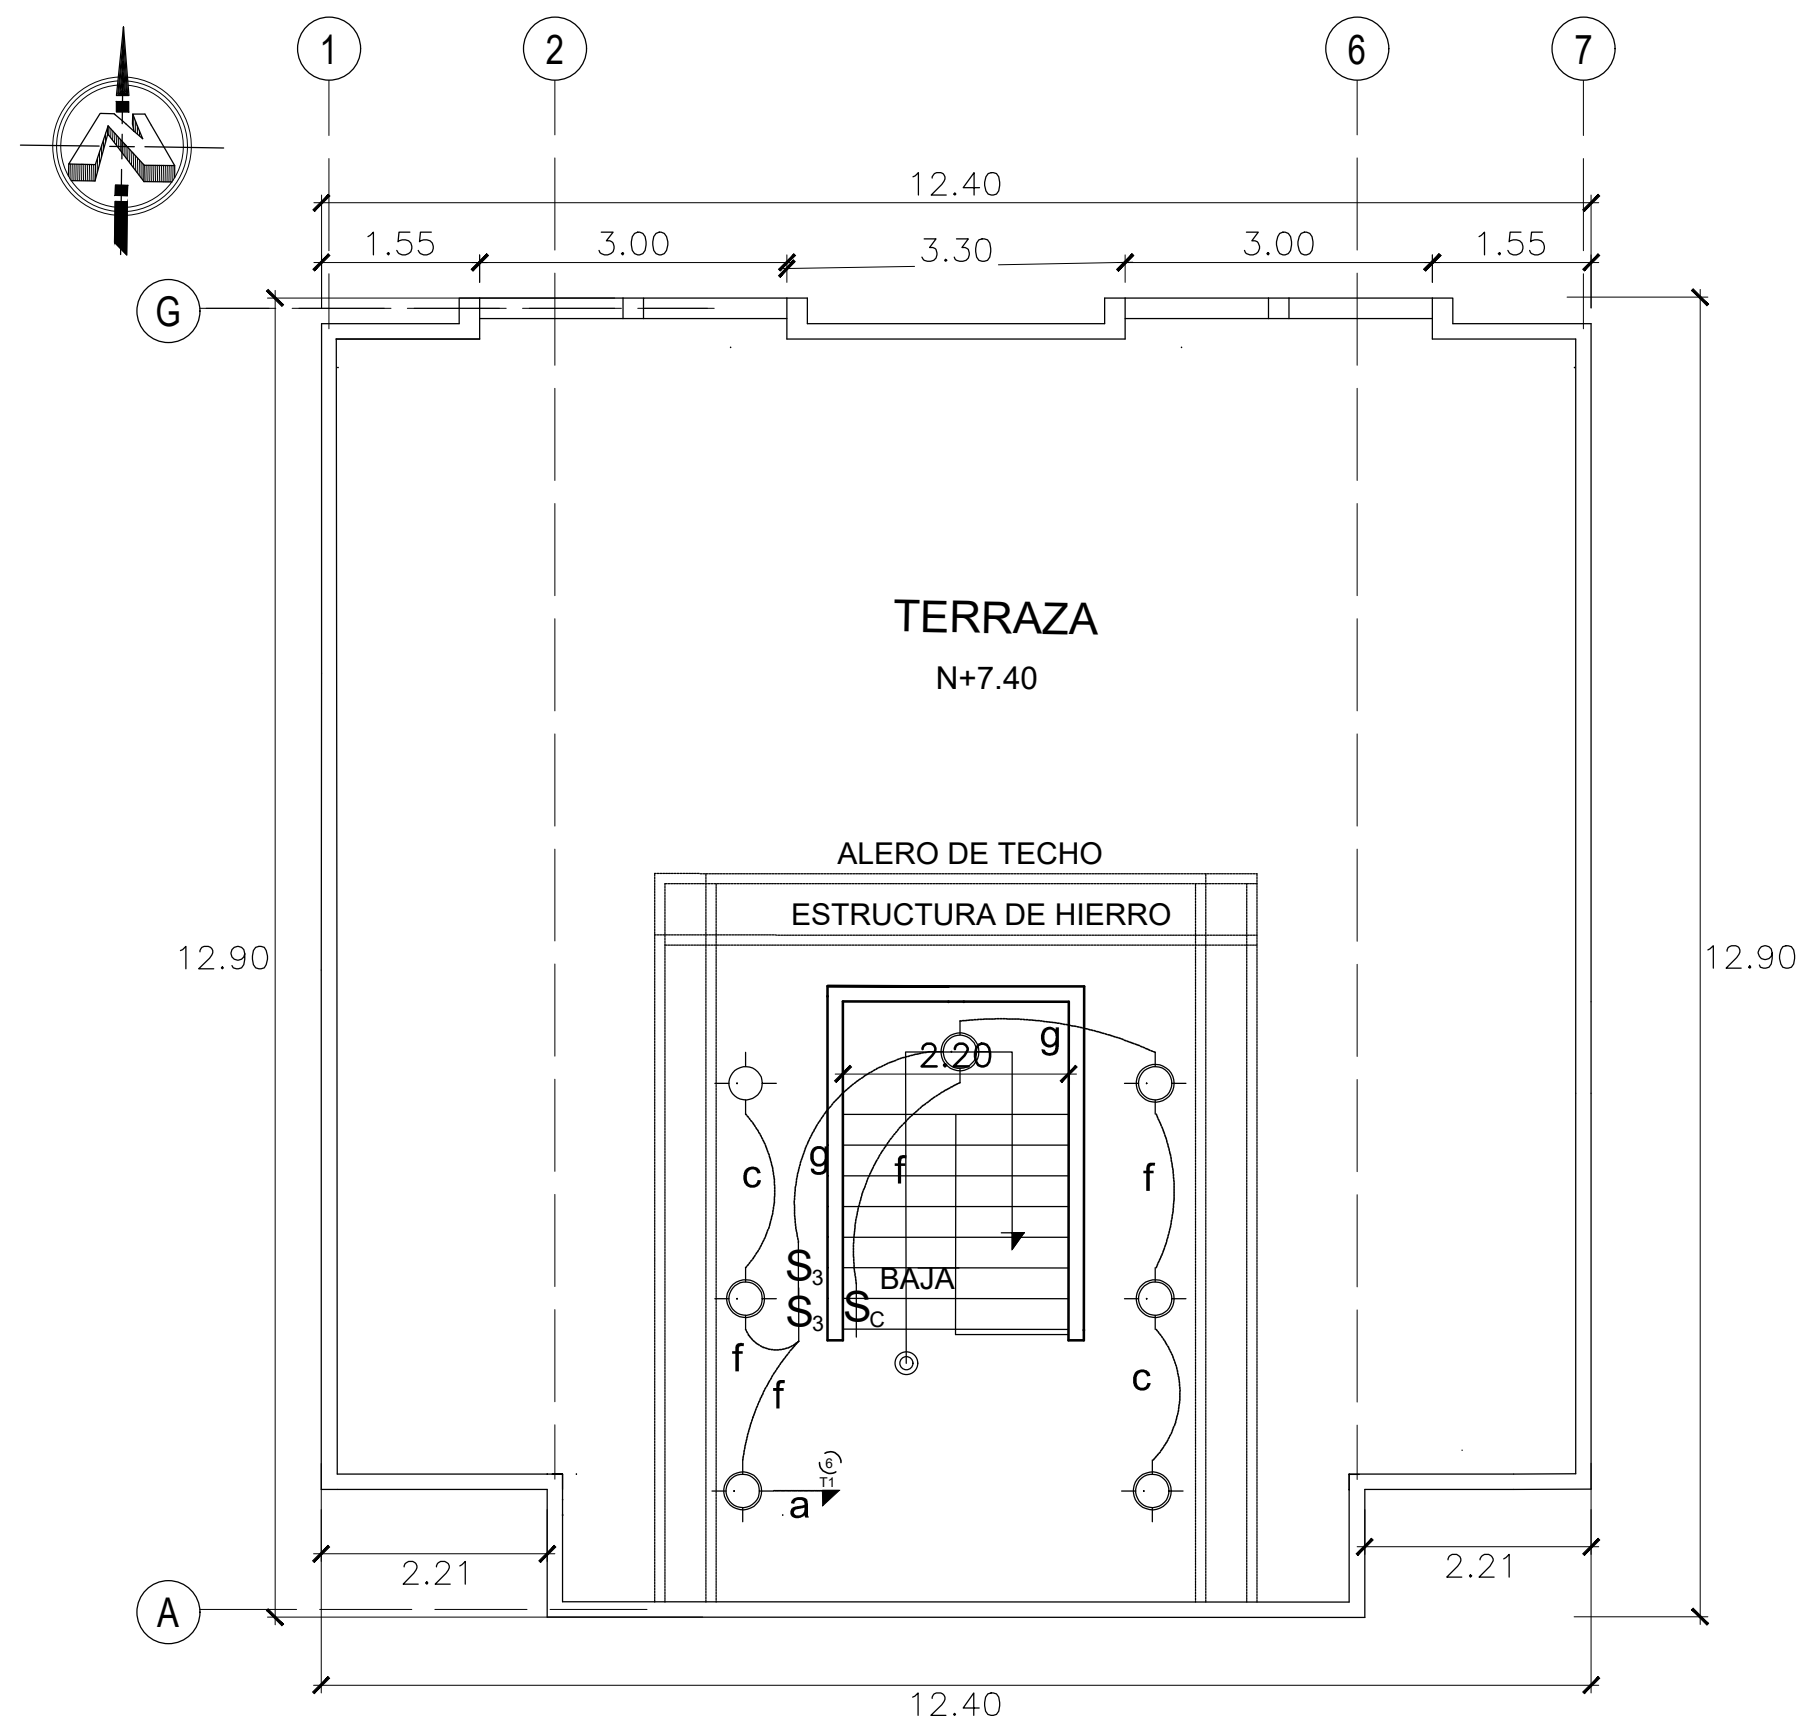

**PLANTA INSTALACIONES ELECTRICAS
LUCES E INTERRUPTORES TERRAZA
ESC. 1:75**



SELLOS DE APROBACION:

ESTE PLANO FORMA PARTE INTEGRAL DE LA RESOLUCION EMITIDA EN FECHA 24 DE JULIO DE 2025 EN FORMATO DIGITAL Y CORRESPONDE AL EXPEDIENTE DE PERMISO DE CONSTRUCCION REFERENCIA 0333-2025. PRESENTADO BAJO LA RESPONSABILIDAD DE LA ARQ MORENA GUADALUPE VASQUEZ LÓPEZ CON REGISTRO PROFESIONAL VMVDU A-4576.

PRESENTA:

ING.. IRVIN RICARDO CABRERA VENTURA

PROYECTO
CONSTRUCCION DE VIVIENDA DE DOS NIVELES
Y TERRAZA EMPRESA AZZUL

PROPIETARIOS
EMPRESA AZZUL S.A DE C.V

UBICACION:
CANTON SAN RAFAEL, CONDOMINIO RECREATIVO, LOMAS DE SAN BLAS, CALLE MAJAHUAL, POLIGONO 6, NUMERO 18, LA LIBERTAD COSTA, DEPARTAMENTO DE LA LIBERTAD

CONTENIDO:

PLANTAS ELECTRICAS
DE LUCES E INTERRUPTORES

ESCALA:
INDICADA

FECHA:
MARZO 2025

HOJA N°:
EL - 01

FIRMA Y SELLO DE PROFESIONALES RESPONSABLES

DISEÑO ARQUITECTÓNICO:
FIRMA:
DISEÑO ARQUITECTÓNICO:
SELLO:


REGISTRO NACIONAL DE ARQUITECTOS E INGENIEROS
CARLA PATRICIA RODRIGUEZ DE CHOCOBAR
A-2339
ARQUITECTA

DIRECTOR DE LA OBRA:
FIRMA:
DIRECTOR DE LA OBRA:
SELLO:


REGISTRO NACIONAL DE ARQUITECTOS E INGENIEROS
CARLOS FRANCISCO CALICIA MAJIA
A-3297
ARQUITECTO

RESPONSABLE DEL TRAMITE:
FIRMA:
RESPONSABLE DEL TRAMITE:
SELLO:


REGISTRO NACIONAL DE ARQUITECTOS E INGENIEROS
Morena Guadalupe Vasquez López
A - 4576
ARQUITECTA

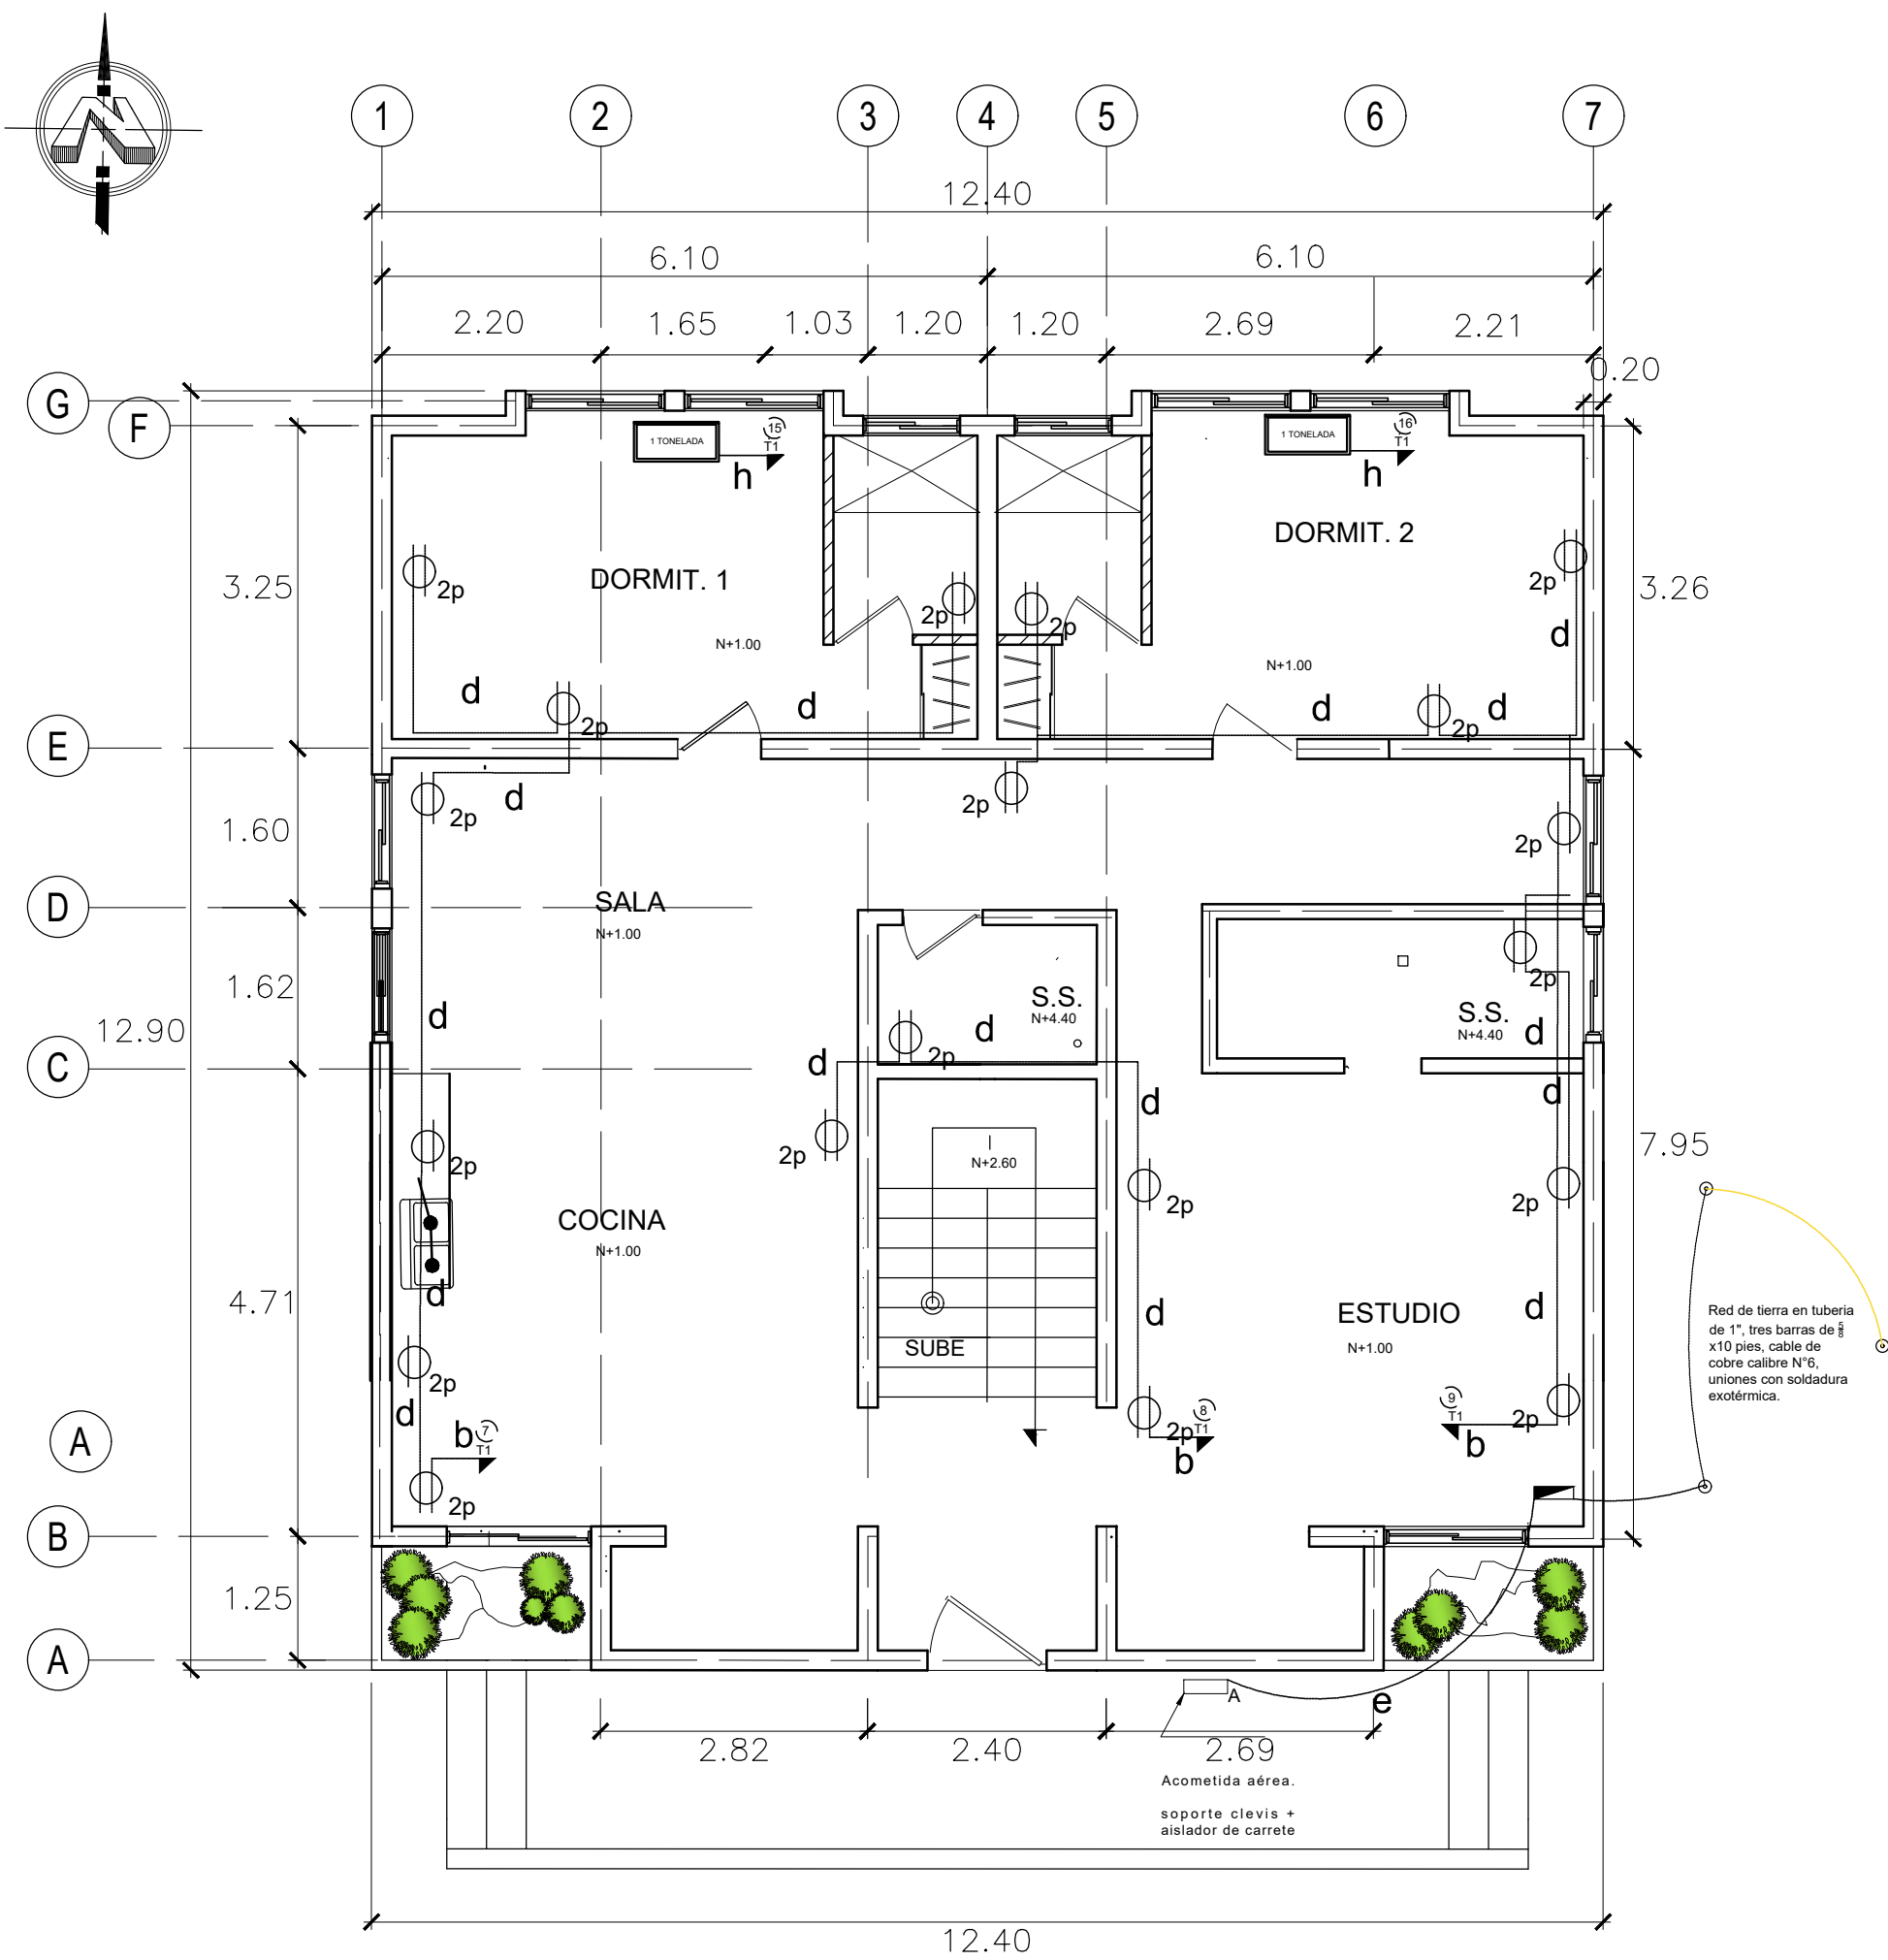

**PLANTA DE INSTALACIONES ELECTRICAS
TOMAS CORRIENTE Y A/C
PRIMER NIVEL
ESC. 1:75**

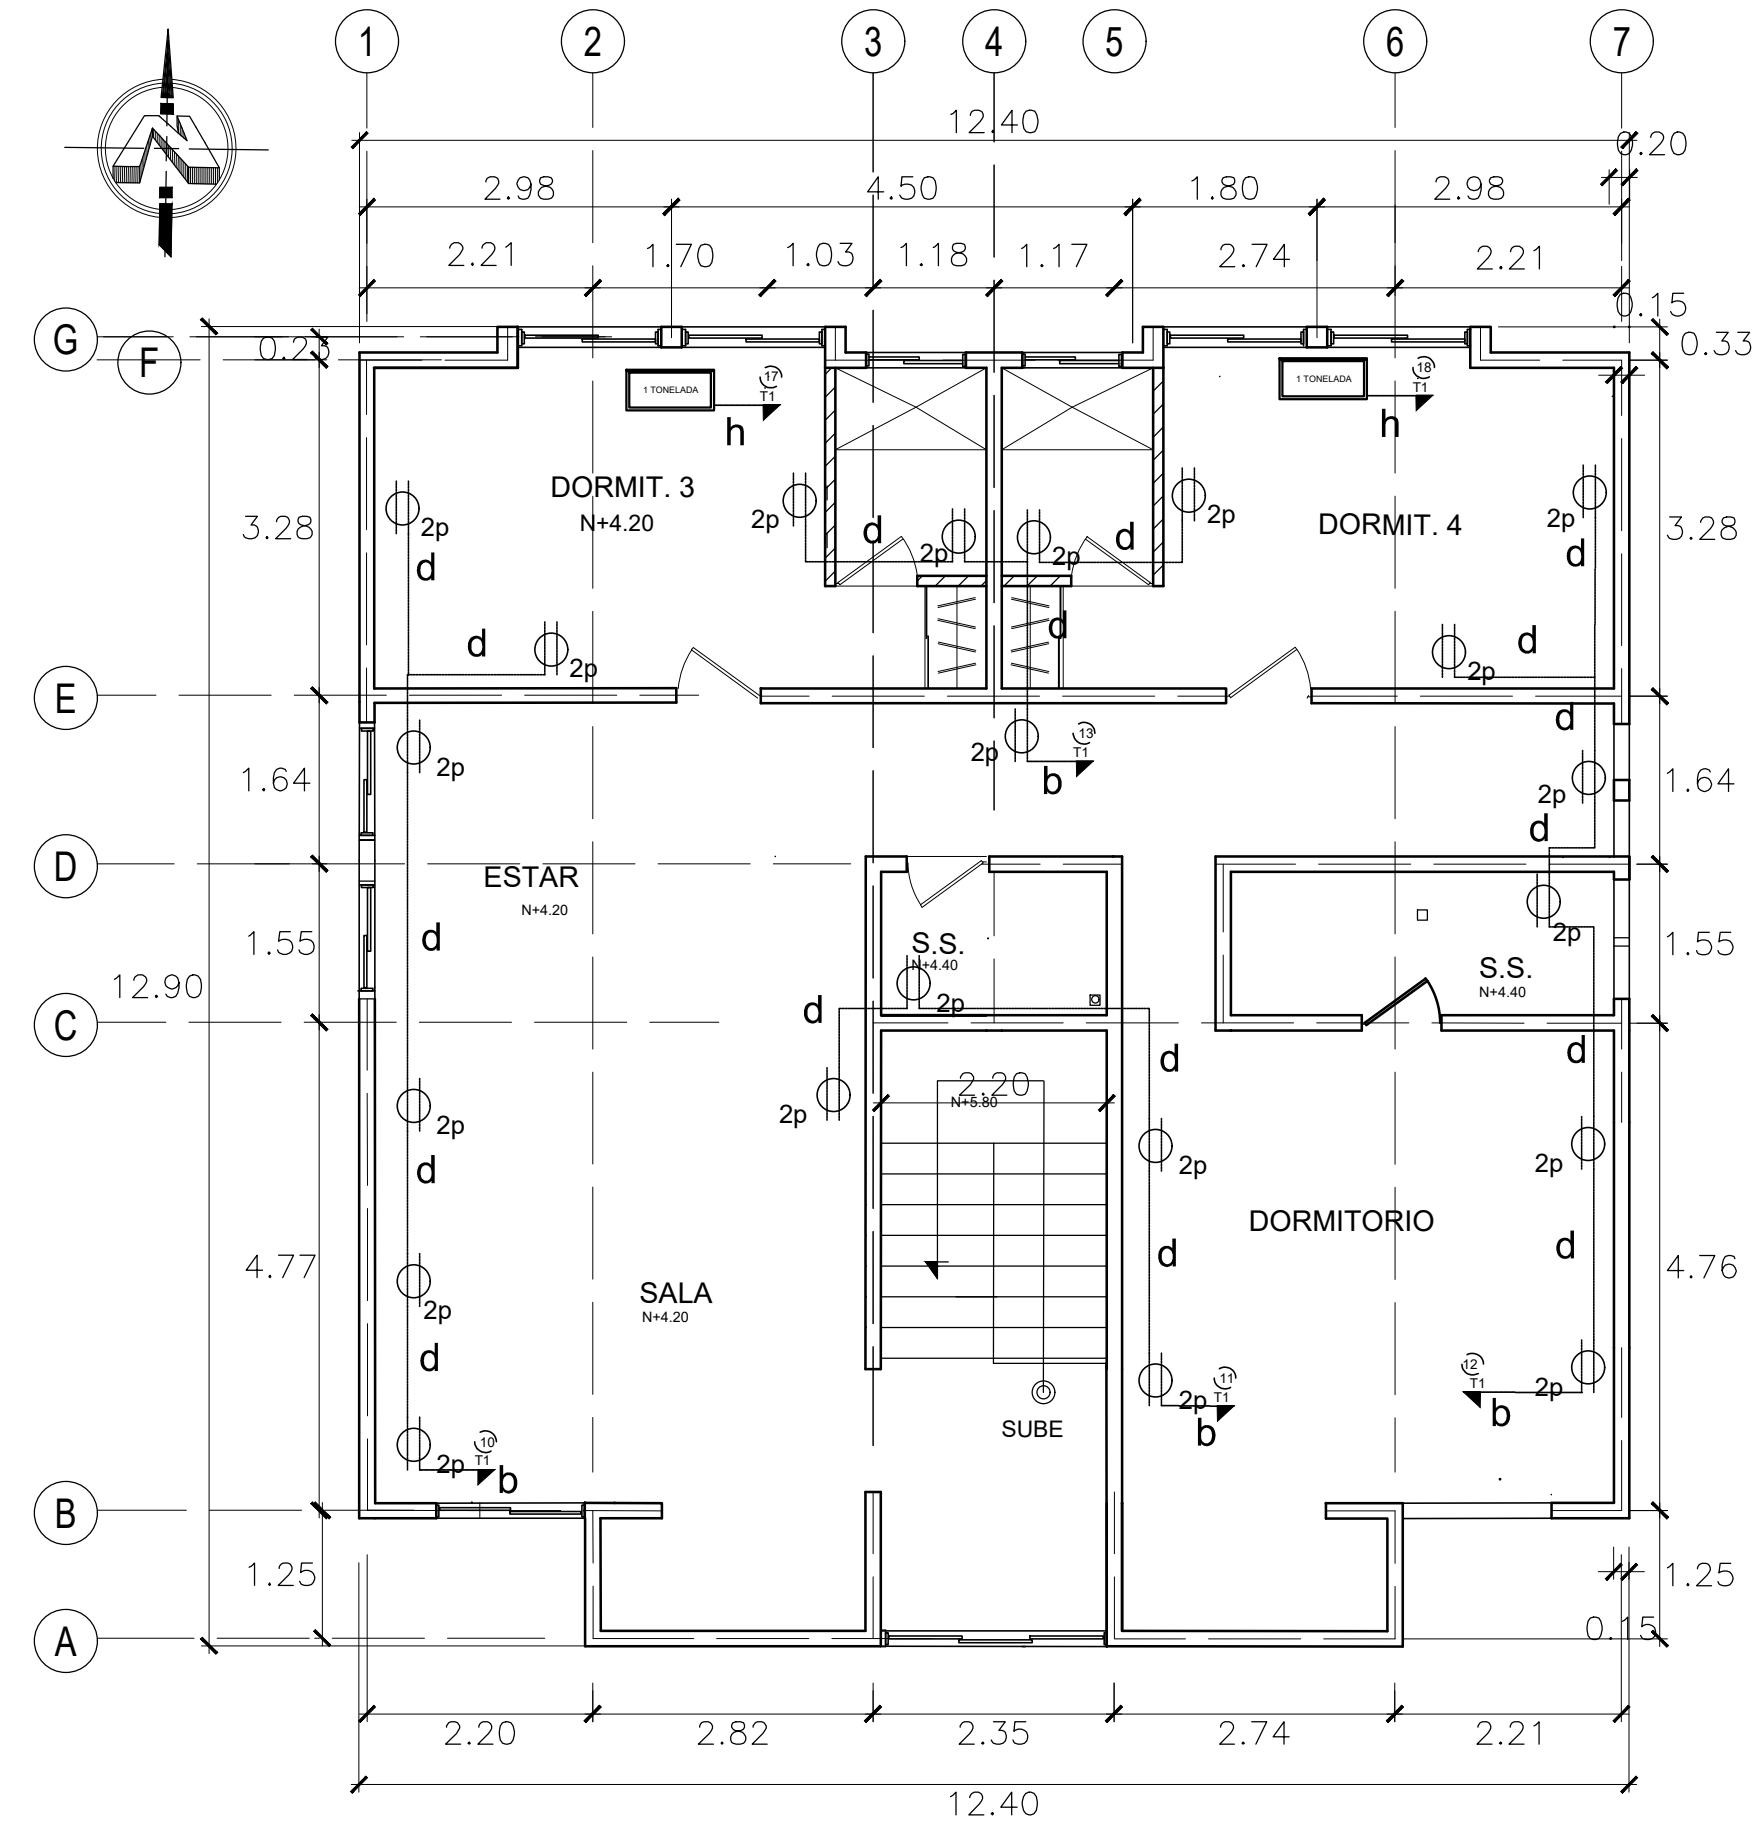

**PLANTA INSTALACIONES ELECTRICAS
TOMAS CORRIENTE Y A/C
SEGUNDO NIVEL
ESC. 1:75**

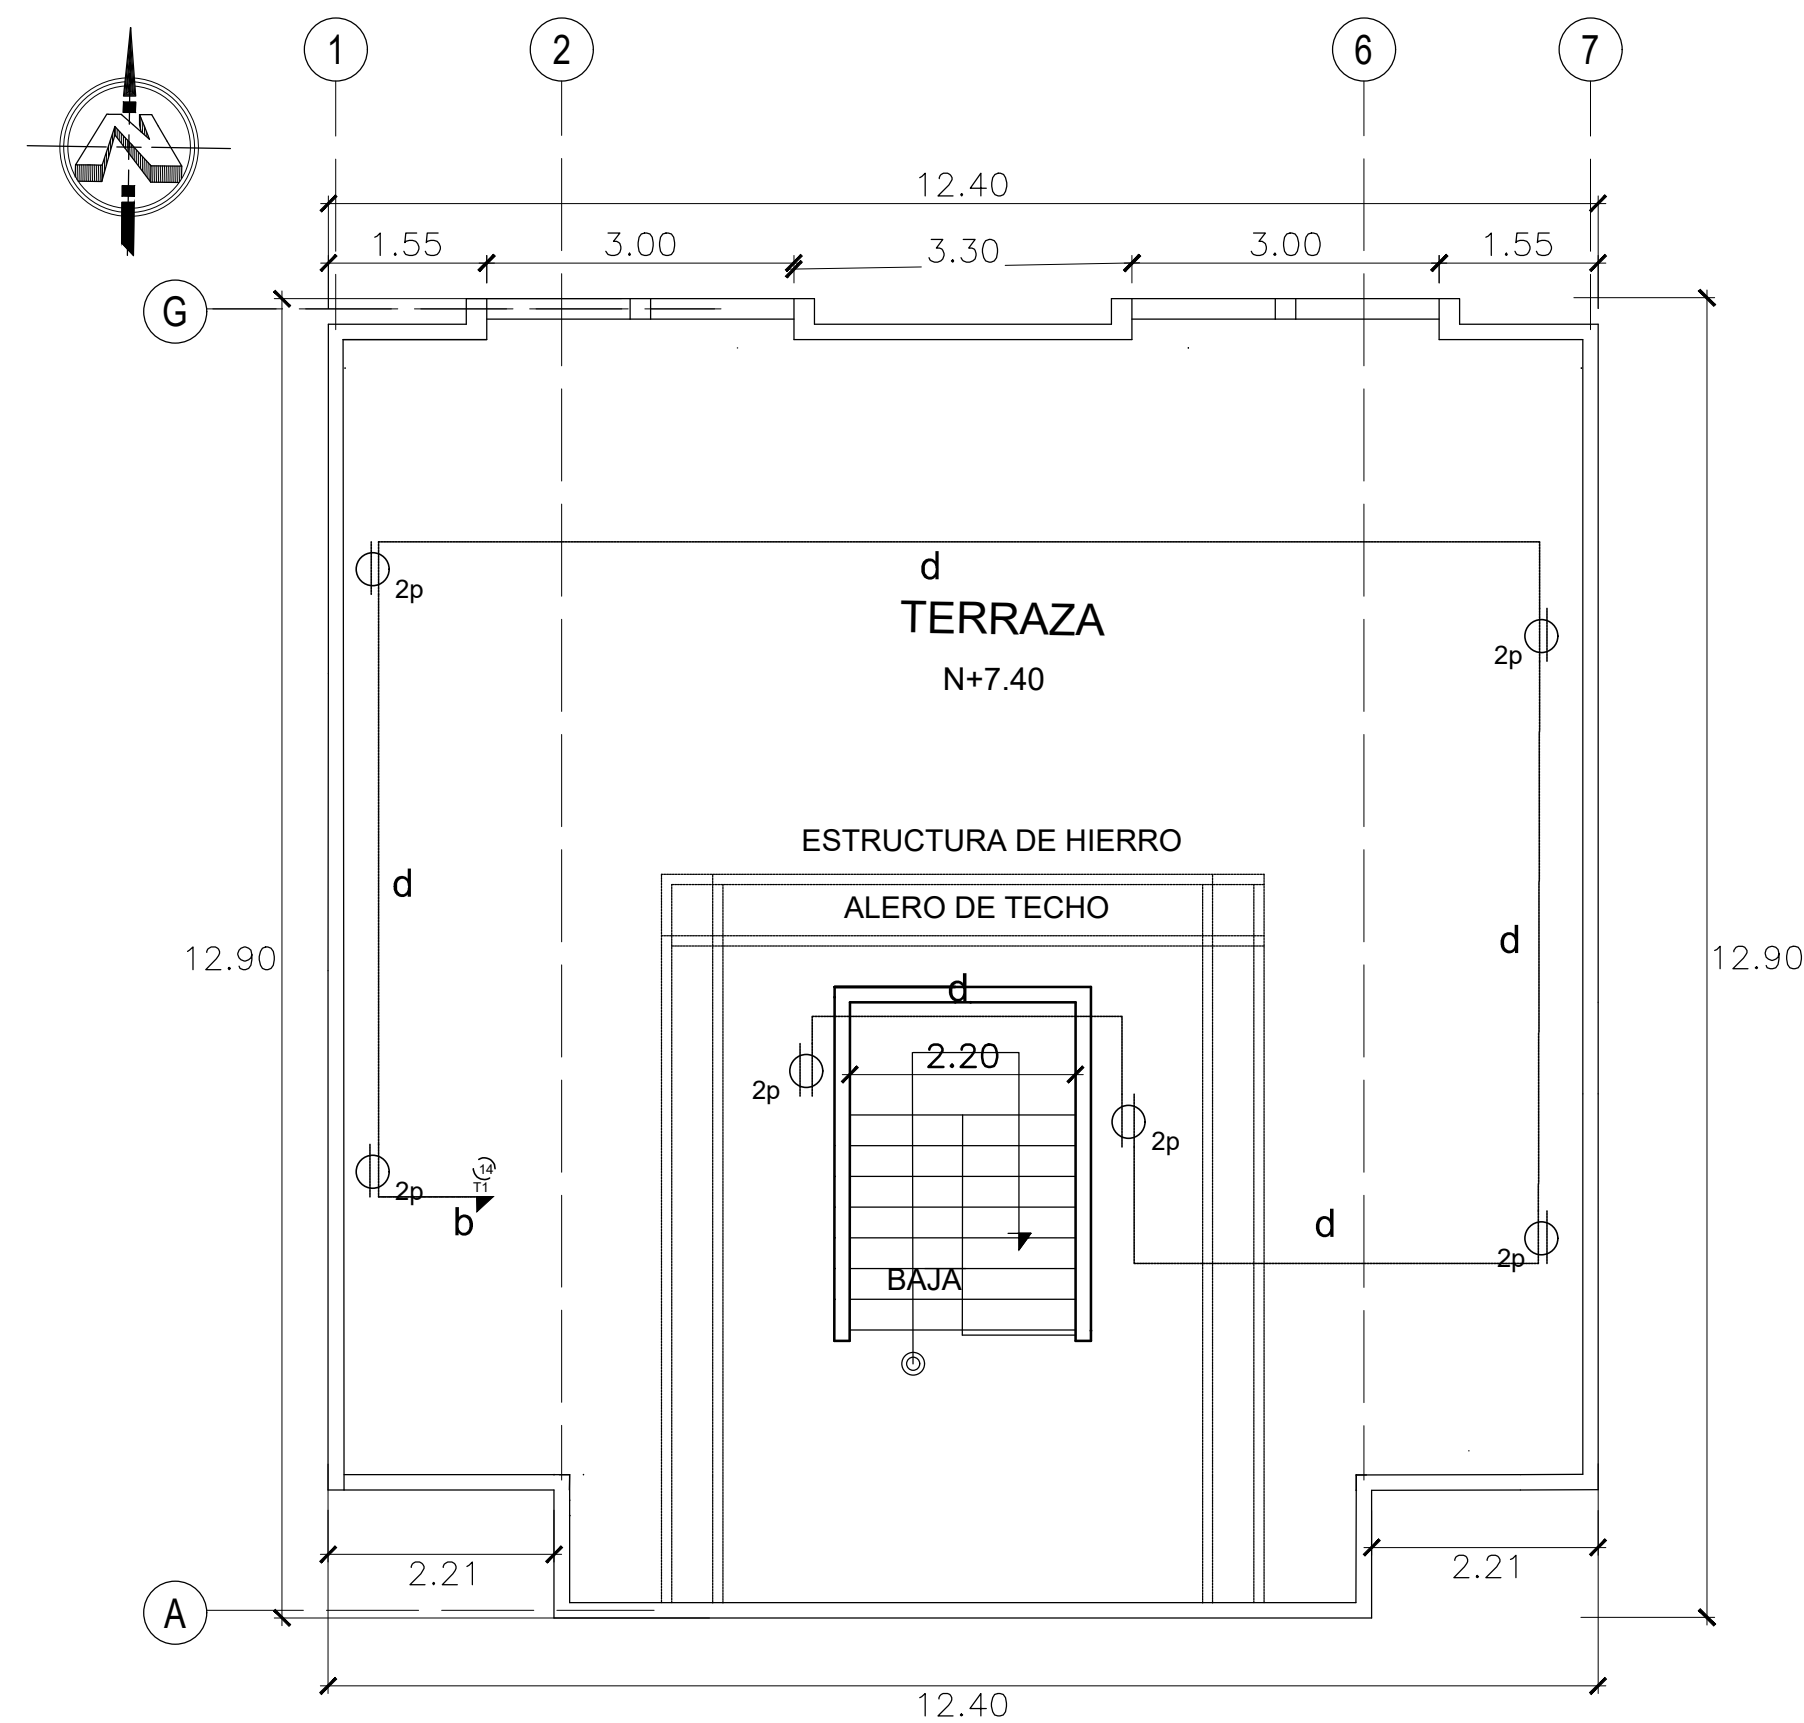

**PLANTA INSTALACIONES ELECTRICAS
TOMAS CORRIENTE TERRAZA**

SELLOS DE APROBACION:

ESTE PLANO FORMA PARTE INTEGRAL DE LA RESOLUCION EMITIDA EN FECHA 24 DE JULIO DE 2025 EN FORMATO DIGITAL Y CORRESPONDE AL EXPEDIENTE DE PERMISO DE CONSTRUCCION REFERENCIA 0333-2025. PRESENTADO BAJO LA RESPONSABILIDAD DE LA ARQ MORENA GUADALUPE VASQUEZ LÓPEZ CON REGISTRO PROFESIONAL VMVDU A-4576.

PRESENTA:

ING.. IRVIN RICARDO CABRERA VENTURA

PROYECTO
CONSTRUCCION DE VIVIENDA DE DOS NIVELES
Y TERRAZA EMPRESA AZZUL
PROPIETARIOS
EMPRESA AZZUL S.A DE C.V
UBICACION:
CANTON SAN RAFAEL, CONDOMINIO RECREATIVO, LOMAS DE SAN BLAS, CALLE
MAJAHUAL, POLIGONO 6, NUMERO 18, LA LIBERTAD COSTA, DEPARTAMENTO DE LA
LIBERTAD

CONTENIDO:
PLANTAS ELECTRICAS
DE TOMACORRIENTES Y AIRES



ESCALA:
INDICADA

FECHA:
MARZO 2025

HOJA N°:
EL - 02

FIRMA Y SELLO DE PROFESIONALES RESPONSABLES

DISEÑO ARQUITECTÓNICO: FIRMA: DISEÑO ARQUITECTÓNICO: SELLO:	DIRECTOR DE LA OBRA: FIRMA: DIRECTOR DE LA OBRA: SELLO:	RESPONSABLE DEL TRAMITE: FIRMA: RESPONSABLE DEL TRAMITE: SELLO:
REGISTRO NACIONAL DE ARQUITECTOS E INGENIEROS CARLA PATRICIA RODRIGUEZ DE CHOCOBAR A-2339 ARQUITECTA	REGISTRO NACIONAL DE ARQUITECTOS E INGENIEROS CARLOS FRANCISCO GALICIA MARIA A-3207 ARQUITECTO	REGISTRO NACIONAL DE ARQUITECTOS E INGENIEROS Morena Guadalupe Vásquez López A-4576 ARQUITECTA

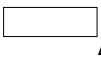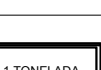CLAVE	DESCRIPCIÓN
 2P	TOMACORRIENTE DOBLE POLARIZADO
 A	ACOMETIDA ELÉCTRICA
	INTERRUPTOR SENCILLO T/DADO TICINO CON SU RESPECTIVA PLACA
	INTERRUPTOR DOBLE T/DADO TICINO CON SU RESPECTIVA PLACA
	TABLERO ELÉCTRICO (SUPERFICIAL).
	INTERRUPTOR TRIPLE T/DADO TICINO CON SU RESPECTIVA PLACA
	EXTRACTOR DE AIRE
	AIRE ACONDICIONADO 1 TONELADA

LEYENDA	DESCRIPCION
a	1 THHN #10 + 1 THHN #12 en tubería de 3/4"
b	1 THHN #10 + 2 THHN #12 en tubería de 3/4"
c	2 THHN # 14 en tubería de 1/2".
d	3 THHN # 12 en tubería de 1/2"
e	3 THHN # 4 en tubería de 1 1/2".
f	3 THHN # 14 en tubería de 1/2".
g	4 THHN # 14 en tubería de 1/2".
h	3 THHN # 10 en tubería de 3/4".

Proyecto: instalaciones eléctricas casa lote #18										
T1										
TABLERO MONOFÁSICO 16 ESPACIOS, BARRAS 125 A. MAIN 70 A 2P				Corriente (A)		PROTECCIÓN	FP	CONDUCTOR THHN	CANALIZACIÓN FLEXIBLE	DESCRIPCIÓN DE LA CARGA
No. Circuito	ESPACIOS	Carga en Watts	Voltaje	A	B					
1	1	236	120	2.46		15A 1P	0.80	1 AWG #10 + 1 AWG #12	3/4 "	12 luminarias led 18W + 1 extractor 20W primer nivel
2	3	162	120	1.69		15A 1P	0.80	1 AWG #10 + 1 AWG #12	3/4 "	9 luminarias led de 18W primer nivel
3	5	216	120	2.25		15A 1P	0.80	1 AWG #10 + 1 AWG #12	3/4 "	12 luminarias led de 18W primer nivel
4	2	236	120		2.46	15A 1P	0.80	1 AWG #10 + 1 AWG #12	3/4 "	12 luminarias led 18W + 1 extractor 20W segundo nivel
5	4	234	120		2.44	15A 1P	0.80	1 AWG #10 + 1 AWG #12	3/4 "	13 luminarias led de 18W segundo nivel
6	6	126	120		1.31	15A 1P	0.80	1 AWG #10 + 1 AWG #12	3/4 "	7 luminarias led de 18W terraza
7	7	1,400	120	14.58		20A 1P	0.80	1 AWG #10 + 2 AWG #12	3/4 "	7 tomacorrientes dobles polarizados primer nivel
8	8	800	120		8.33	20A 1P	0.80	1 AWG #10 + 2 AWG #12	3/4 "	4 tomacorrientes dobles polarizados primer nivel
9	9	1,400	120	14.58		20A 1P	0.80	1 AWG #10 + 2 AWG #12	3/4 "	7 tomacorrientes dobles polarizados primer nivel
10	10	1,200	120		12.50	20A 1P	0.80	1 AWG #10 + 2 AWG #12	3/4 "	6 tomacorrientes dobles polarizados segundo nivel
11	11	800	120	8.33		20A 1P	0.80	1 AWG #10 + 2 AWG #12	3/4 "	4 tomacorrientes dobles polarizados segundo nivel
12	12	1,200	120		12.50	20A 1P	0.80	1 AWG #10 + 2 AWG #12	3/4 "	6 tomacorrientes dobles polarizados segundo nivel
13	13	1,000	120	10.42		20A 1P	0.80	1 AWG #10 + 2 AWG #12	3/4 "	5 tomacorrientes dobles polarizados segundo nivel
14	14	1,200	120		12.50	20A 1P	0.80	1 AWG #10 + 2 AWG #12	3/4 "	6 tomacorrientes dobles polarizados terraza
POTENCIA INSTALADA KW		10,210		54	52	ALIMENTADOR: 3 THHN #6 (2F+N) EN TUBERÍA DE ø 1 1/4"				
FACTOR DEMANDA		0.8								
DEMANDA ESPERADA KW		8,168								

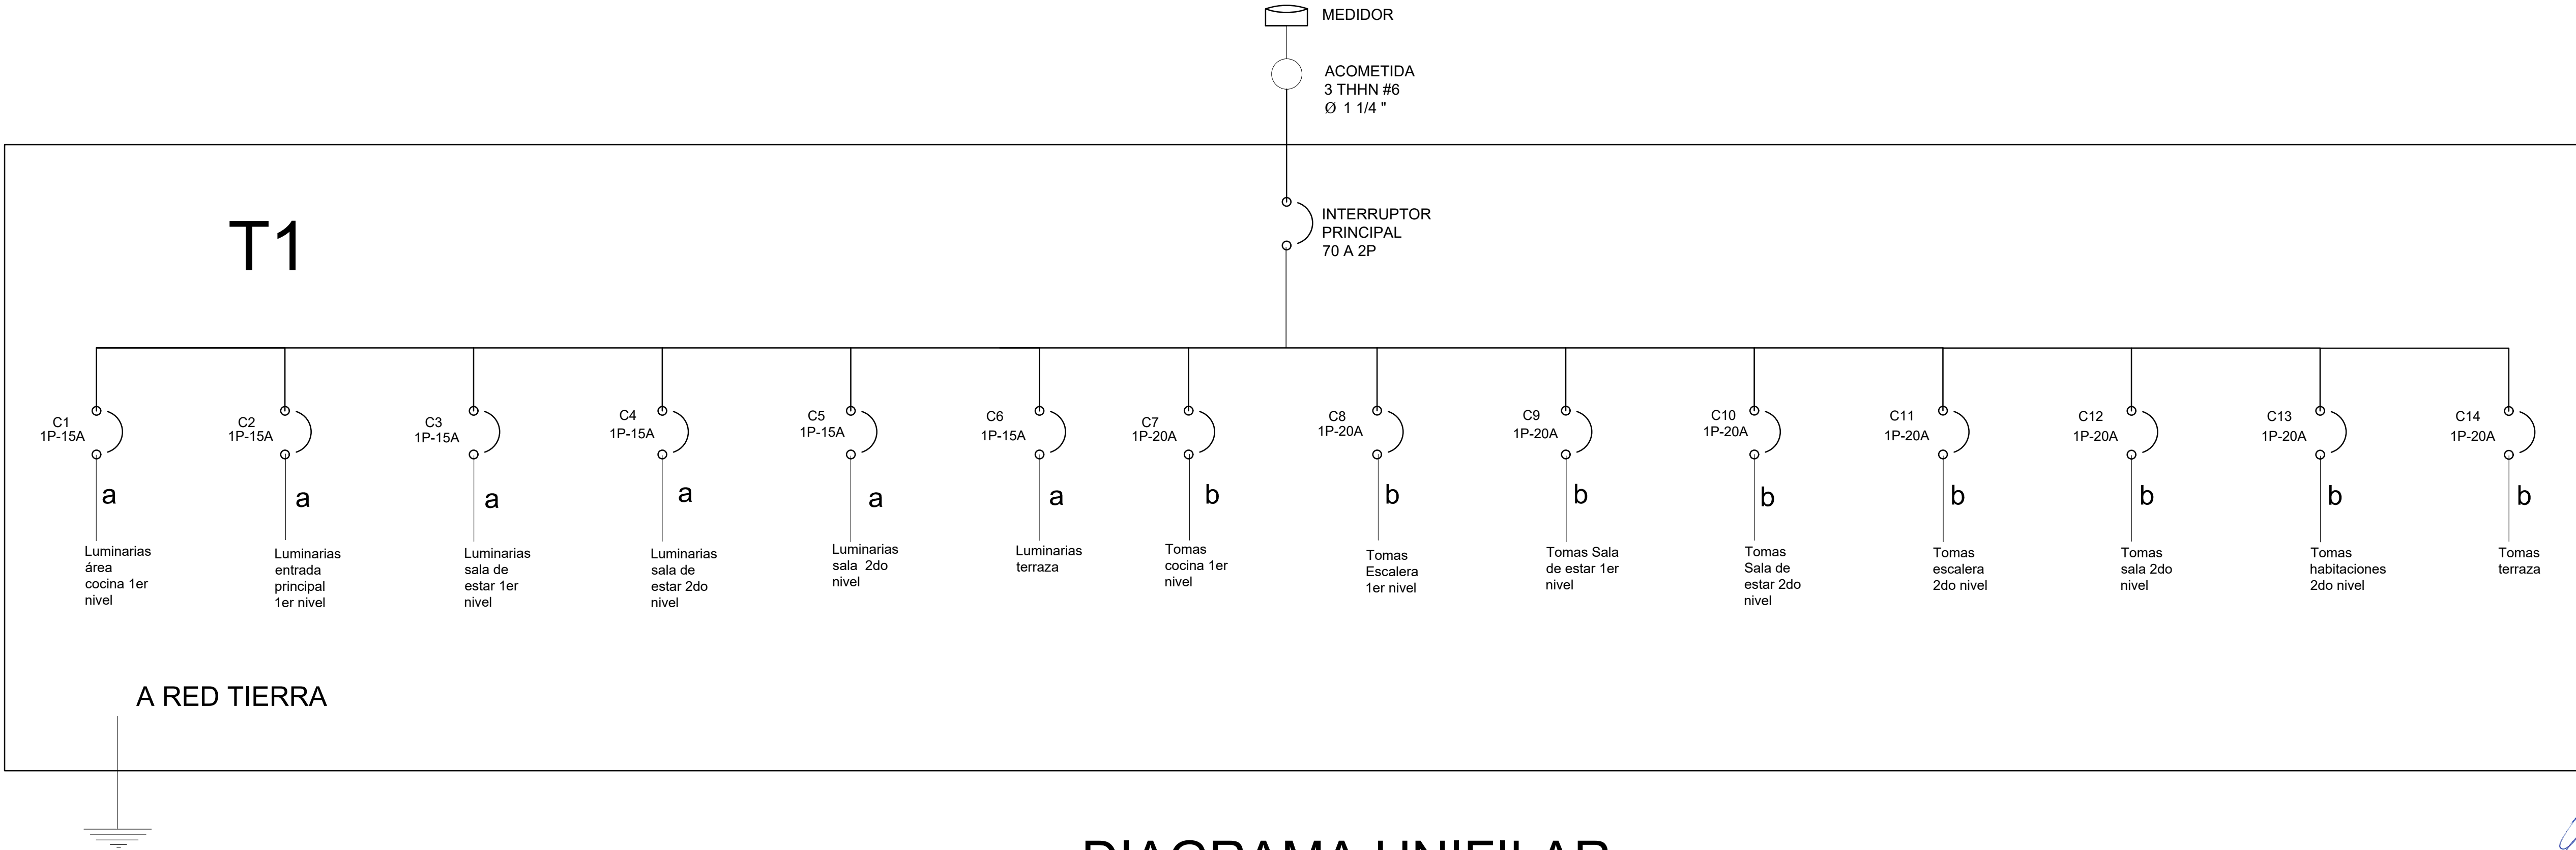


DIAGRAMA UNIFILAR

SELLOS DE APROBACION:

ESTE PLANO FORMA PARTE INTEGRAL DE LA RESOLUCION EMITIDA EN FECHA 24 DE JULIO DE 2025 EN FORMATO DIGITAL Y CORRESPONDE AL EXPEDIENTE DE PERMISO DE CONSTRUCCION REFERENCIA 0333-2025. PRESENTADO BAJO LA RESPONSABILIDAD DE LA ARQ MORENA GUADALUPE VÁSQUEZ LÓPEZ CON REGISTRO PROFESIONAL VMVDU A-4576.

PRESENTA:

ING.. IRVIN RICARDO CABRERA VENTURA

PROYECTO
CONSTRUCCION DE VIVIENDA DE DOS NIVELES Y TERRAZA EMPRESA AZZUL

PROPIETARIOS
EMPRESA AZZUL S.A DE C.V

UBICACION:
CANTON SAN RAFAEL, CONDOMINIO RECREATIVO, LOMAS DE SAN BLAS, CALLE MAJAHUAL, POLIGONO 6, NUMERO 18, LA LIBERTAD COSTA, DEPARTAMENTO DE LA LIBERTAD


CONTENIDO:
CUADRO DE CARGAS
CUADRO DE LEYENDA DE CABLEADO ELECTRICO
DIAGRAMA UNIFILAR


ESCALA:
INDICADA


FECHA:
MARZO 2025


HOJA Nº:
EL - 03

FIRMA Y SELLO DE PROFESIONALES RESPONSABLES

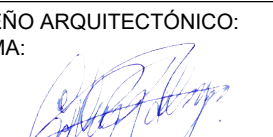DISEÑO ARQUITECTÓNICO:
FIRMA:

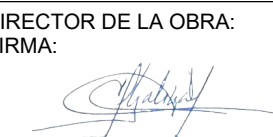DISEÑO ARQUITECTÓNICO:
SELLO:

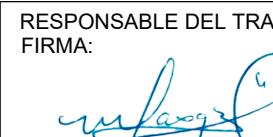
DIRECTOR DE LA OBRA:
FIRMA:

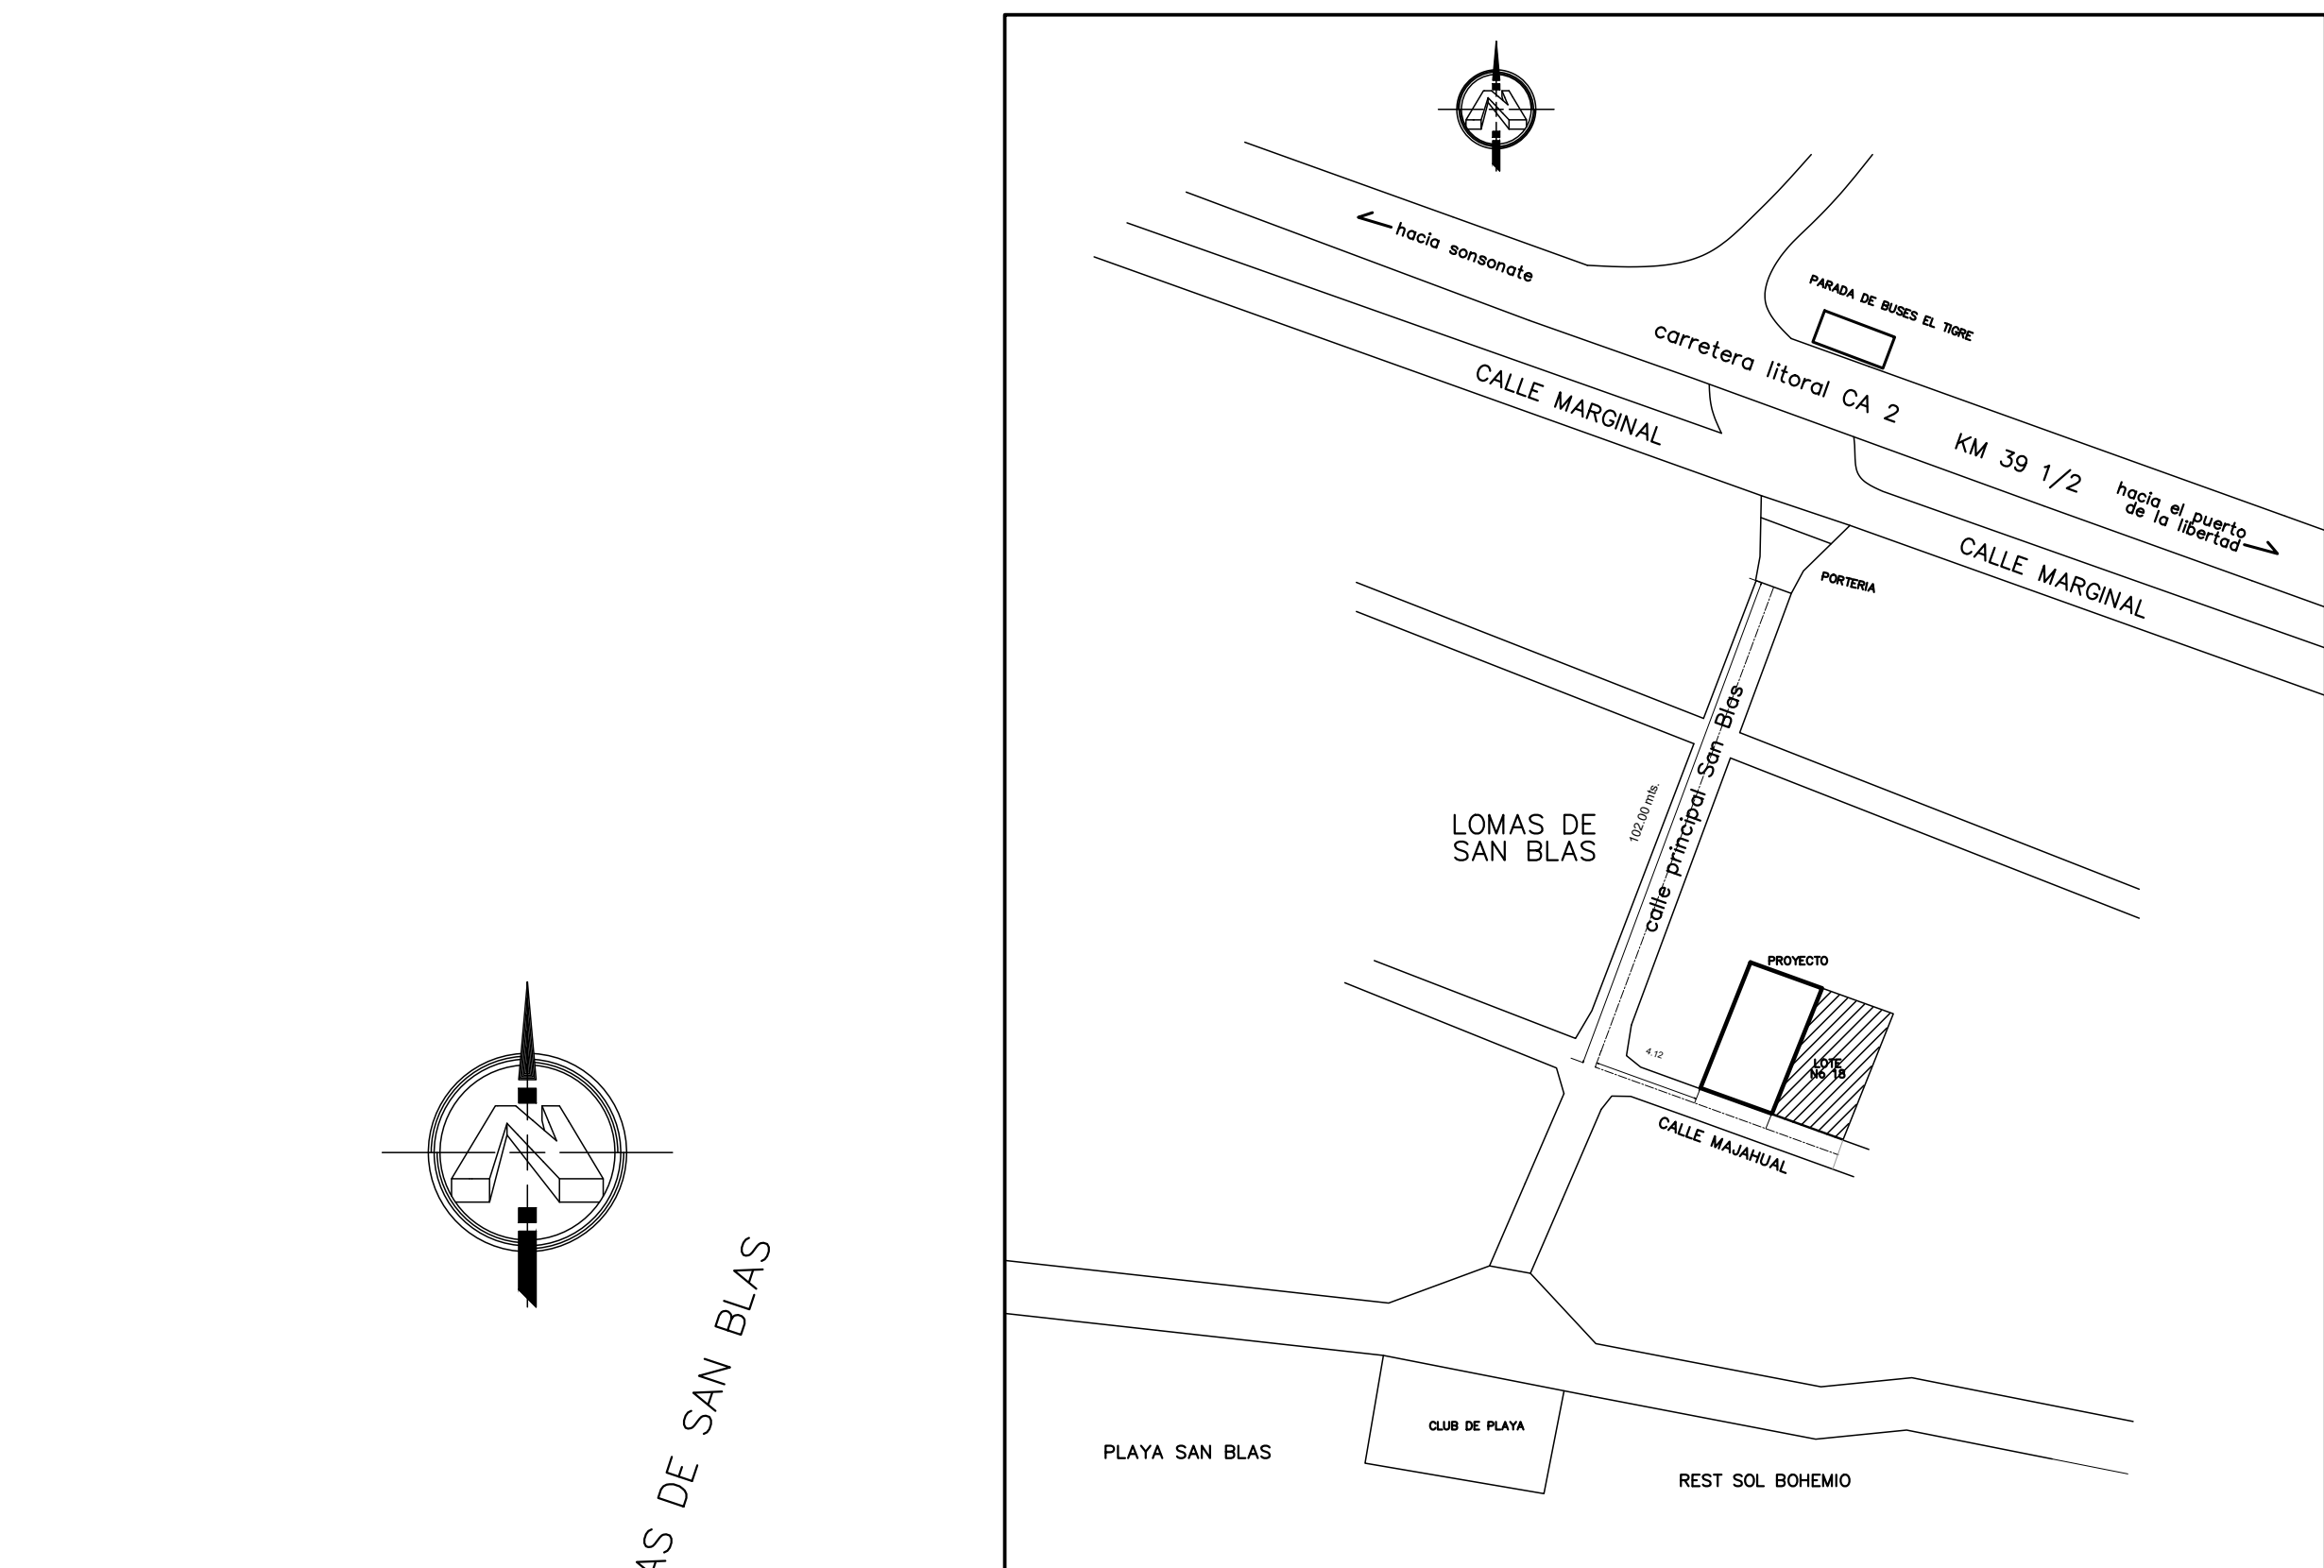DIRECTOR DE LA OBRA:
SELLO:


RESPONSABLE DEL TRAMITE:
FIRMA:

RESPONSABLE DEL TRAMITE:
SELLO:


ESQUEMA DE UBICACION
SIN ESCALA

PARCELA 2017 CUADRO DE RUMBOS Y DISTANCIAS		
MOJON	RUMBO	DISTANCIA
1 - 2	N 22° 09' 06" E	26.00
2 - 3	N 67° 42' 41" W	14.80
3 - 4	S 22° 09' 06" W	25.95
4 - 1	S 67° 35' 10" E	14.80
AREA = 384.30 m²		

SIMBOLOGIA TIPO LINDEROS Y OTROS DETALLES	
Cf. Cv.	cercos fijos cercos vivos
pd Tp. Mu.	Pared tapial muro mamposteria
Mo.No.	Mojon-No. principal
X= Y=	Coordenada de longitud Coordenada de latitud
Pig. Bm.	Puntos topograficos Banco de marcas
pee ppee	poste energia electrica poste principal energia electrica
ptel	poste con transformador
	poste de telefono
	poste de luminaria
cap	caja de agua potable
ct.	caja tragante A.L.L.
	arbol puntos de referencia

SELLOS DE APROBACION:

ESTE PLANO FORMA PARTE INTEGRAL DE LA RESOLUCION EMITIDA EN FECHA 24 DE JULIO DE 2025 EN FORMATO DIGITAL Y CORRESPONDE AL EXPEDIENTE DE PERMISO DE CONSTRUCCION REFERENCIA 0333-2025. PRESENTADO BAJO LA RESPONSABILIDAD DE LA ARQ. MORENA GUADALUPE VASQUEZ LOPEZ CON REGISTRO PROFESIONAL VMVDU A-4576.

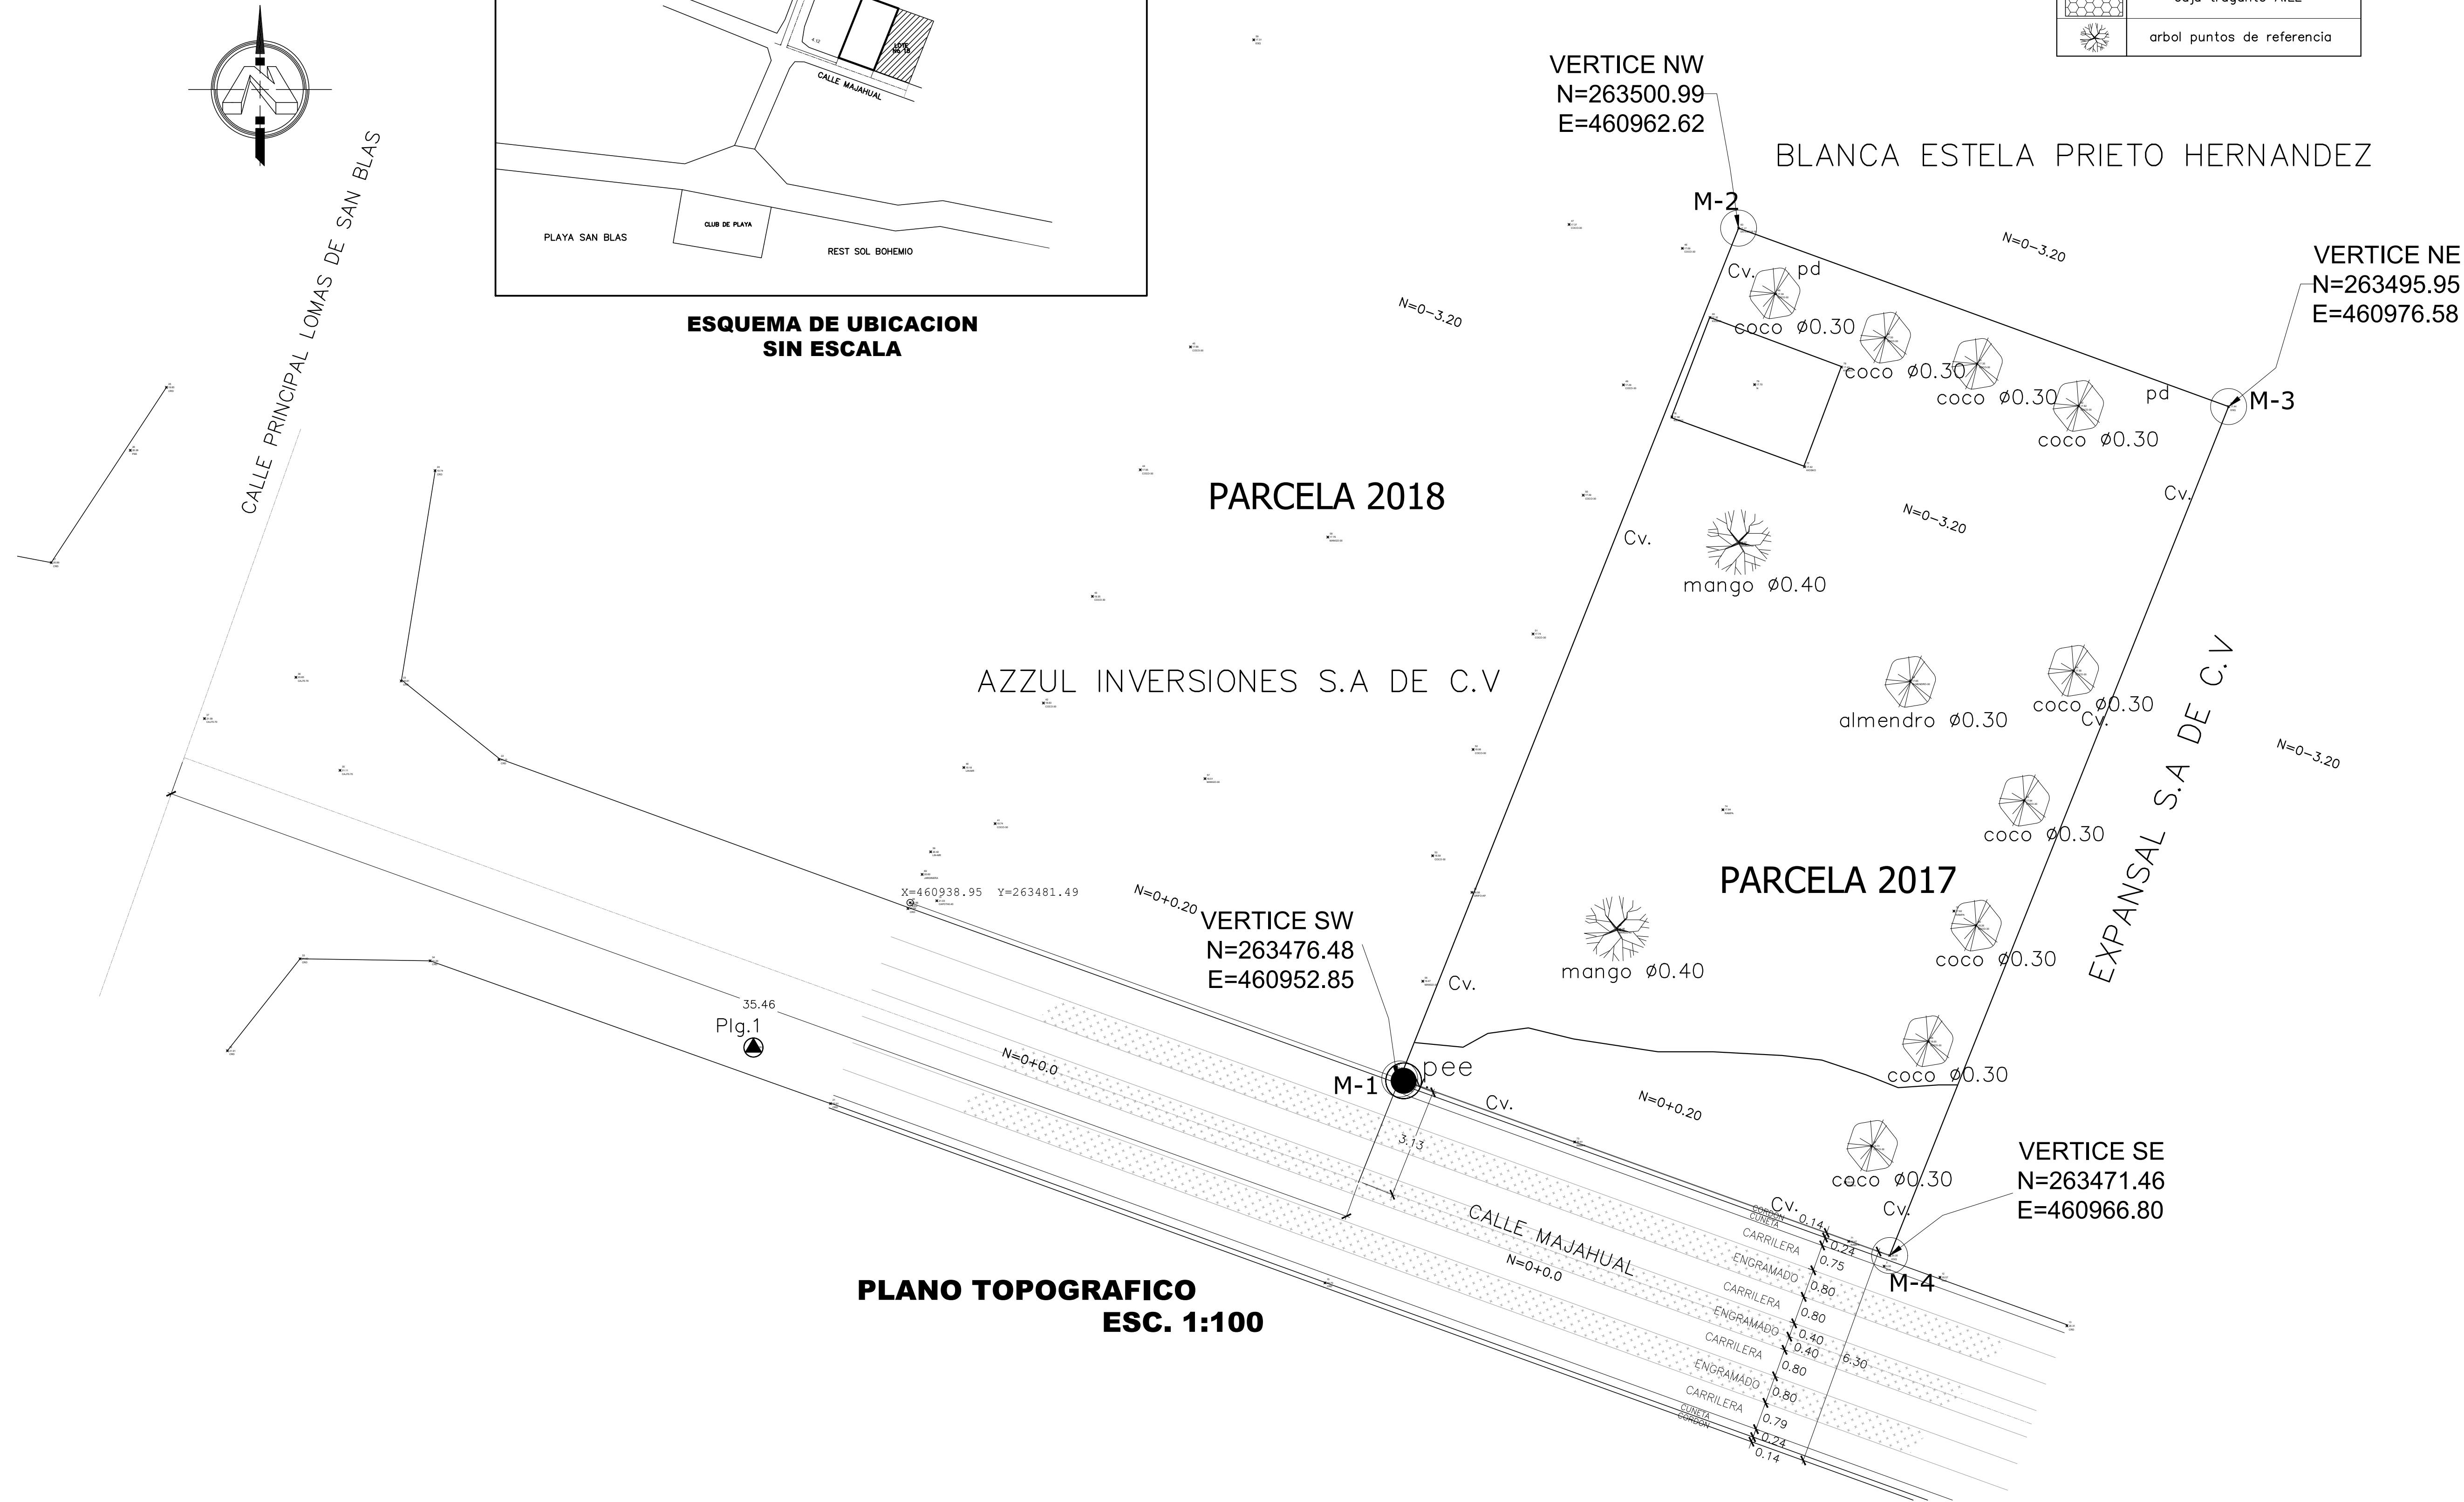

PLANO TOPOGRAFICO
ESC. 1:100

PRESENTA:

ARQ. KARLA RODRIGUEZ DE CHOCOBAR

PROYECTO
CONSTRUCCION DE VIVIENDA DE DOS NIVELES
Y TERRAZA EMPRESA AZZUL

PROPIETARIOS
EMPRESA AZZUL S.A DE C. V

UBICACION:
CANTON SAN RAFAEL, CONDOMINIO RECREATIVO, LOMAS DE SAN BLAS, CALLE MAJAHUAL, POLIGONO 6, NUMERO 18, LA LIBERTAD COSTA, DEPARTAMENTO DE LA LIBERTAD


CONTENIDO:

PLANO TOPOGRAFICO

ESCALA: INDICADA	AREA TOTAL DEL TERRENO: AREA DE CONSTRUCCION:	384.76 M2 458.61 M2	FECHA: MARZO 2025	HOJA N°: T-01
---------------------	--	------------------------	----------------------	------------------

FIRMA Y SELLO DE PROFESIONALES RESPONSABLES		
DISEÑO ARQUITECTÓNICO: FIRMA: DISEÑO ARQUITECTÓNICO: SELLO:	DIRECTOR DE LA OBRA: FIRMA: DIRECTOR DE LA OBRA: SELLO:	RESPONSABLE DEL TRAMITE: FIRMA: RESPONSABLE DEL TRAMITE: SELLO:
REGISTRO NACIONAL DE ARQUITECTOS E INGENIEROS CARLA PATRICIA RODRIGUEZ DE CHOCOBAR A-2339 ARQUITECTA	REGISTRO NACIONAL DE ARQUITECTOS E INGENIEROS CARLOS FRANCISCO GALICIA MADIA A-3297 ARQUITECTO	REGISTRO NACIONAL DE ARQUITECTOS E INGENIEROS Morena Guadalupe Vasquez López A - 4576 ARQUITECTA

PERFIL 1 PROFILE

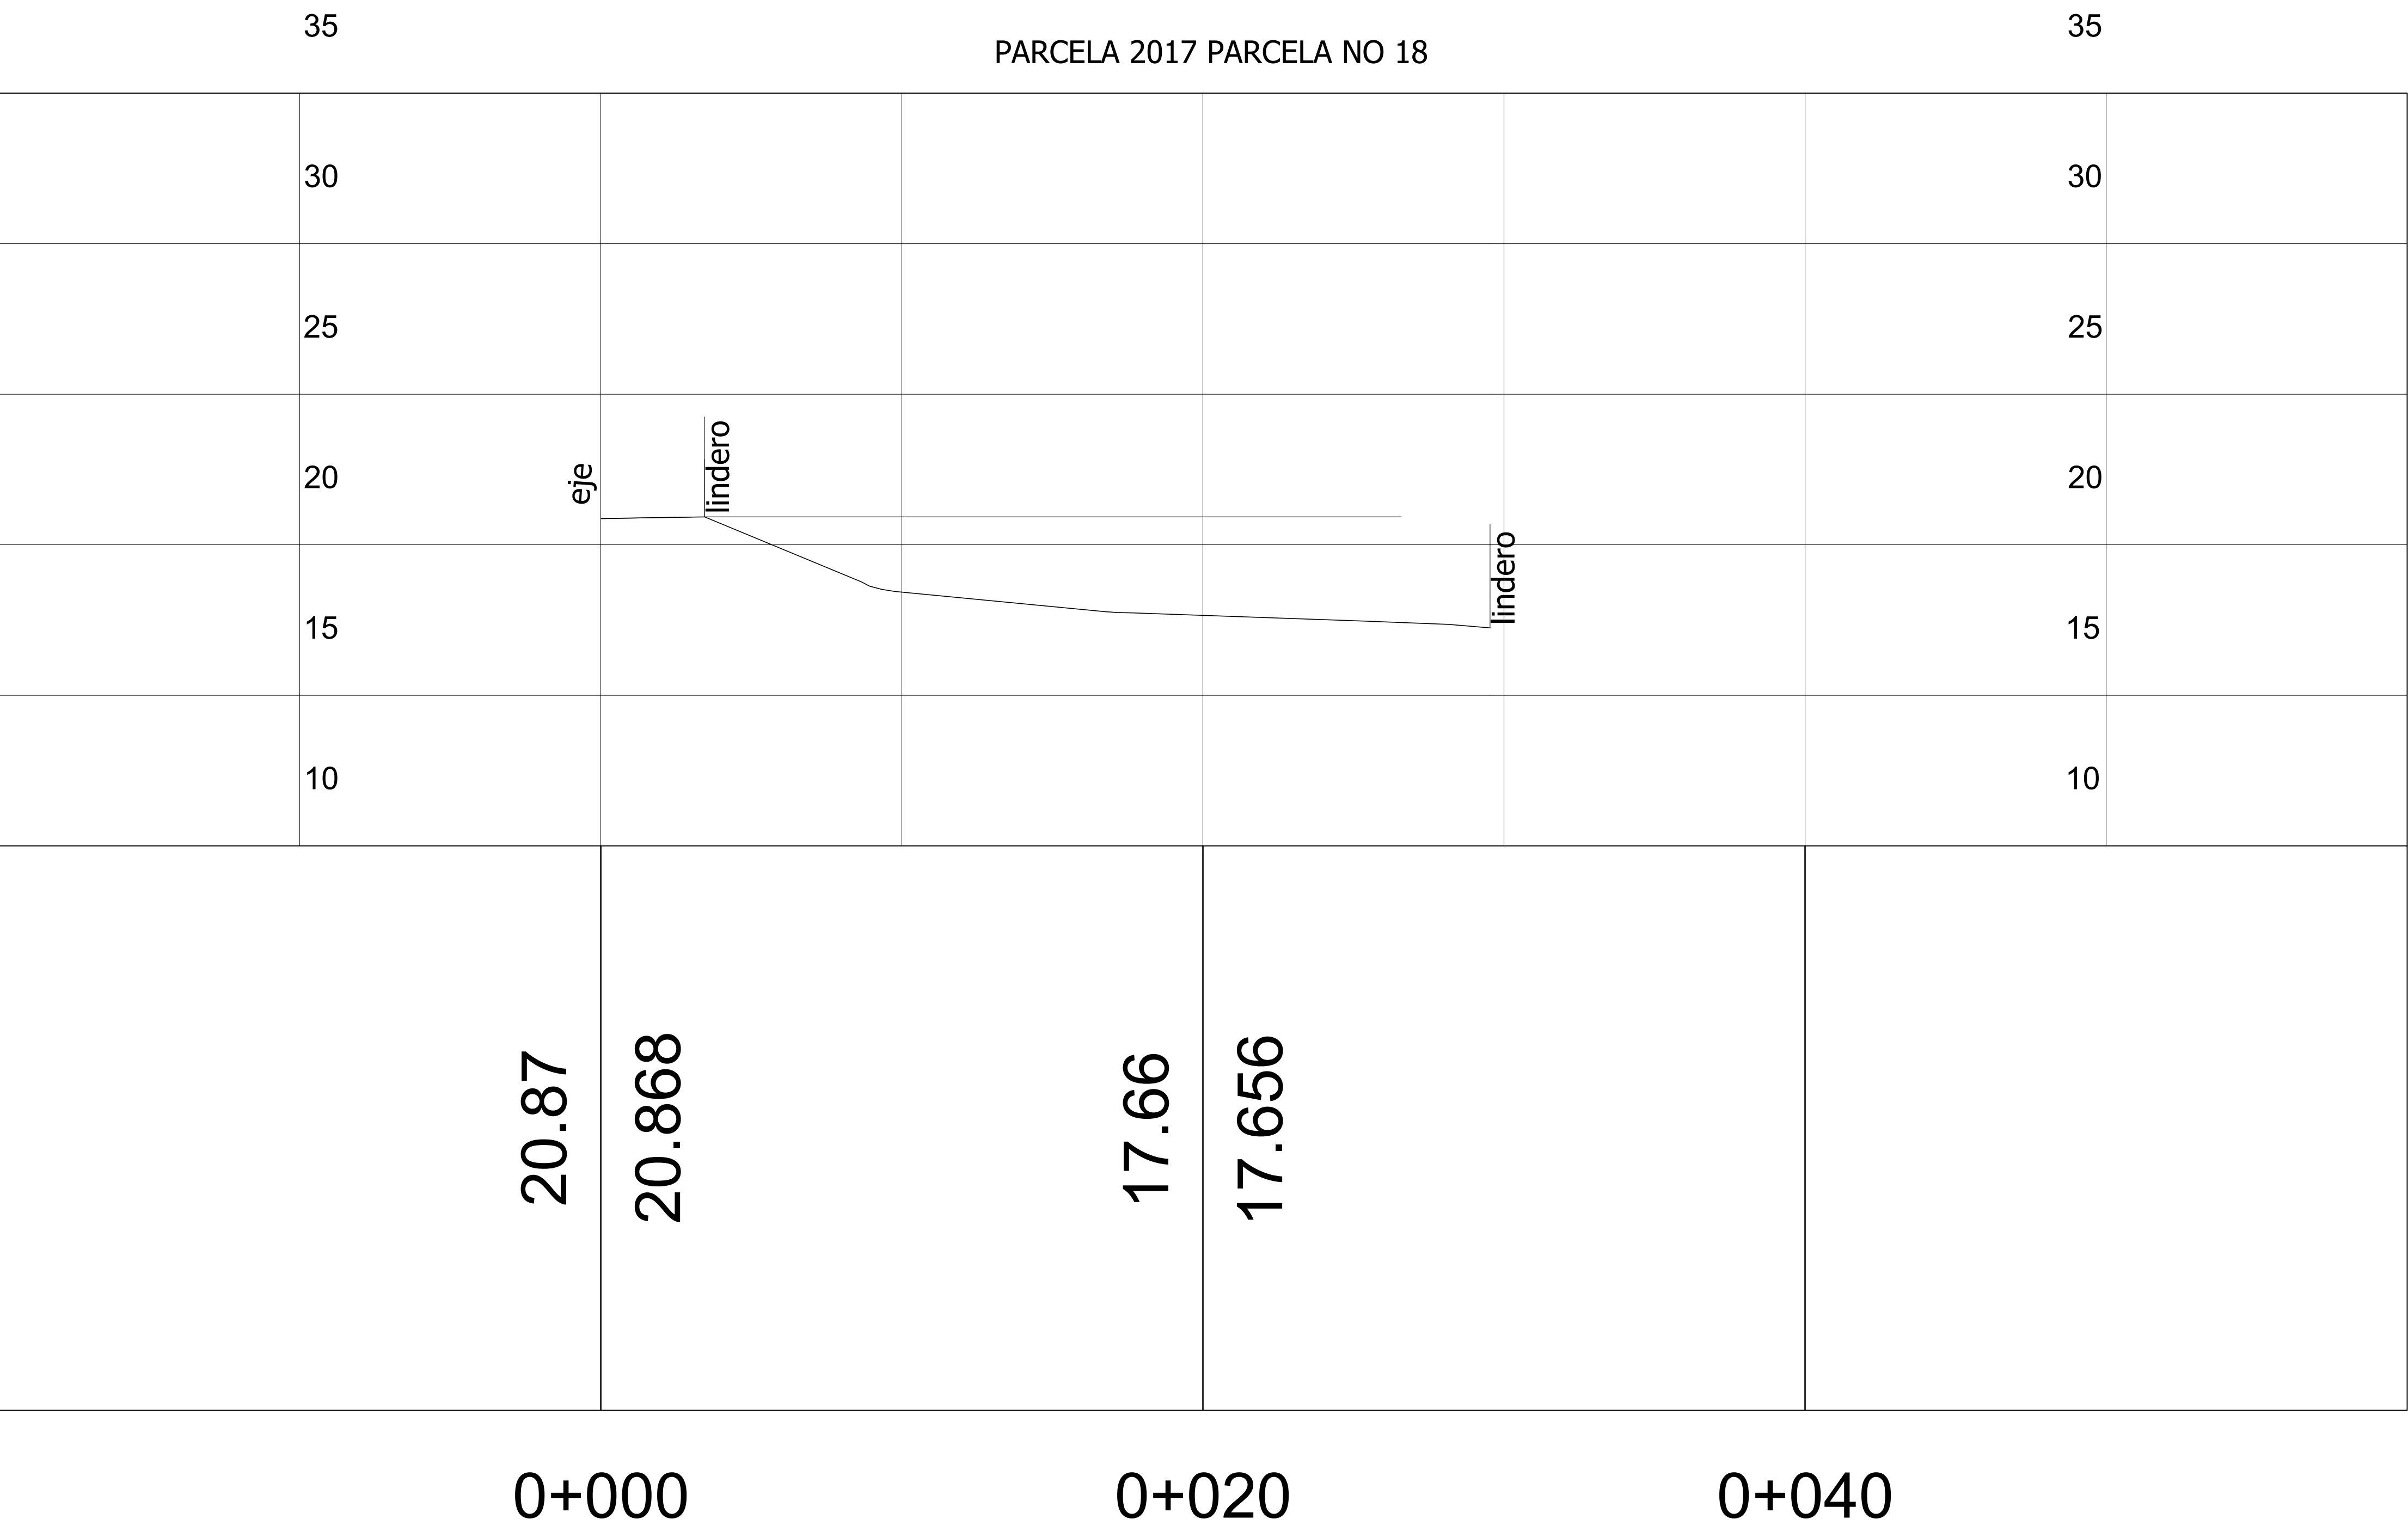

SELLOS DE APROBACION:

ESTE PLANO FORMA PARTE INTEGRAL DE LA RESOLUCION EMITIDA EN FECHA 24 DE JULIO DE 2025 EN FORMATO DIGITAL Y CORRESPONDE AL EXPEDIENTE DE PERMISO DE CONSTRUCCION REFERENCIA 0333-2025. PRESENTADO BAJO LA RESPONSABILIDAD DE LA ARQ MORENA GUADALUPE VASQUEZ LÓPEZ CON REGISTRO PROFESIONAL VMVDU A-4576.

PRESENTA:

ARQ. KARLA RODRIGUEZ DE CHOCOBAR

PROYECTO
CONSTRUCCION DE VIVIENDA DE DOS NIVELES
Y TERRAZA EMPRESA AZZUL
PROPIETARIOS
EMPRESA AZZUL S.A DE C.V
UBICACION:
CANTON SAN RAFAEL, CONDOMINIO RECREATIVO, LOMAS DE SAN BLAS, CALLE MAJAHUAL, POLIGONO 6, NUMERO 18, LA LIBERTAD COSTA. DEPARTAMENTO DE LA LIBERTAD

CONTENIDO:

PERFIL

ESCALA:
INDICADA

FECHA:
MARZO 2025

HOJA N°:
T-02

FIRMA Y SELLO DE PROFESIONALES RESPONSABLES

DISEÑO ARQUITECTÓNICO: FIRMA: DISEÑO ARQUITECTÓNICO: SELLO: 	DIRECTOR DE LA OBRA: FIRMA: DIRECTOR DE LA OBRA: SELLO: 	RESPONSABLE DEL TRAMITE: FIRMA: RESPONSABLE DEL TRAMITE: SELLO:
---	---	---